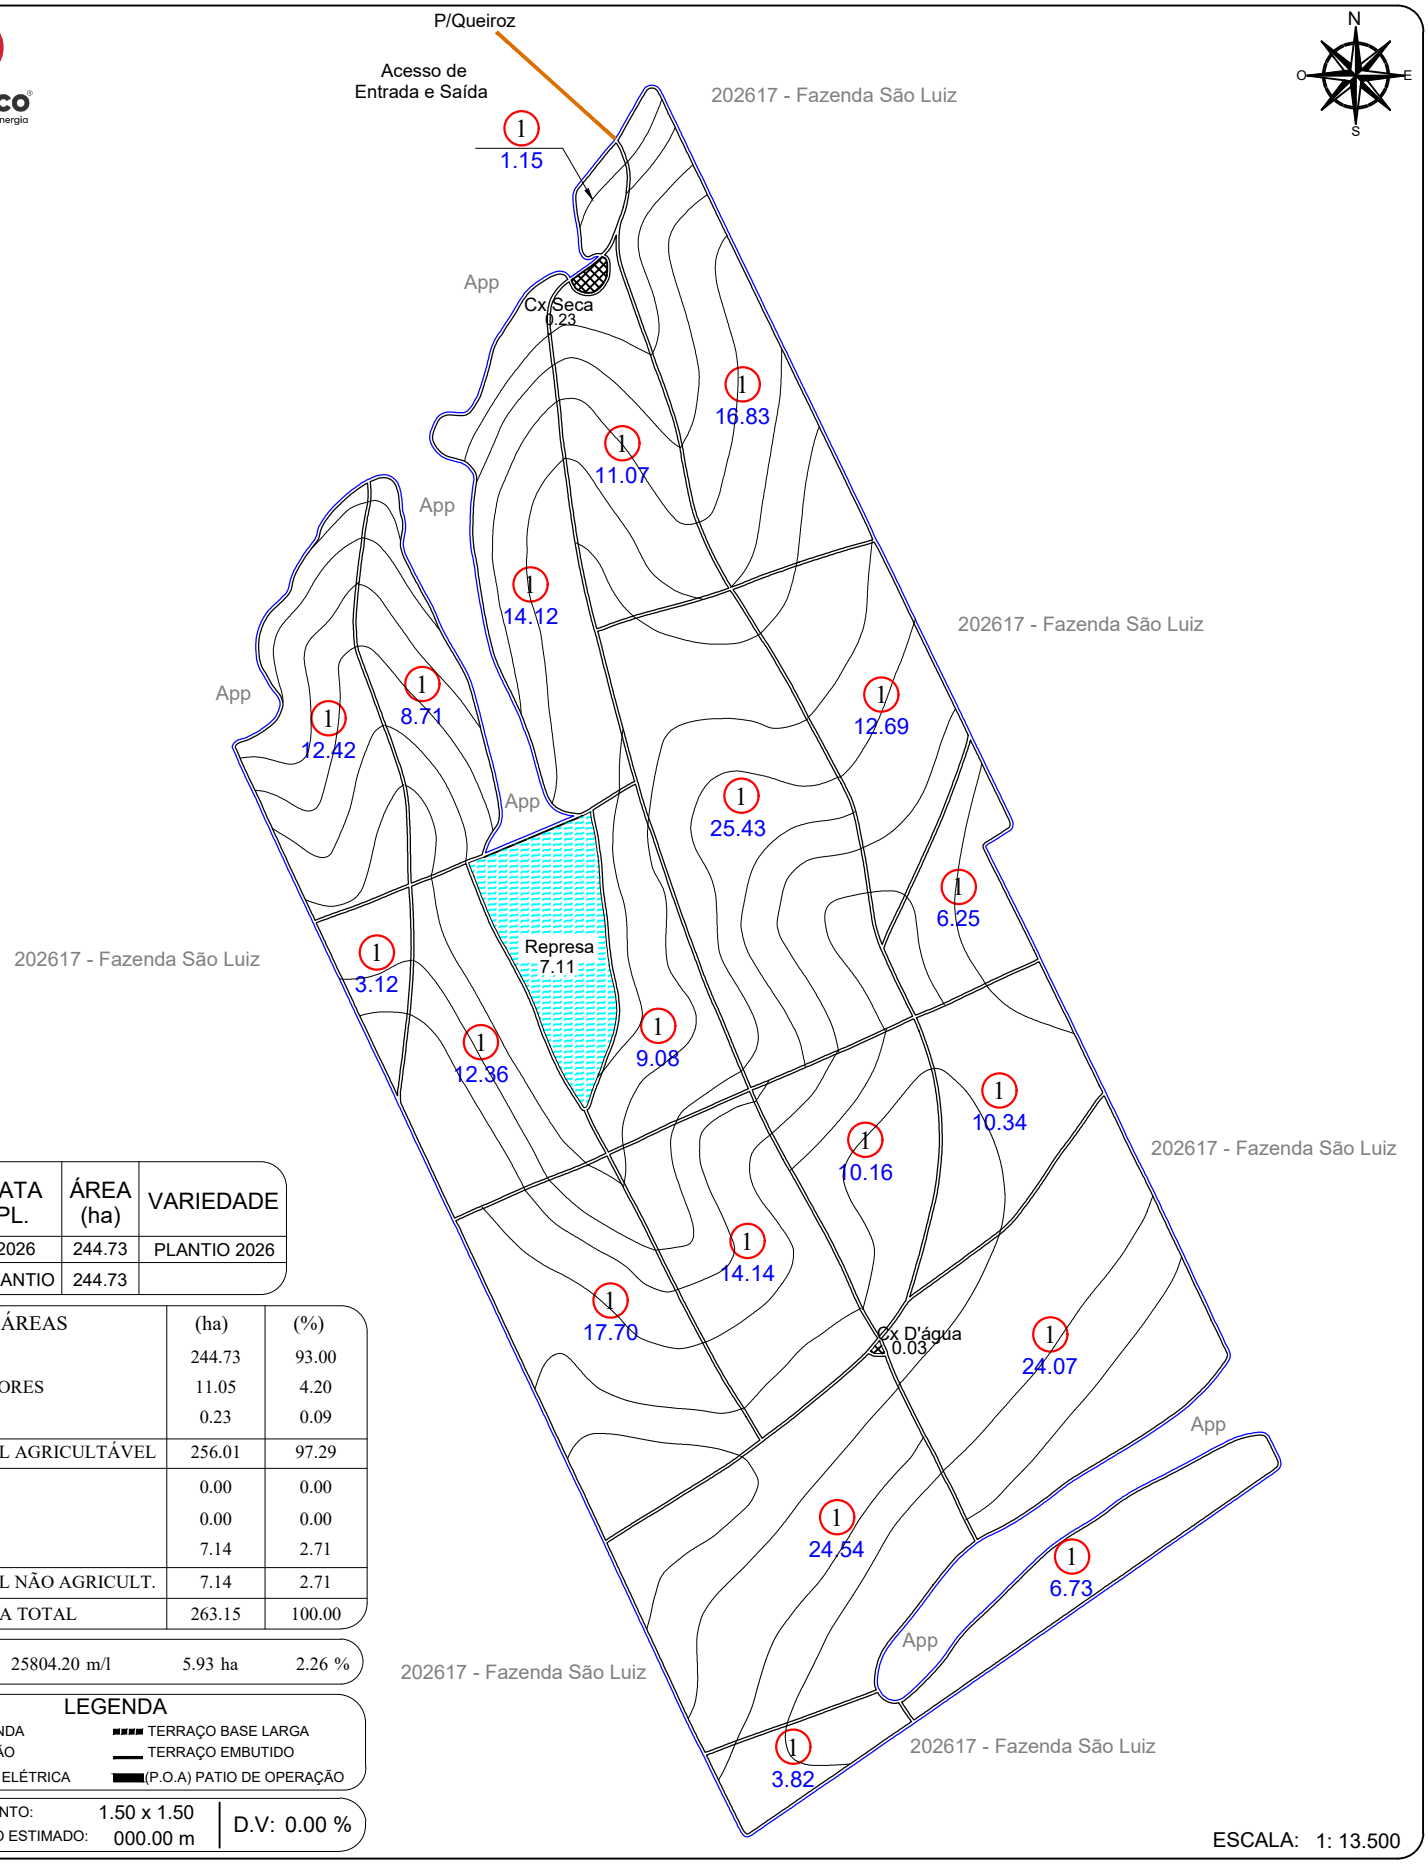


Nº TAL.	DATA PL.	ÁREA (ha)	VARIEDADE
1	2026	244.73	PLANTIO 2026
TOTAL PLANTIO		244.73	

ÁREAS	(ha)	(%)
PLANTIO	244.73	93.00
CARREADORES	11.05	4.20
OUTROS	0.23	0.09
SUB TOTAL AGRICULTÁVEL	256.01	97.29
AP.P.	0.00	0.00
ÁRVORES	0.00	0.00
OUTROS	7.14	2.71
SUB TOTAL NÃO AGRICULT.	7.14	2.71
ÁREA TOTAL	263.15	100.00

C. NÍVEL: 25804.20 m/l 5.93 ha 2.26 %


LEGENDA

- FAZENDA
- TALHÃO
- REDE ELÉTRICA
- TERRAÇO BASE LARGA
- TERRAÇO EMBUTIDO
- (P.O.A) PATIO DE OPERAÇÃO

ESPAÇAMENTO: 1.50 x 1.50
TIRO MÉDIO ESTIMADO: 000.00 m
D.V: 0.00 %

ESCALA: 1: 13.500

CROQUI DE ACESSO

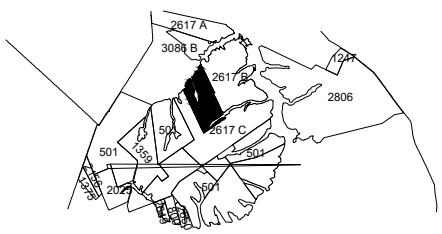

FAZENDA NOSSA SENHORA DE FÁTIMA

PROPRIETÁRIO: ALEXANDRE DE F. FERRAZ E OUTROS
COMPRADOR: CLEALCO
MUNICÍPIO: POMPÉIA - SP

DISTÂNCIAS (km):
UNID. I - Asfalto: 65.70 Terra.: 5.00
UNID.I I - Asfalto: 6.70 Terra.: 5.00

COORDENADAS: E(X): 579368.77 N(Y): 7577181.81
LAT: -21°54'28.0095" LONG: -50°13'53.7264"

LEVANTAMENTO VIA:
SATÉLITE
GPS / VANT
GOOGLE

CLEALCO - AÇÚCAR E ALCOOL S/A - DEPARTAMENTO DE GEOTECNOLOGIA

UNIDADE: II
PARTE: A/B
FUNDO AGRÍCOLA: 303086

M:\01-Mapa de safra\Mapas Atualizados\Terceiro\303086 - Fazenda Nossa Senhora de Fátima (Alexandre de Figueiredo Ferraz)\303086 A - Fazenda Nossa Senhora de Fátima (Alexandre de Figueiredo Ferraz).dwg

Fabiano Castro 05/03/26