
Clealco
Açúcar, Etanol e Energia

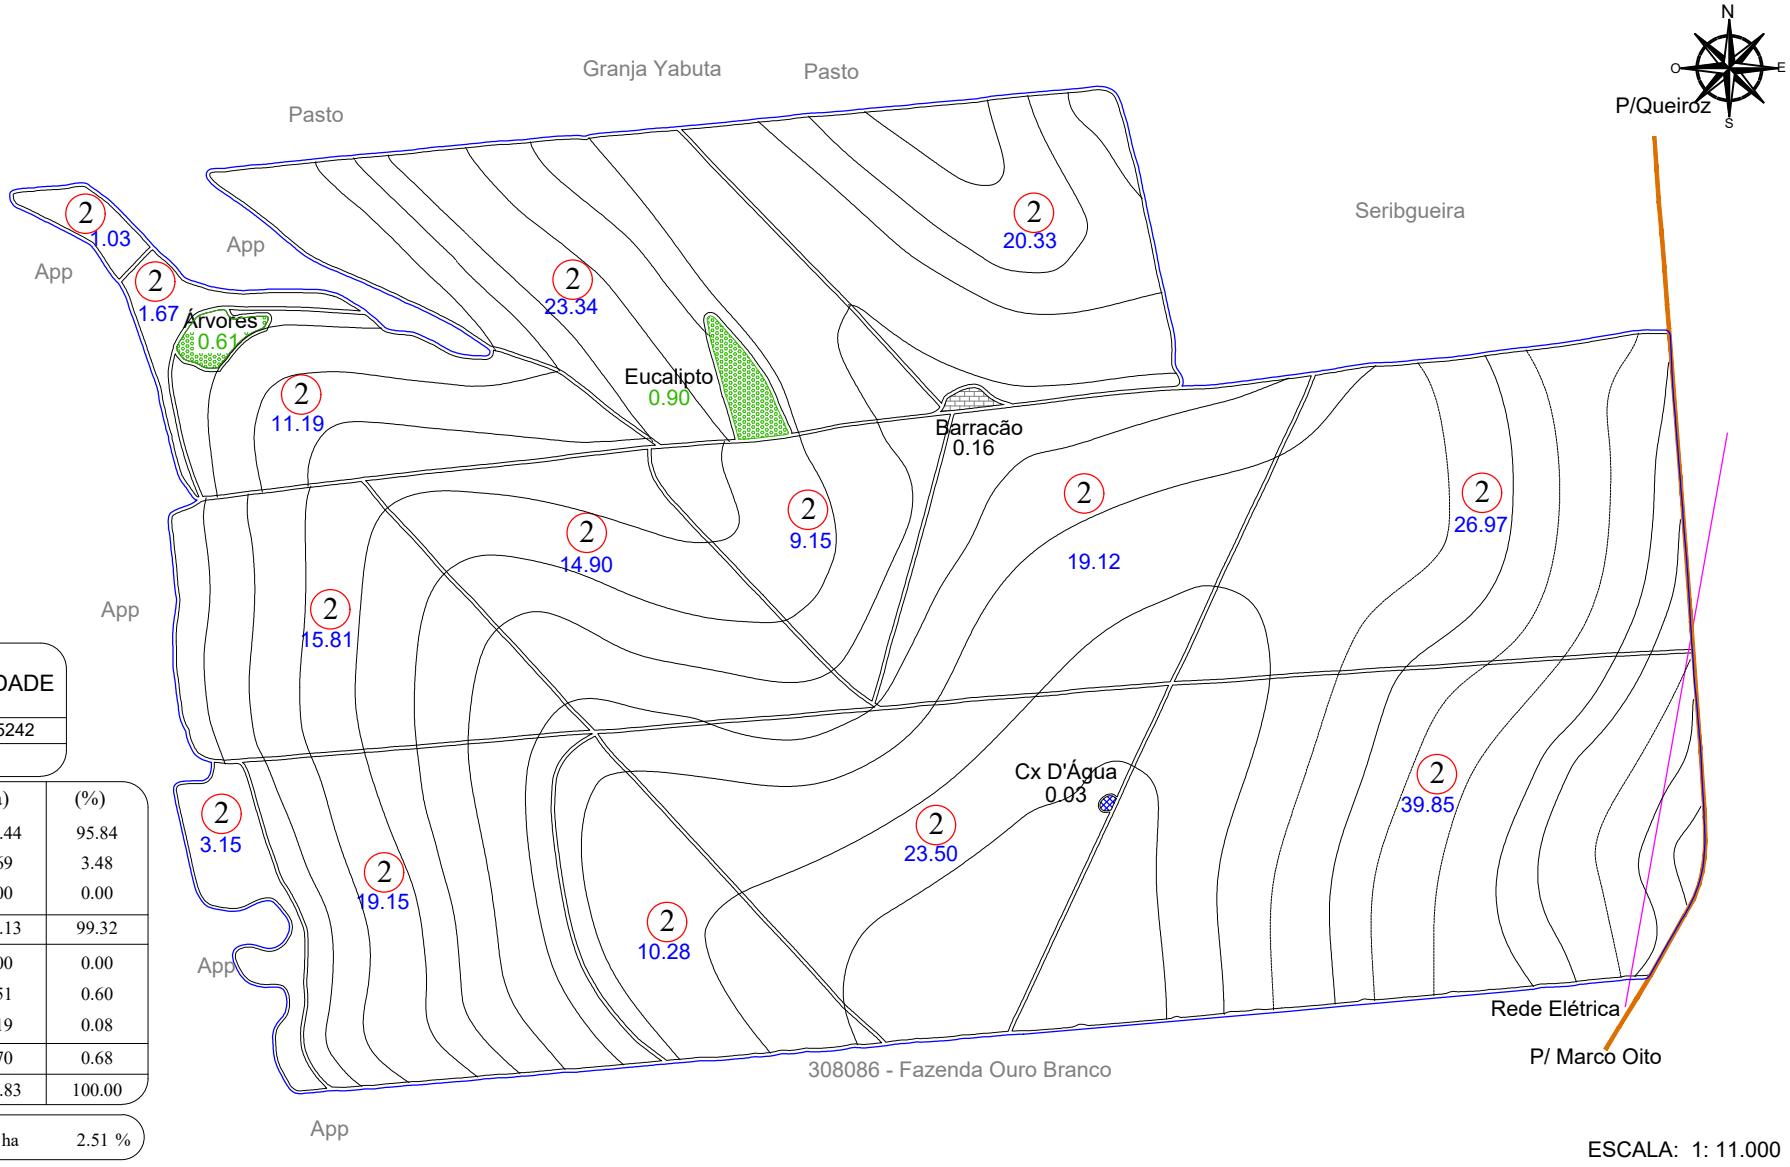

Nº TAL.	DATA PL.	ÁREA (ha)	VARIEDADE
2	04/2024	239.44	RB97 5242
TOTAL PLANTIO		239.44	

ÁREAS	(ha)	(%)
PLANTIO	239.44	95.84
CARREADORES	8.69	3.48
OUTROS	0.00	0.00
SUB TOTAL AGRICULTÁVEL	248.13	99.32
AP.P.	0.00	0.00
ÁRVORES	1.51	0.60
OUTROS	0.19	0.08
SUB TOTAL NÃO AGRICULT.	1.70	0.68
ÁREA TOTAL	249.83	100.00

C. NÍVEL:	27273.80 m/l	6.27 ha	2.51 %


ESCALA: 1: 11.000

LEGENDA

- FAZENDA
- TALHÃO
- REDE ELÉTRICA
- TERRAÇO BASE LARGA
- TERRAÇO EMBUTIDO
- VAZIO
- CARREGADO

ESPAÇAMENTO: 1.50 x 1.50
TIRO MÉDIO ESTIMADO: 000.00 m
D.V: 4.75 %

CROQUI DE ACESSO

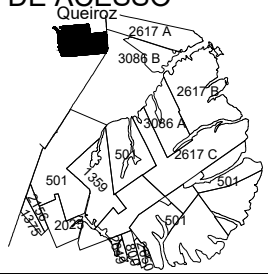

FAZENDA NOSSA SENHORA DE FÁTIMA

PROPRIETÁRIO: ALEXANDRE DE F. FERRAZ E OUTROS
COMPRADOR: CLEALCO
MUNICÍPIO: POMPÉIA - SP

DISTÂNCIAS (km):
UNID. I - Asfalto: 65.70 Terra.: 5.00
UNID.I I - Asfalto: 0.00 Terra.: 5.00

COORDENADAS: E(X): 576131.09 N(Y): 7580104.65
LAT: -21°52'53.4688" LONG: -50°15'47.0519"
CLEALCO - AÇÚCAR E ALCOOL S/A - DEPARTAMENTO DE GEOTECNOLOGIA

LEVANTAMENTO VIA:
SATÉLITE
GPS / VANT
GOOGLE

UNIDADE: II
PARTE: B/C
FUNDO AGRÍCOLA: 303086

M:\01-Mapa de safra\Mapas Atualizados\Terceiro\303086 - Fazenda Nossa Senhora de Fátima (Alexandre de Figueiredo Ferraz)\303086 B - Fazenda Nossa Senhora de Fátima (Alexandre de Figueiredo Ferraz).dwg

Bruno Gamboa 17/03/26