ZONA D.V.	Nº TAL.	DATA PL.	ÁREA (ha)	VAR.
	1		4.13	
	2		11.29	
	3		10.72	
	4		13.96	
	5		16.93	
	6		20.39	
	7		8.08	RB 975242
	8		6.51	
	9		11.07	
	10		20.17	
	11		22.07	
	12		31.67	
	13		16.31	
	14		22.47	CTC 04
	15		9.65	
	16		17.90	RB 975242
	17		26.58	
	18		0.53	
999 4.21 %	19	07/2022	23.66	CTC 04
	20		29.37	RB975242
	21		1.05	
	22		0.15	
	23		6.90	
	24		6.73	CTC 04
	25		2.51	
	26		5.56	
	27		7.57	
	28		17.98	
	29		10.84	RB 975242
	30		14.18	
	31		19.71	
	32		13.97	
	33		2.67	
	34		12.80	CTC 04
	35		9.36	
	36		16.87	
TOTAL PLANTIO			472.31	--------

ÁREAS	(ha)	(%)
PLANTIO	472.31	90.80
CARREADORES	14.71	2.83
OUTROS	0.00	0.00
SUB TOTAL AGRICULTÁVEL	487.02	93.63
AP.P.	0.00	0.00
ÁRVORES	0.15	0.03
OUTROS	33.01	6.35
SUB TOTAL NÃO AGRICULT.	33.16	6.37
ÁREA TOTAL	520.18	100.00

C. NÍVEL: 50671.69 m/l 11.65 ha 2.24 %


LEGENDA

- FAZENDA
- TALHÃO
- CURVA DE NÍVEL
- CARREADOR
- CONFRONTANTE
- REDE ELÉTRICA
- TRAJETO VAZIO
- TRAJETO CARREGADO

PLANTIO MANUAL - ESPAÇAMENTO: 1.50 X 1.50
TIRO MÉDIO ESTIMADO: 000.00m


Clealco
Açúcar, Etanol e Energia

NM

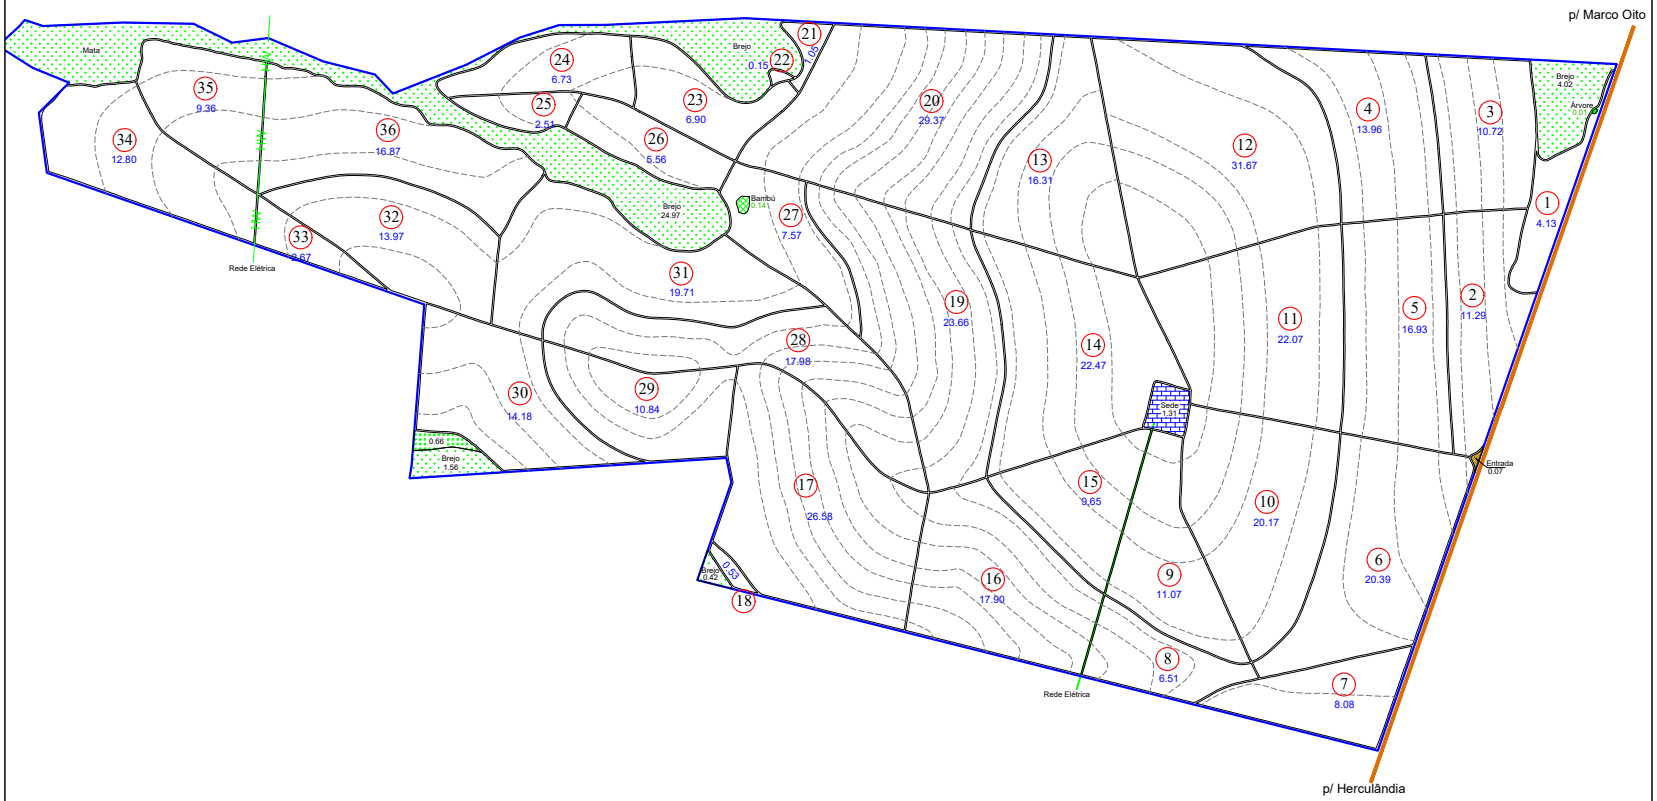

ESCALA: 1: 21.000

CROQUI DE ACESSO

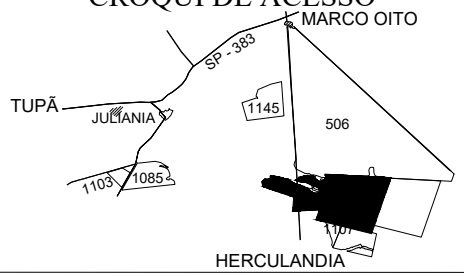

FAZENDA PLANALTO

PROPRIETÁRIO: FELIPE DE F. FERRAZ
COMPRADOR: CLEALCO S/A
MUNICÍPIO: HERCULÂNDIA

DISTÂNCIAS (km):
UNID. I - Asfalto: 32.50 Terra.: 30.50
UNID.I I - Asfalto: 16.50 Terra.: 8.00
UNID. III -Asfalto: 59.00 Terra.: 19.00

COORDENADAS: E(X): 572447.1149 N(Y): 7575353.750
LAT: 21°55'28,5398" LONG: 50°17'54,6641"

CLEALCO - AÇÚCAR E ALCOOL S/A - DEPARTAMENTO DE TOPOGRAFIA

UNIDADE: I
PARTE: A/A
FUNDO AGRÍCOLA: 303252

M:\01-Mapa de safra\Mapas Atualizados\Terceiro\303252 - Fazenda Planalto (Felipe de Figueiredo Ferraz)\303252 - Fazenda Planalto (Felipe de Figueiredo Ferraz).dwg

Fernanda Bezerra 12/04/23