ZONA D.V.	Nº TAL.	DATA PL.	ÁREA (ha)	VARIEDADE
3.25%	1	03/2025	44.96	DIVERSAS
	2		48.66	
	3	04/2024	4.53	CTC 9001
	4	03/2025	30.56	DIVERSAS
	5		19.84	
	6		14.89	
	7		14.26	
	8		27.18	
	9	04/2024	5.41	CTC 9001
	10	06/2023	8.34	
TOTAL			218.63	--------


ÁREAS	(ha)	(%)
PLANTIO	218.63	96.29
CARREADORES	8.01	3.53
OUTROS	0.00	0.00
SUB TOTAL AGRICULTÁVEL	226.64	99.82
AP.P.	0.00	0.00
ÁRVORES	0.41	0.18
OUTROS	0.00	0.00
SUB TOTAL NÃO AGRICULT.	0.41	0.18
ÁREA TOTAL	227.05	100.00

C. NÍVEL: 17575.05 m/l 4.04 ha 1.78 %


LEGENDA

- FAZENDA
- TALHÃO
- CURVA DE NÍVEL
- CARREADOR
- CONFRONTANTE
- REDE ELÉTRICA
- TRAJETO VAZIO
- TRAJETO CARREGADO

PLANTIO MANUAL - ESPAÇAMENTO: 1.50 X 1.50

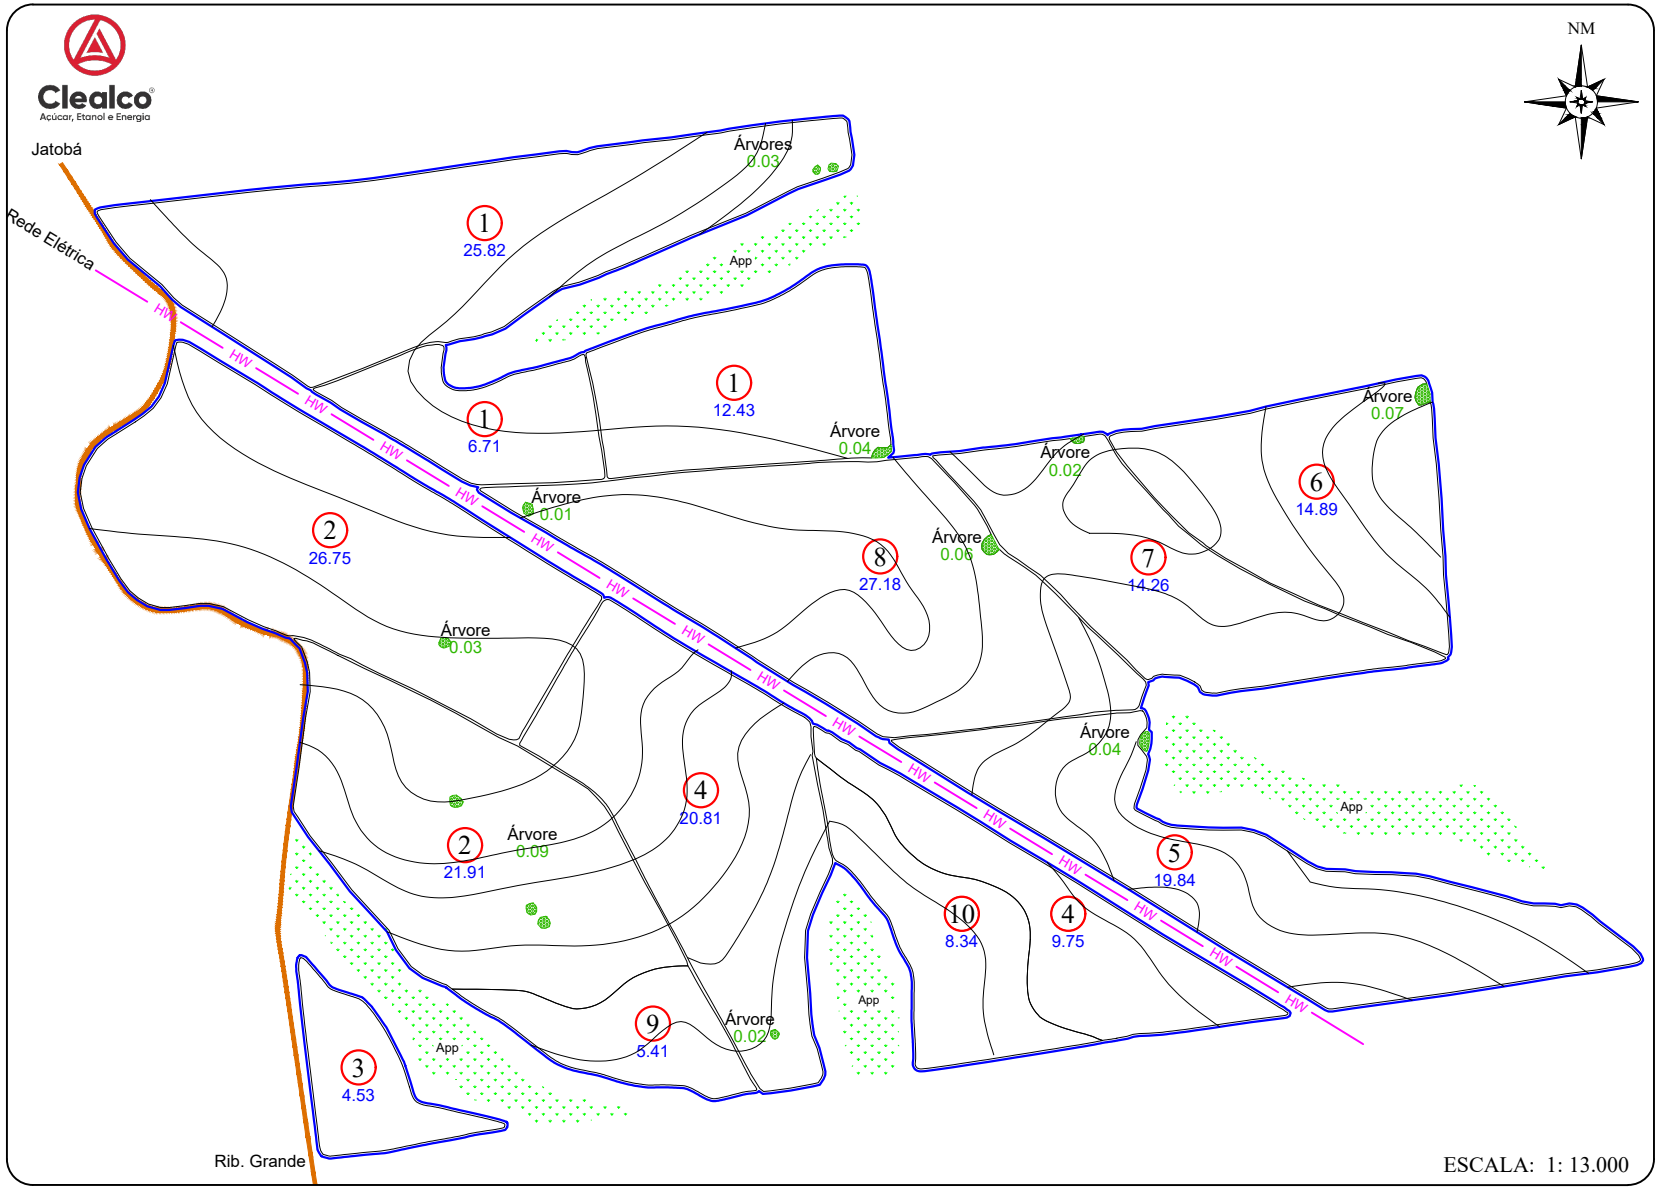

CROQUI DE ACESSO

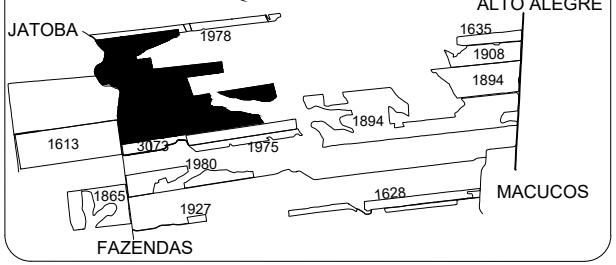

FAZENDA SANTA MARIA

PROPRIETÁRIO: WILLIAN AVILA PEREIRA
COMPRADOR: CLEALCO S/A
MUNICÍPIO: ALTO ALEGRE

DISTÂNCIAS (km):
UNID. I - Asfalto: 42.00 Terra.: 3.70
UNID.I I - Asfalto: 31.00 Terra.: 3.90
UNID. III -Asfalto: 24.50 Terra.: 3.00

COORDENADAS: E(X): 580781.06 N(Y): 7605757.17
LAT: -21°38'58.4419" LONG: -50°13'9.5415"

CLEALCO - AÇÚCAR E ALCOOL S/A - DEPARTAMENTO DE TOPOGRAFIA

UNIDADE: II
PARTE: A/A
FUNDO AGRÍCOLA: 303273