
Clealco
Açúcar, Etanol e Energia

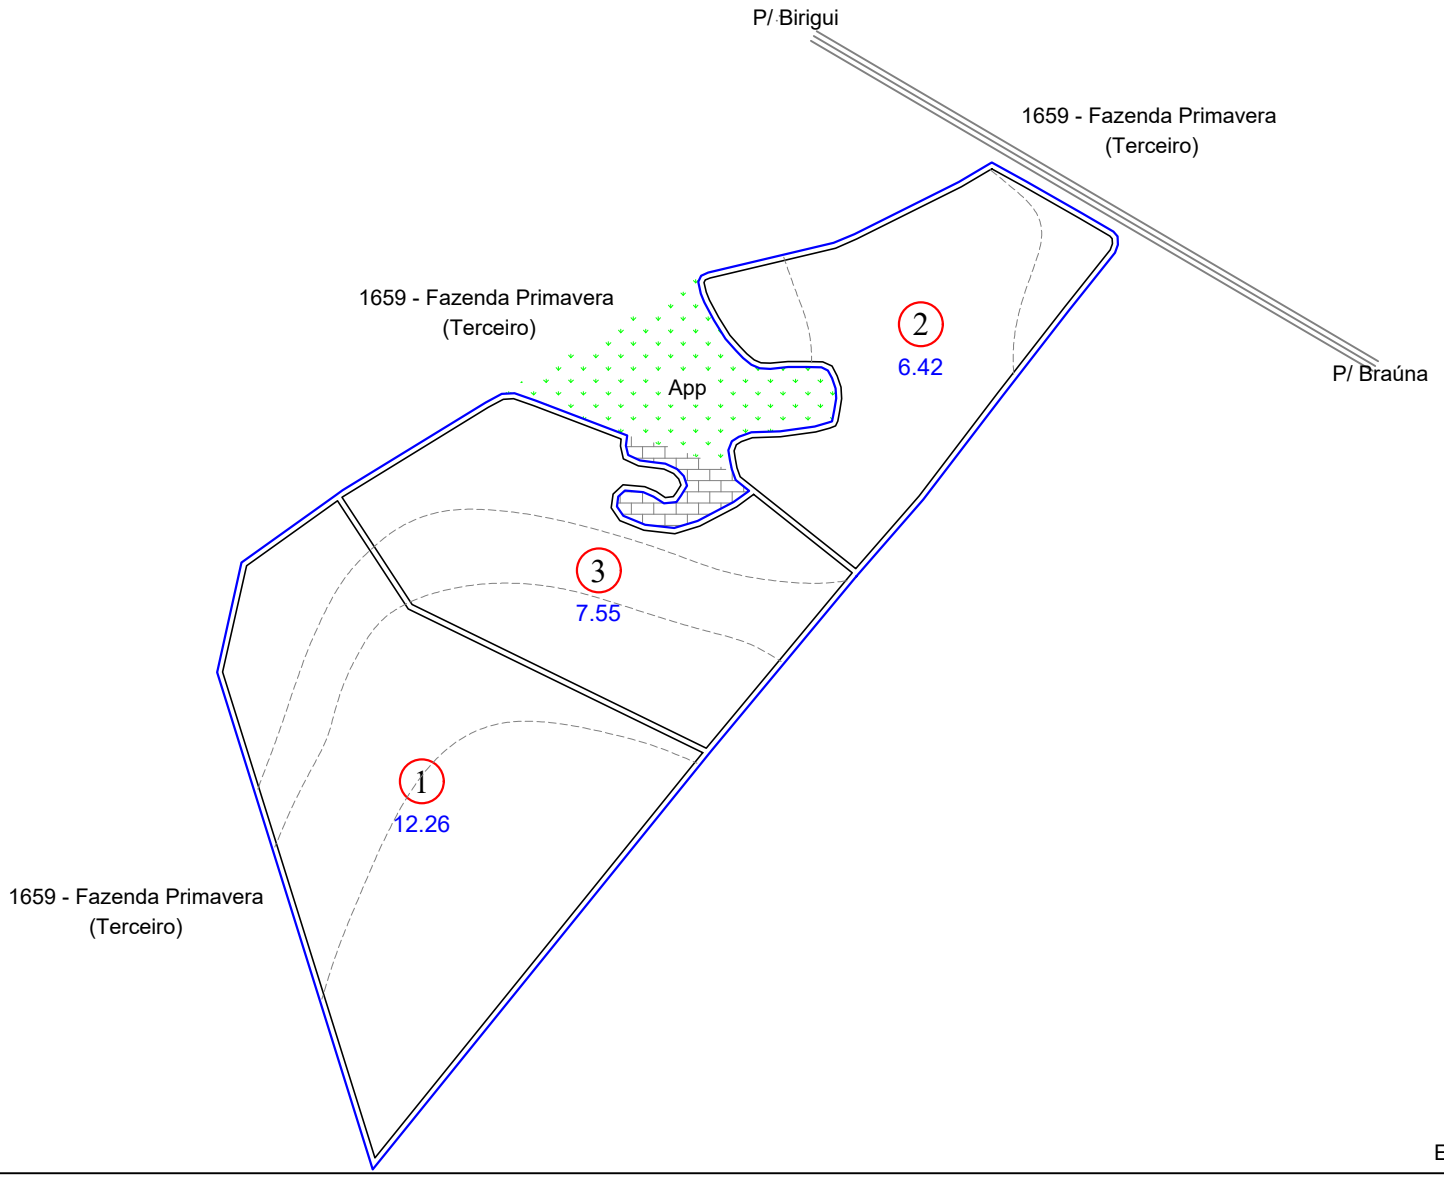

Nº TAL.	DATA PL.	ÁREA (ha)	VARIEDADE
1	04/2020	12.26	CTC 04
2	2026	6.42	REFORMA
3	04/2022	7.55	RB 975201
TOTAL PLANTIO		26.23	

ÁREAS	(ha)	(%)
PLANTIO	26.23	93.50
CARREADORES	1.82	6.50
OUTROS	0.00	0.00
SUB TOTAL AGRICULTÁVEL	28.05	100.00
AP.P.	0.00	0.00
ÁRVORES	0.00	0.00
OUTROS	0.00	0.00
SUB TOTAL NÃO AGRICULT.	0.00	0.00
ÁREA TOTAL	28.05	100.00

C. NÍVEL: 0.00 m/l 0.00 ha 0.00 %


ESCALA: 1: 7.000

LEGENDA

- FAZENDA
- TALHÃO
- REDE ELÉTRICA
- TERRAÇO BASE LARGA
- TERRAÇO EMBUTIDO

ESPAÇAMENTO: 1.50 x 1.50 D.V: 4.50 %
TIRO MÉDIO ESTIMADO: 250.38 m

CROQUI DE ACESSO

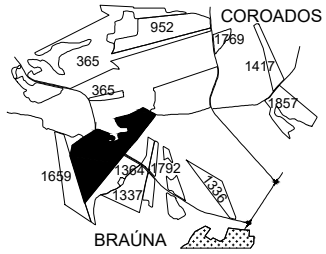

SÍTIO NOSSA SENHORA APARECIDA

PROPRIETÁRIO: LUIZ AUGUSTO DANELUCCI
COMPRADOR: CLEALCO
MUNICÍPIO: COROADOS - SP

DISTÂNCIAS (km):
UNID. I - Asfalto: 23.50 Terra.: 0.70
UNID.I I - Asfalto: 73.50 Terra.: 1.00

COORDENADAS: E(X): 568373.83 N(Y): 7623642.04
LAT: -21°29'18.6278" LONG: -50°20'23.8136"
CLEALCO - AÇÚCAR E ALCOOL S/A - DEPARTAMENTO DE GEOTECNOLOGIA

LEVANTAMENTO VIA:
SATÉLITE
GPS / VANT
GOOGLE

UNIDADE: I
PARTE: A/A
FUNDO AGRÍCOLA: 303291

M:\01-Mapa de safra\Mapas Atualizados\Terceiro\303291 - Sítio Nossa Senhora Aparecida (Luiz Augusto Danelucci)\303291 - Sítio Nossa Senhora Aparecida (Luiz Augusto Danelucci).dwg

Fabiano Castro 05/03/26