D.V.	Nº TAL.	DATA PL.	ÁREA (ha)	VARIEDADE
5.27%	1	06/2024	61.67	RB867515
TOTAL PLANTIO			61.67	

ÁREAS	(ha)	(%)
PLANTIO	61.67	96.97
CARREADORES	1.91	3.00
OUTROS	0.00	0.00
SUB TOTAL AGRICULTÁVEL	63.58	99.97
AP.P.	0.00	0.00
ÁRVORES	0.02	0.03
OUTROS	0.00	0.00
SUB TOTAL NÃO AGRICULT.	0.02	0.03
ÁREA TOTAL	63.60	100.00

C. NÍVEL:	8014.42 m/l	1.84 ha	2.90 %

LEGENDA

▬ FAZENDA	▪▪▪▪ TERRAÇO BASE LARGA
▬ TALHÃO	── TERRAÇO EMBUTIDO
-·- REDE ELÉTRICA	

ESPAÇAMENTO: 1.50 x 1.50

TIRO MÉDIO ESTIMADO: 325.55 m

Clealco
Açúcar, Etanol e Energia

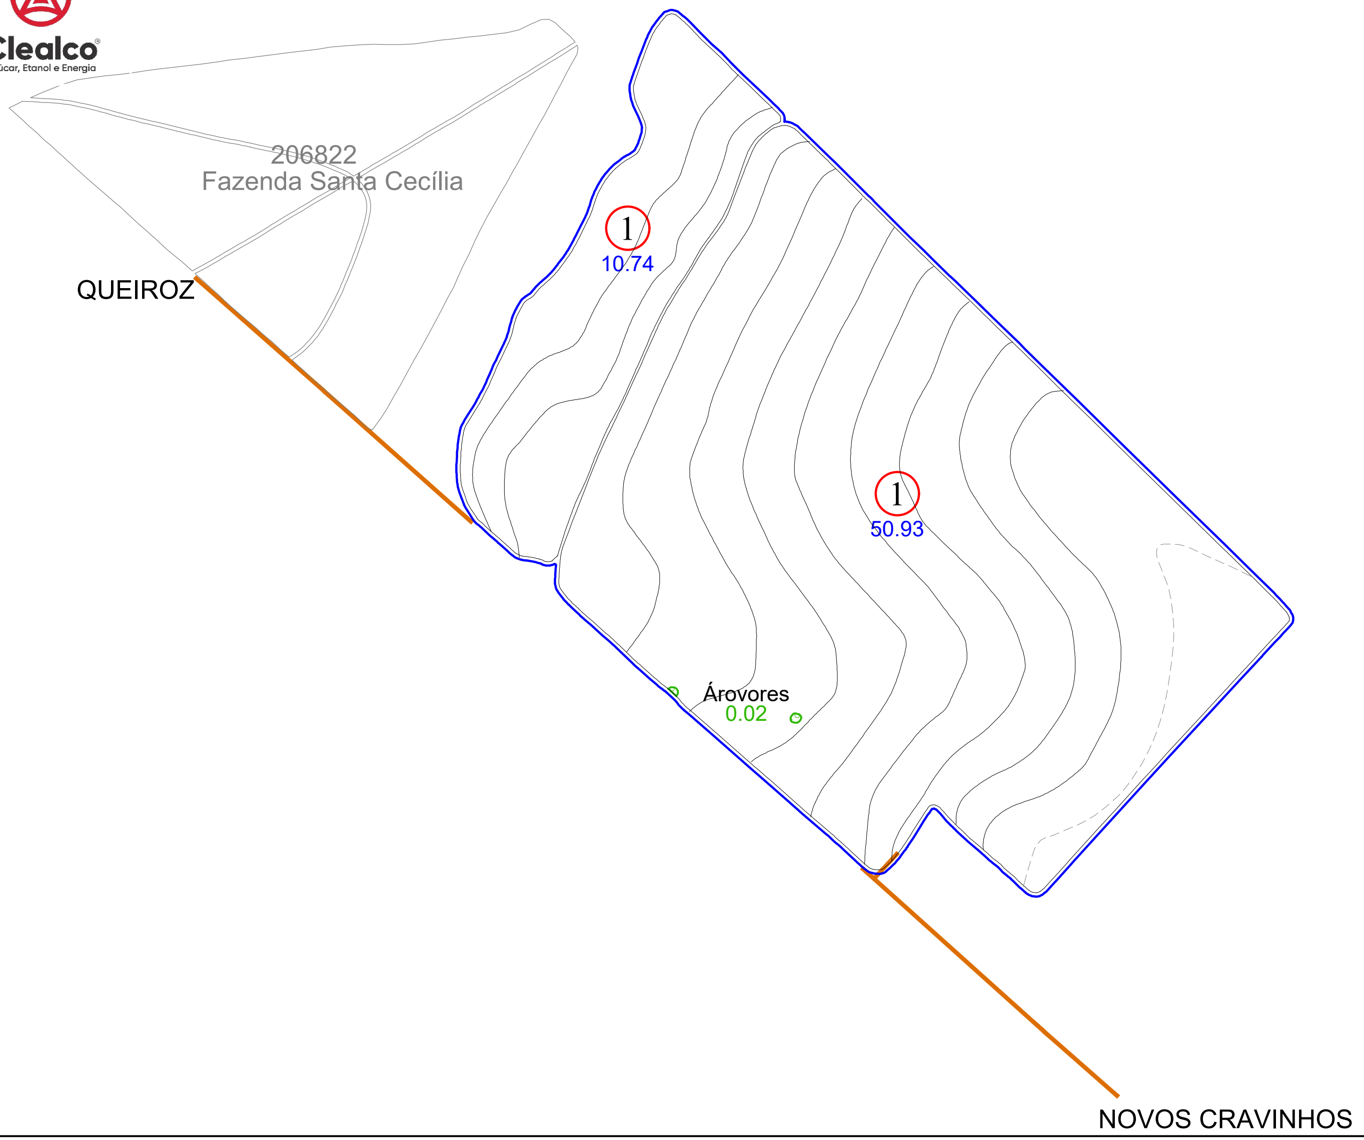

ESCALA: 1: 10.000

CROQUI DE ACESSO

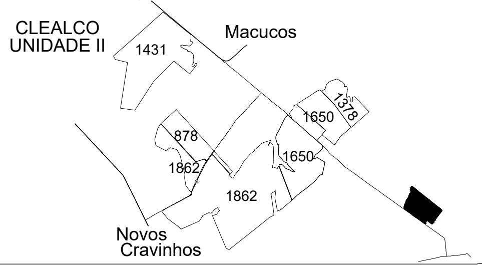

FAZENDA SANTA CECÍLIA

PROPRIETÁRIO: ADRIANO M. DE ANDRADE
COMPRADOR: CLEALCO S/A
MUNICÍPIO: QUEIROZ

DISTÂNCIAS (km):

UNID. I -	Asfalto:	72.00	Terra.:	00.00
UNID.I I -	Asfalto:	6.10	Terra.:	7.43
UNID. III -	Asfalto:	64.00	Terra.:	00.00

COORDENADAS:	E(X):	590639.45	N(Y):	7583142.47
	LAT:	-21°51'12.1979"	LONG:	-50°7'22.1228"

CLEALCO - AÇÚCAR E ALCOOL S/A - DEPARTAMENTO DE GEOTECNOLOGIA

UNIDADE:
II

PARTE:
A/A

FUNDO AGRÍCOLA:
303313

M:\01-Mapa de safra\Mapas Atualizados\Terceiro\303313 - Fazenda Santa Cecilia (Adriano Marco de Andrade) \303313 - Fazenda Santa Cecilia (Adriano Marco de Andrade) .dwg

Bruno Gamboa 05/12/24