ZONA	Nº TAL.	DATA PL.	ÁREA (ha)	VAR.
999	1	06/2021	39.97	RB 97 5201
	2		36.39	
	3		22.93	
	4		40.13	RB 97 5242
	5		37.97	
TOTAL PLANTIO			177.39	--------


ÁREAS	(ha)	(%)
PLANTIO	177.39	97.24
CARREADORES	4.92	2.70
OUTROS	0.00	0.00
SUB TOTAL AGRICULTÁVEL	182.31	99.94
AP.P.	0.00	0.00
MATA	0.00	0.00
OUTROS	0.11	0.06
SUB TOTAL NÃO AGRICULT.	0.11	0.06
ÁREA TOTAL	182.42	100.00

C. NÍVEL: 9584.13 m/l 2.20 ha 1.21 %


LEGENDA

- FAZENDA
- TALHÃO
- CURVA DE NÍVEL
- CARREADOR
- CONFRONTANTE
- REDE ELÉTRICA
- TRAJETO VAZIO
- TRAJETO CARREGADO

PLANTIO MANUAL - ESPAÇAMENTO: 1.50 X 1.50

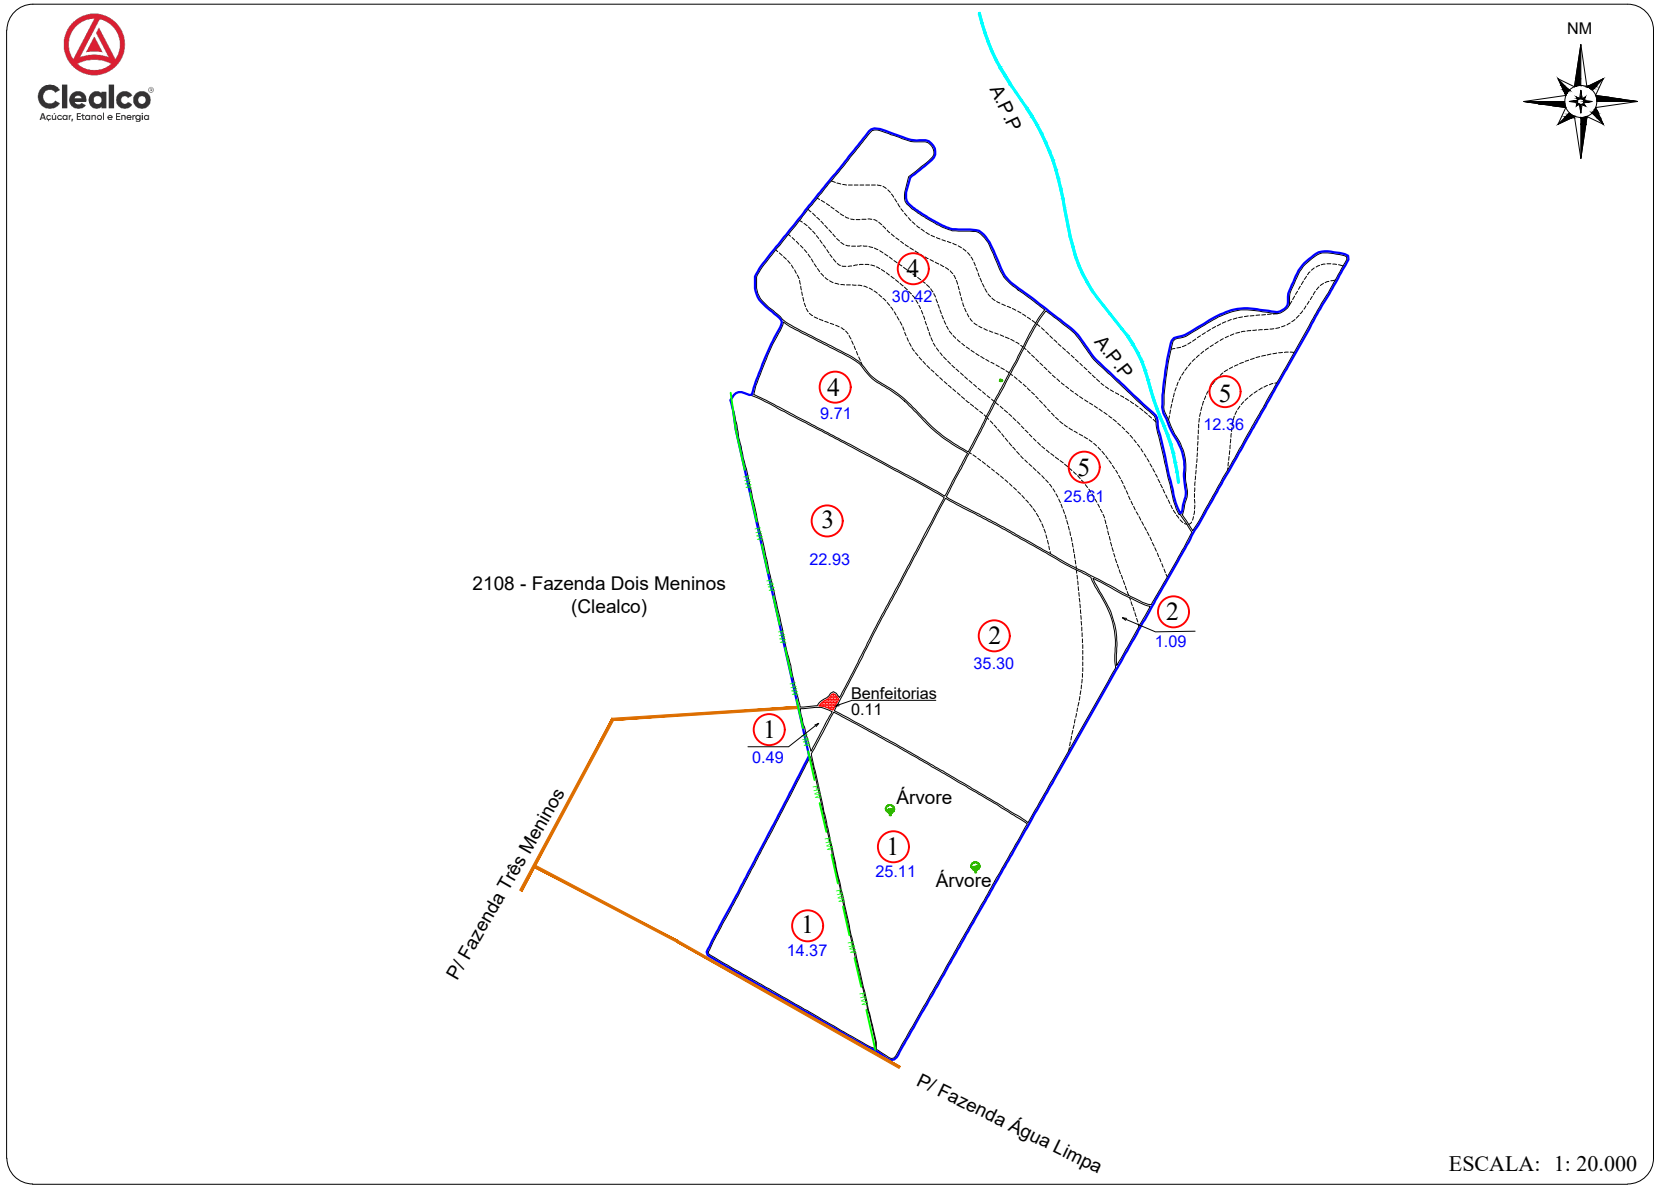

CROQUI DE ACESSO

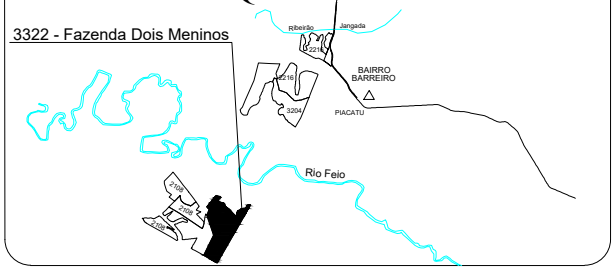

FAZENDA DOIS MENINOS

PROPRIETÁRIO: ODIR ROMANO
COMPRADOR: CLEALCO S/A
MUNICÍPIO: RINÓPOLIS

DISTÂNCIAS (km):
UNID. I - Asfalto: 45.60 Terra.: 0.70
UNID.I I - Asfalto: 81.00 Terra.: 6.50
UNID. III -Asfalto: 85.60 Terra.: 0.70

COORDENADAS: E(X): 525.141,05 N(Y): 7.612.040,05
LAT: 21°35'40.0515" LONG: 50°45'25.6295"

CLEALCO - AÇÚCAR E ALCOOL S/A - DEPARTAMENTO DE TOPOGRAFIA

UNIDADE: I
PARTE: A/A
FUNDO AGRÍCOLA: 303322

M:\01-Mapa de safra\Mapas Atualizados\Terceiro\303322 - Fazenda Dois Meninos (Odir Romano)\303322 - Fazenda Dois Meninos (Odir Romano).dwg

Pedro Becker 02/09/21