

Clealco
Açúcar, Etanol e Energia

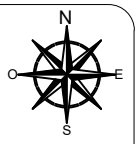

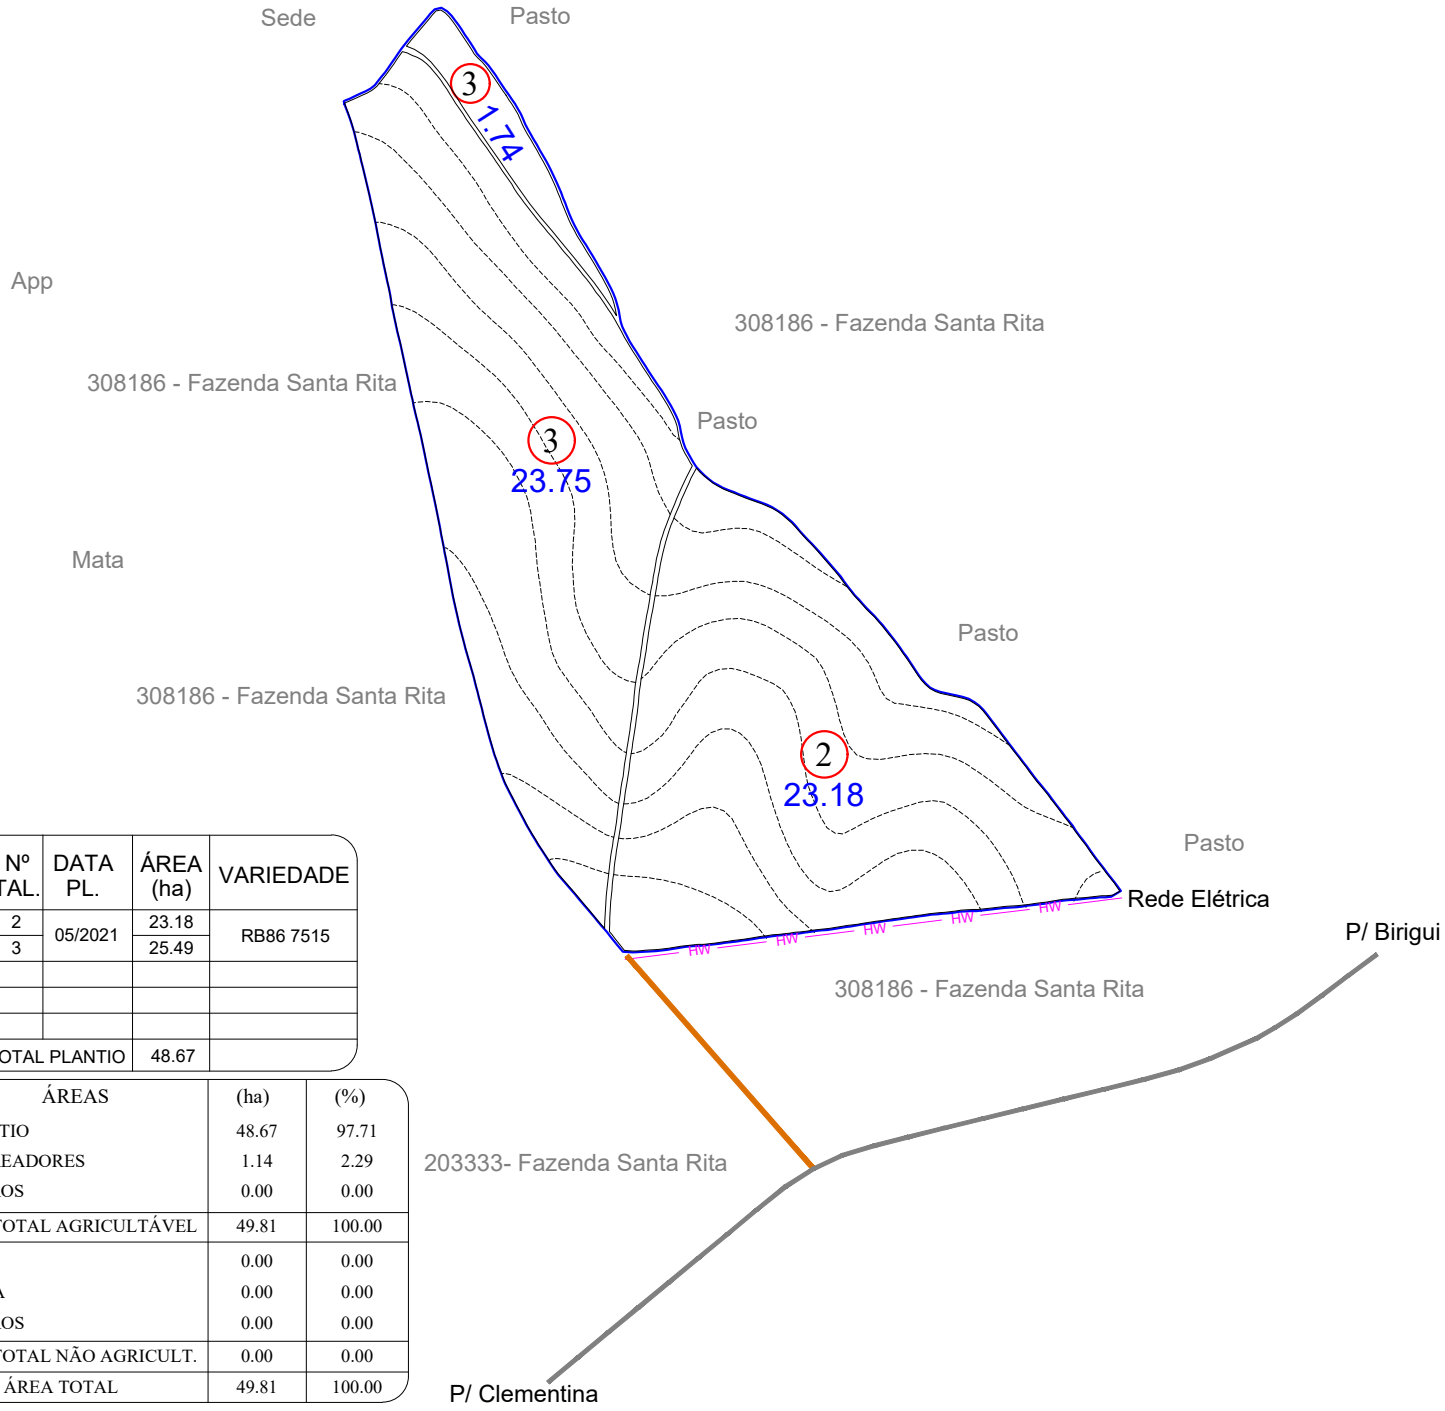

ZONA	Nº TAL.	DATA PL.	ÁREA (ha)	VARIEDADE
999	2	05/2021	23.18	RB86 7515
	3		25.49	
TOTAL PLANTIO			48.67	

ÁREAS	(ha)	(%)
PLANTIO	48.67	97.71
CARREADORES	1.14	2.29
OUTROS	0.00	0.00
SUB TOTAL AGRICULTÁVEL	49.81	100.00
AP.P.	0.00	0.00
MATA	0.00	0.00
OUTROS	0.00	0.00
SUB TOTAL NÃO AGRICULT.	0.00	0.00
ÁREA TOTAL	49.81	100.00

C. NÍVEL: 7323.05 m/l 1.68 ha 3.38 %


LEGENDA

- FAZENDA
- TALHÃO
- REDE ELÉTRICA
- TERRAÇO BASE LARGA
- TERRAÇO EMBUTIDO
- (P.O.A) PATIO DE OPERAÇÃO

ESPAÇAMENTO: 1.50 x 1.50
TIRO MÉDIO ESTIMADO: 000.00 m
D.V: 0.00 %

ESCALA: 1: 10.000

CROQUI DE ACESSO

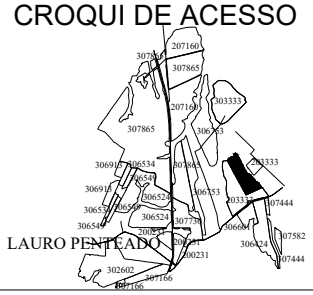

LAURO PENTEADO

FAZENDA SANTA RITA

PROPRIETÁRIO: ALCEU TOSSATO
COMPRADOR: CLEALCO
MUNICÍPIO: COROADOS - SP

DISTÂNCIAS (km):
UNID. I - Asfalto: 11.20 Terra.: 1.20
UNID.I I - Asfalto: 67.00 Terra.: 1.20

COORDENADAS: E(X): 561240.29 N(Y): 7623010.77
LAT: -21°29'40.0876" LONG: -50°24'31.6309"

CLEALCO - AÇÚCAR E ALCOOL S/A - DEPARTAMENTO DE GEOTECNOLOGIA

LEVANTAMENTO VIA:
- SATÉLITE
- GPS / VANT
- GOOGLE

UNIDADE: I
PARTE: A/B
FUNDO AGRÍCOLA: 303333

M:\01-Mapa de safra\Mapas Atualizados\Terceiro\303333 - Fazenda Santa Rita (Espólio de Alceu Tossato)\303333 A - Fazenda Santa Rita (Espolio de Alceu Tossato).dwg

Bruno Gamboa 19/11/25