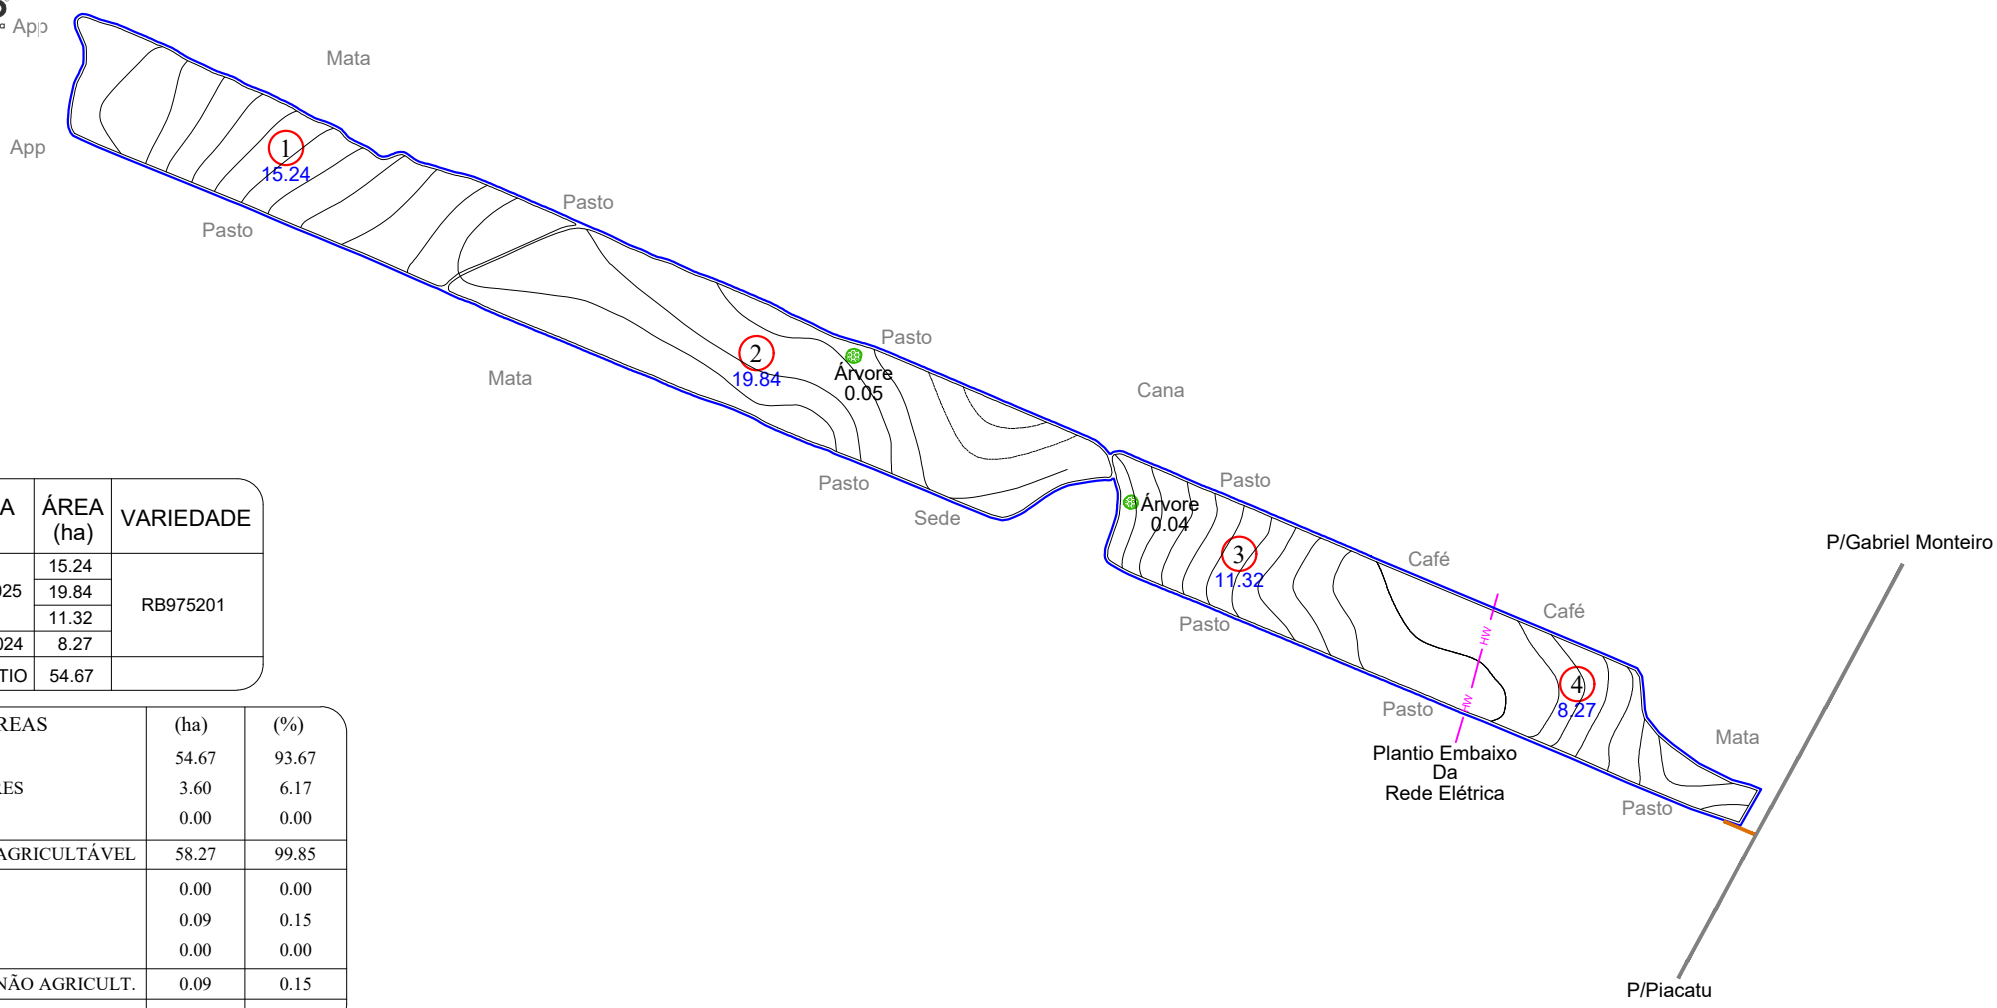


Nº TAL.	DATA PL.	ÁREA (ha)	VARIEDADE
1	05/2025	15.24	RB975201
2		19.84	
3		11.32	
4	05/2024	8.27	
TOTAL PLANTIO		54.67	

ÁREAS	(ha)	(%)
PLANTIO	54.67	93.67
CARREADORES	3.60	6.17
OUTROS	0.00	0.00
SUB TOTAL AGRICULTÁVEL	58.27	99.85
AP.P.	0.00	0.00
ÁRVORES	0.09	0.15
OUTROS	0.00	0.00
SUB TOTAL NÃO AGRICULT.	0.09	0.15
ÁREA TOTAL	58.36	100.00

C. NÍVEL: 8243.88 m/l 1.90 ha 3.25 %


ESCALA: 1: 13.500

LEGENDA

- FAZENDA
- TALHÃO
- REDE ELÉTRICA
- TERRAÇO BASE LARGA
- TERRAÇO EMBUTIDO

ESPAÇAMENTO: 1.50 x 1.50
TIRO MÉDIO ESTIMADO: 175.07 m
D.V: 4.14 %

CROQUI DE ACESSO

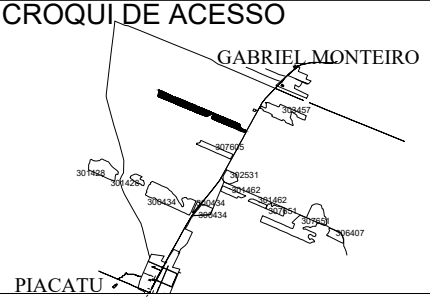

SÍTIO NOSSA SENHORA APARECIDA II

PROPRIETÁRIO: ADAUTO SPINARDI
COMPRADOR: CLEALCO
MUNICÍPIO: GABRIEL MONTEIRO - SP

DISTÂNCIAS (km):
UNID. I - Asfalto: 28.00 Terra.: 3.00
UNID.I I - Asfalto: 67.00 Terra.: 3.00

COORDENADAS: E(X): 543191.53 N(Y): 7618156.06
LAT: -21°32'19.8819" LONG: -50°34'58.4390"

CLEALCO - AÇÚCAR E ALCOOL S/A - DEPARTAMENTO DE GEOTECNOLOGIA

LEVANTAMENTO VIA:
SATÉLITE
GPS / VANT
GOOGLE

UNIDADE: I
PARTE: A/A
FUNDO AGRÍCOLA: 303394

M:\01-Mapa de safra\Mapas Atualizados\Terceiro\303394 - Sitio Nossa Senhora Aparecida I (Adauto Spinardi)\303394 - Sitio Nossa Senhora Aparecida I (Adauto Spinardi).dwg

Bruno Gamboa 02/12/25