D.V.	Nº TAL.	DATA PL.	ÁREA (ha)	VARIEDADE
3.83%	1	06/2024	34.41	RB975242
TOTAL PLANTIO			34.41	

ÁREAS	(ha)	(%)
PLANTIO	34.41	91.10
CARREADORES	3.30	8.74
OUTROS	0.04	0.11
SUB TOTAL AGRICULTÁVEL	37.75	99.95
AP.P.	0.00	0.00
ÁRVORES	0.02	0.05
OUTROS	0.00	0.00
SUB TOTAL NÃO AGRICULT.	0.02	0.05
ÁREA TOTAL	37.77	100.00

C. NÍVEL:	2883.73 m/l	0.66 ha	1.76 %

LEGENDA

- ▬ FAZENDA
- ▬ TALHÃO
- ---- REDE ELÉTRICA
- ▬ TERRAÇO BASE LARGA
- — TERRAÇO EMBUTIDO

ESPAÇAMENTO:	1.50 x 1.50
TIRO MÉDIO ESTIMADO:	144.70 m

Clealco
Açúcar, Etanol e Energia

▨ (N.P)-NÃO PLANTOU	
TALHÃO	(ha)
1	0.04
Total	0.04

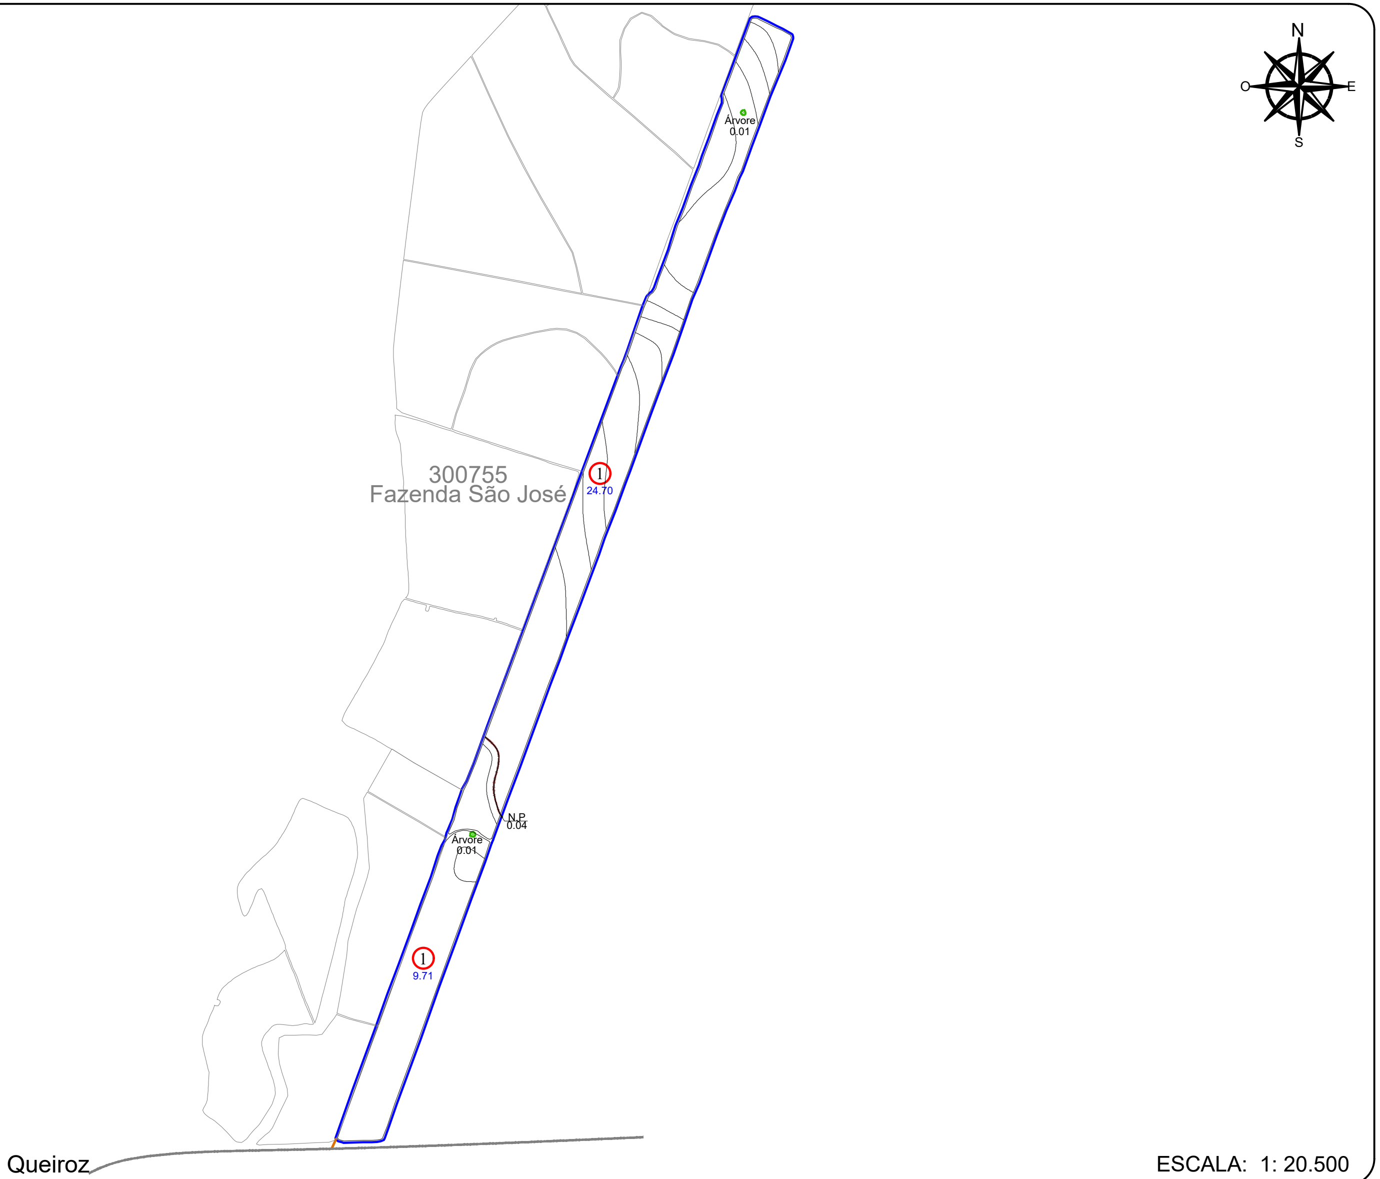

ESCALA: 1: 20.500

CROQUI DE ACESSO

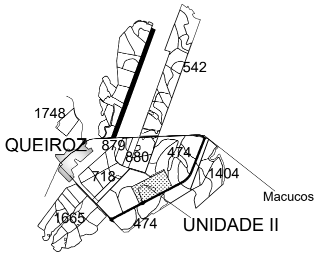

SÍTIO TANAKA

PROPRIETÁRIO:	CLAUDIO MIGUEL GRISOLIA
COMPRADOR:	CLEALCO S/A
MUNICÍPIO:	QUEIROZ- SP

DISTÂNCIAS (km):

	Asfalto:		Terra.:	
UNID. I -	Asfalto:	60.60	Terra.:	00.00
UNID.I I -	Asfalto:	6.00	Terra.:	00.00
UNID. III -	Asfalto:	48.50	Terra.:	00.00

COORDENADAS:			
E(X):	580307.97	N(Y):	7591306.57
LAT:	-21°46'48.4897"	LONG:	-50°13'23.4776"

CLEALCO - AÇÚCAR E ALCOOL S/A - DEPARTAMENTO DE GEOTECNOLOGIA

UNIDADE:
II

PARTE:
A/A

FUNDO AGRÍCOLA:
303400

M:\01-Mapa de safra\Mapas Atualizados\Terceiro\303400 - Sitio Tanaka (Claudio Miguel Grisolia)\303400 - Sitio Tanaka (Claudio Miguel Grisolia).dwg

Bruno Gamboa 04/12/24