
Clealco
Açúcar, Etanol e Energia



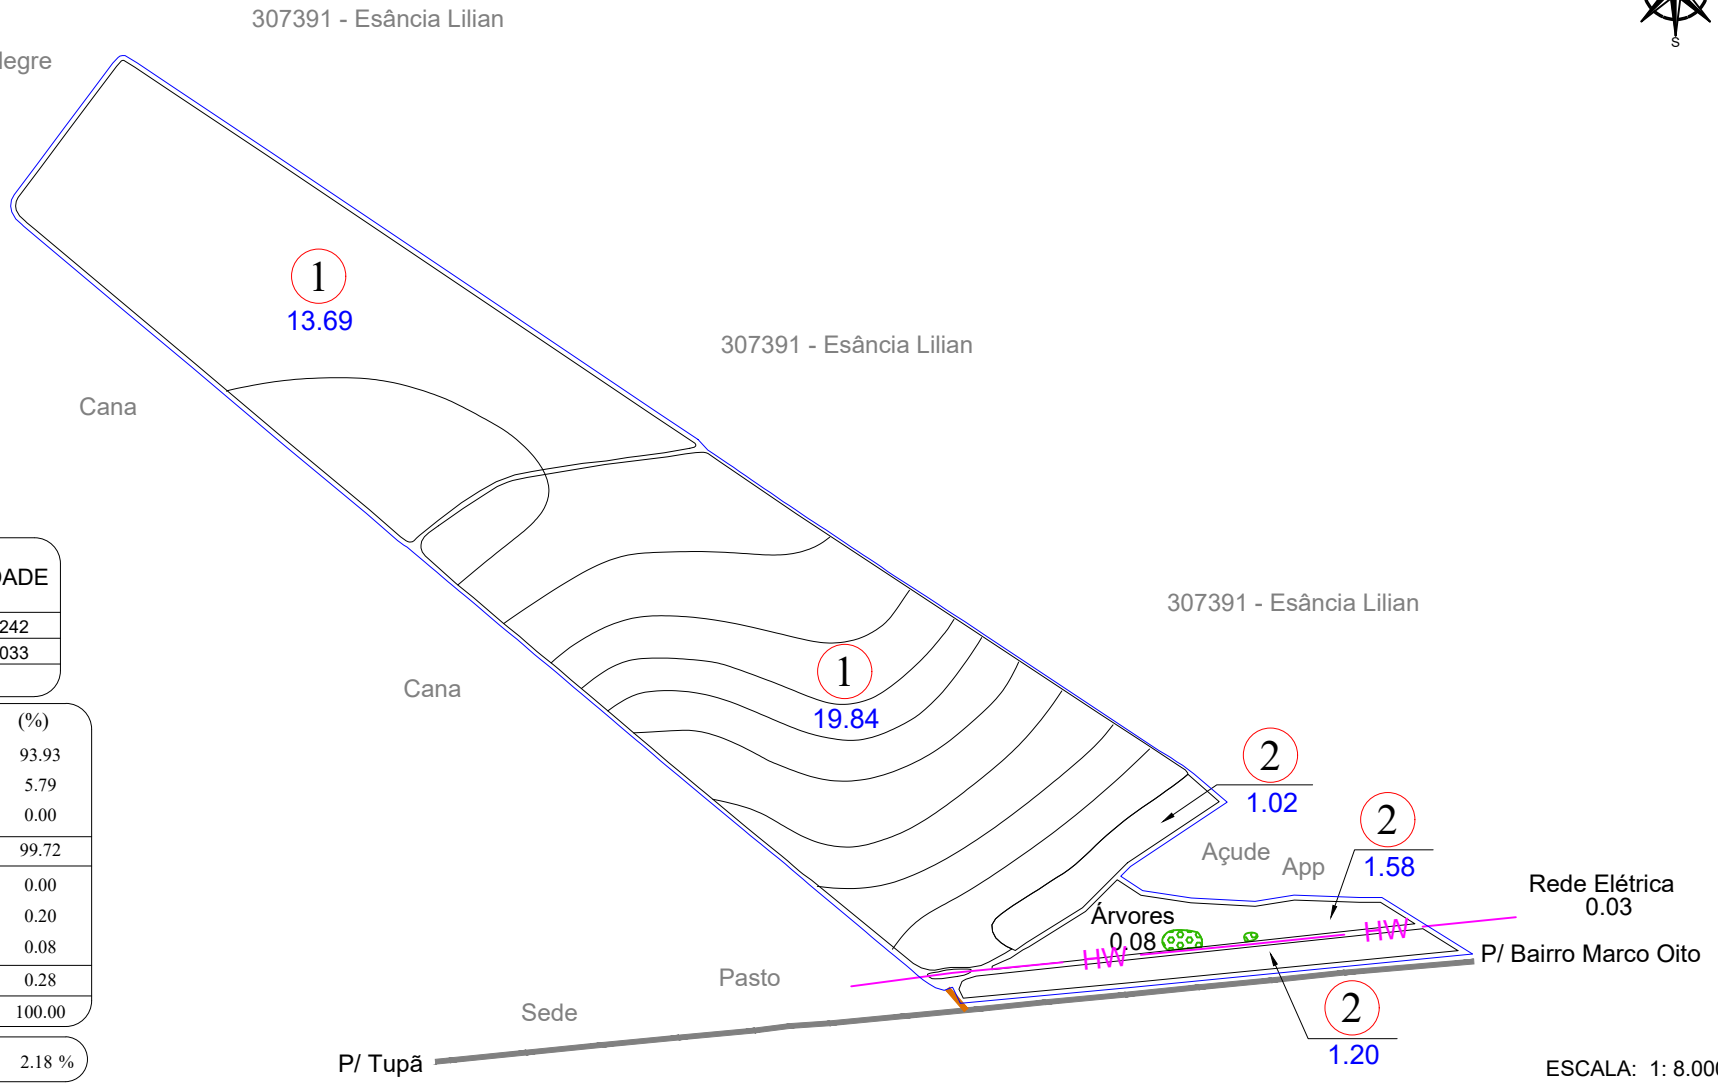

Nº TAL.	DATA PL.	ÁREA (ha)	VARIEDADE
1	2026	33.53	RB 975242
2	05/2024	3.80	RB 975033
TOTAL PLANTIO		37.33	


ÁREAS	(ha)	(%)
PLANTIO	37.33	93.93
CARREADORES	2.30	5.79
OUTROS	0.00	0.00
SUB TOTAL AGRICULTÁVEL	39.63	99.72
AP.P.	0.00	0.00
MATA	0.08	0.20
OUTROS	0.03	0.08
SUB TOTAL NÃO AGRICULT.	0.11	0.28
ÁREA TOTAL	39.74	100.00

C. NÍVEL: 3759.88 m/l 0.86 ha 2.18 %

LEGENDA
- FAZENDA
- TALHÃO
- REDE ELÉTRICA
- TERRAÇO BASE LARGA
- TERRAÇO EMBUTIDO

ESPAÇAMENTO: 1.50 x 1.50
TIRO MÉDIO ESTIMADO: 000.00 m
D.V: 4.18 %

CROQUI DE ACESSO

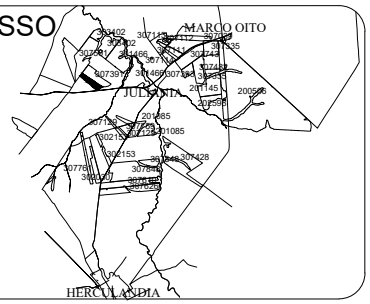

FAZENDA NOSSA SENHORA APARECIDA

PROPRIETÁRIO: REGINALDO V. RODRIGUES
COMPRADOR: CLEALCO
MUNICÍPIO: HERCULÂNDIA - SP

DISTÂNCIAS (km):
UNID. I - Asfalto: 83.80 Terra.: 0.40
UNID.I I - Asfalto: 25.00 Terra.: 1.00

COORDENADAS: E(X): 562016.88 N(Y): 7578609.48
LAT: -21°53'44.0928" LONG: -50°23'58.6646"
CLEALCO - AÇÚCAR E ALCOOL S/A - DEPARTAMENTO DE GEOTECNOLOGIA

LEVANTAMENTO VIA:
SATÉLITE
GPS / VANT
GOOGLE

UNIDADE: II
PARTE: A/A
FUNDO AGRÍCOLA: 303474

M:\01-Mapa de safra\Mapas Atualizados\Terceiro\303474 - Fazenda Nossa Senhora Aparecida (Reginaldo Viana Rodrigues)\303474 - Fazenda Nossa Senhora Aparecida (Reginaldo Viana Rodrigues).dwg

Benati 30/06/2026