
Clealco
Açúcar, Etanol e Energia

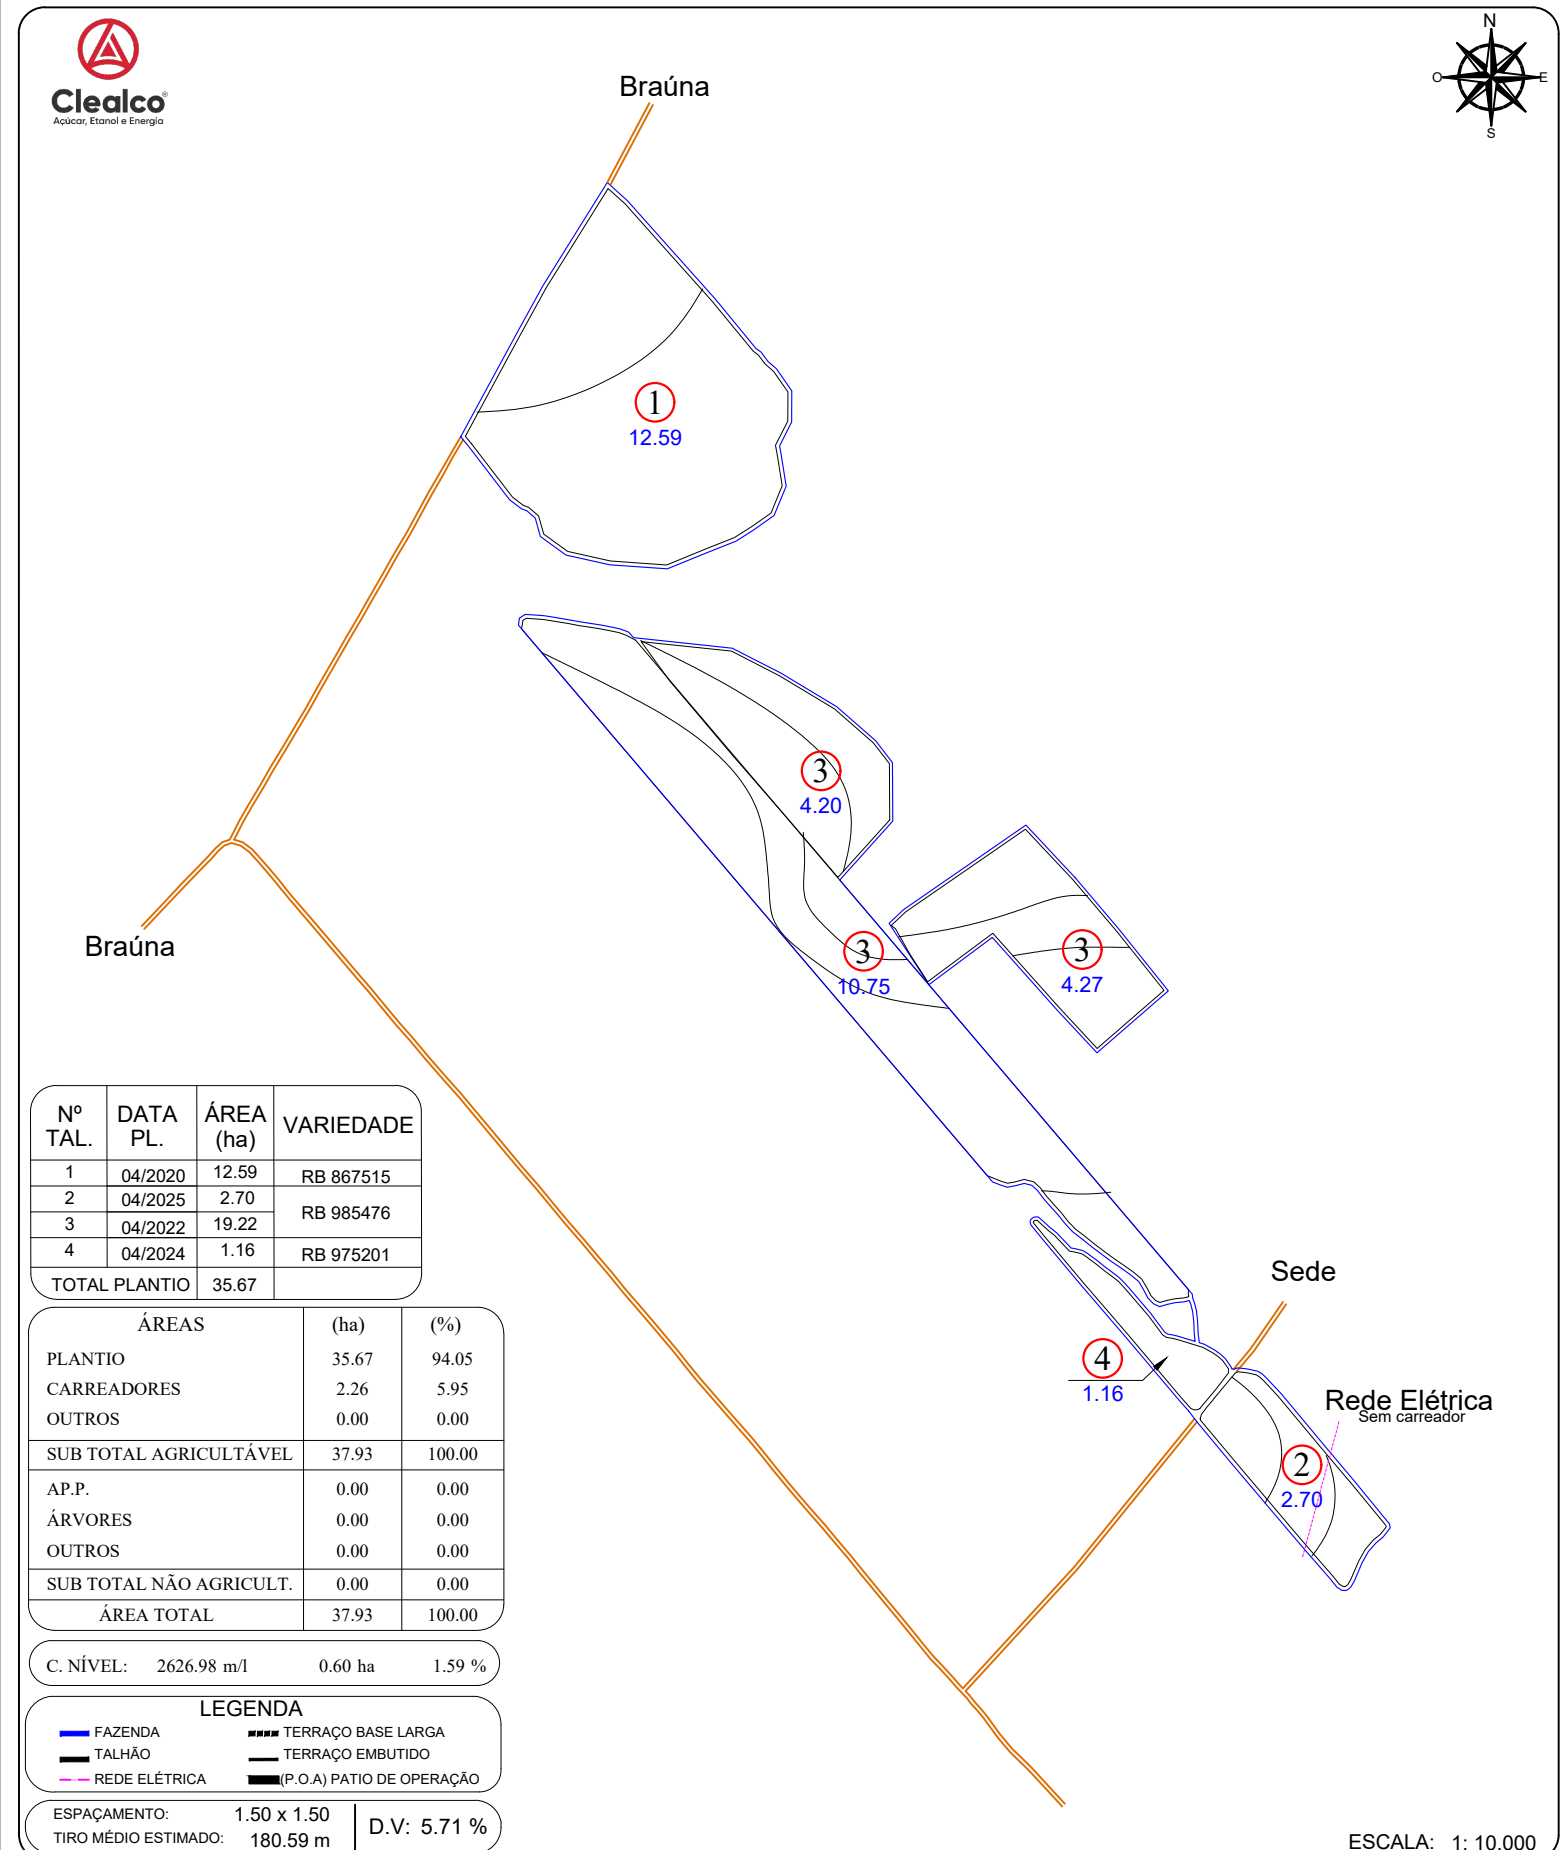

Nº TAL.	DATA PL.	ÁREA (ha)	VARIEDADE
1	04/2020	12.59	RB 867515
2	04/2025	2.70	RB 985476
3	04/2022	19.22	
4	04/2024	1.16	RB 975201
TOTAL PLANTIO		35.67	

ÁREAS	(ha)	(%)
PLANTIO	35.67	94.05
CARREADORES	2.26	5.95
OUTROS	0.00	0.00
SUB TOTAL AGRICULTÁVEL	37.93	100.00
AP.P.	0.00	0.00
ÁRVORES	0.00	0.00
OUTROS	0.00	0.00
SUB TOTAL NÃO AGRICULT.	0.00	0.00
ÁREA TOTAL	37.93	100.00

C. NÍVEL: 2626.98 m/l 0.60 ha 1.59 %


LEGENDA

- FAZENDA
- TALHÃO
- REDE ELÉTRICA
- TERRAÇO BASE LARGA
- TERRAÇO EMBUTIDO
- (P.O.A) PATIO DE OPERAÇÃO

ESPAÇAMENTO: 1.50 x 1.50
TIRO MÉDIO ESTIMADO: 180.59 m
D.V: 5.71 %

ESCALA: 1: 10.000

CROQUI DE ACESSO

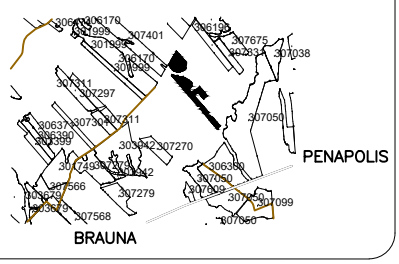

SÍTIO SÃO FRANCISCO

PROPRIETÁRIO: FERNANDO BOUGO AVELHAN
COMPRADOR: CLEALCO
MUNICÍPIO: GLICÉRIO - SP

DISTÂNCIAS (km):
UNID. I - Asfalto: 24.73 Terra.: 0.00
UNID.I I - Asfalto: 84.00 Terra.: 0.00

COORDENADAS: E(X): 576699.63 N(Y): 7625521.51
LAT: -21°28'16.2882" LONG: -50°15'34.7947"

CLEALCO - AÇÚCAR E ALCOOL S/A - DEPARTAMENTO DE GEOTECNOLOGIA

LEVANTAMENTO VIA:
- SATÉLITE
- GPS / VANT
- GOOGLE

UNIDADE: I
PARTE: A/A
FUNDO AGRÍCOLA: 303597

M:\01-Mapa de safra\Mapas Atualizados\Terceiro\303597 - Sítio São Francisco (Fernando Bougo Avelhan)\303597 - Sítio São Francisco (Fernando Bougo Avelhan).dwg

Benati 29/08/2025