
Clealco
Açúcar, Etanol e Energia

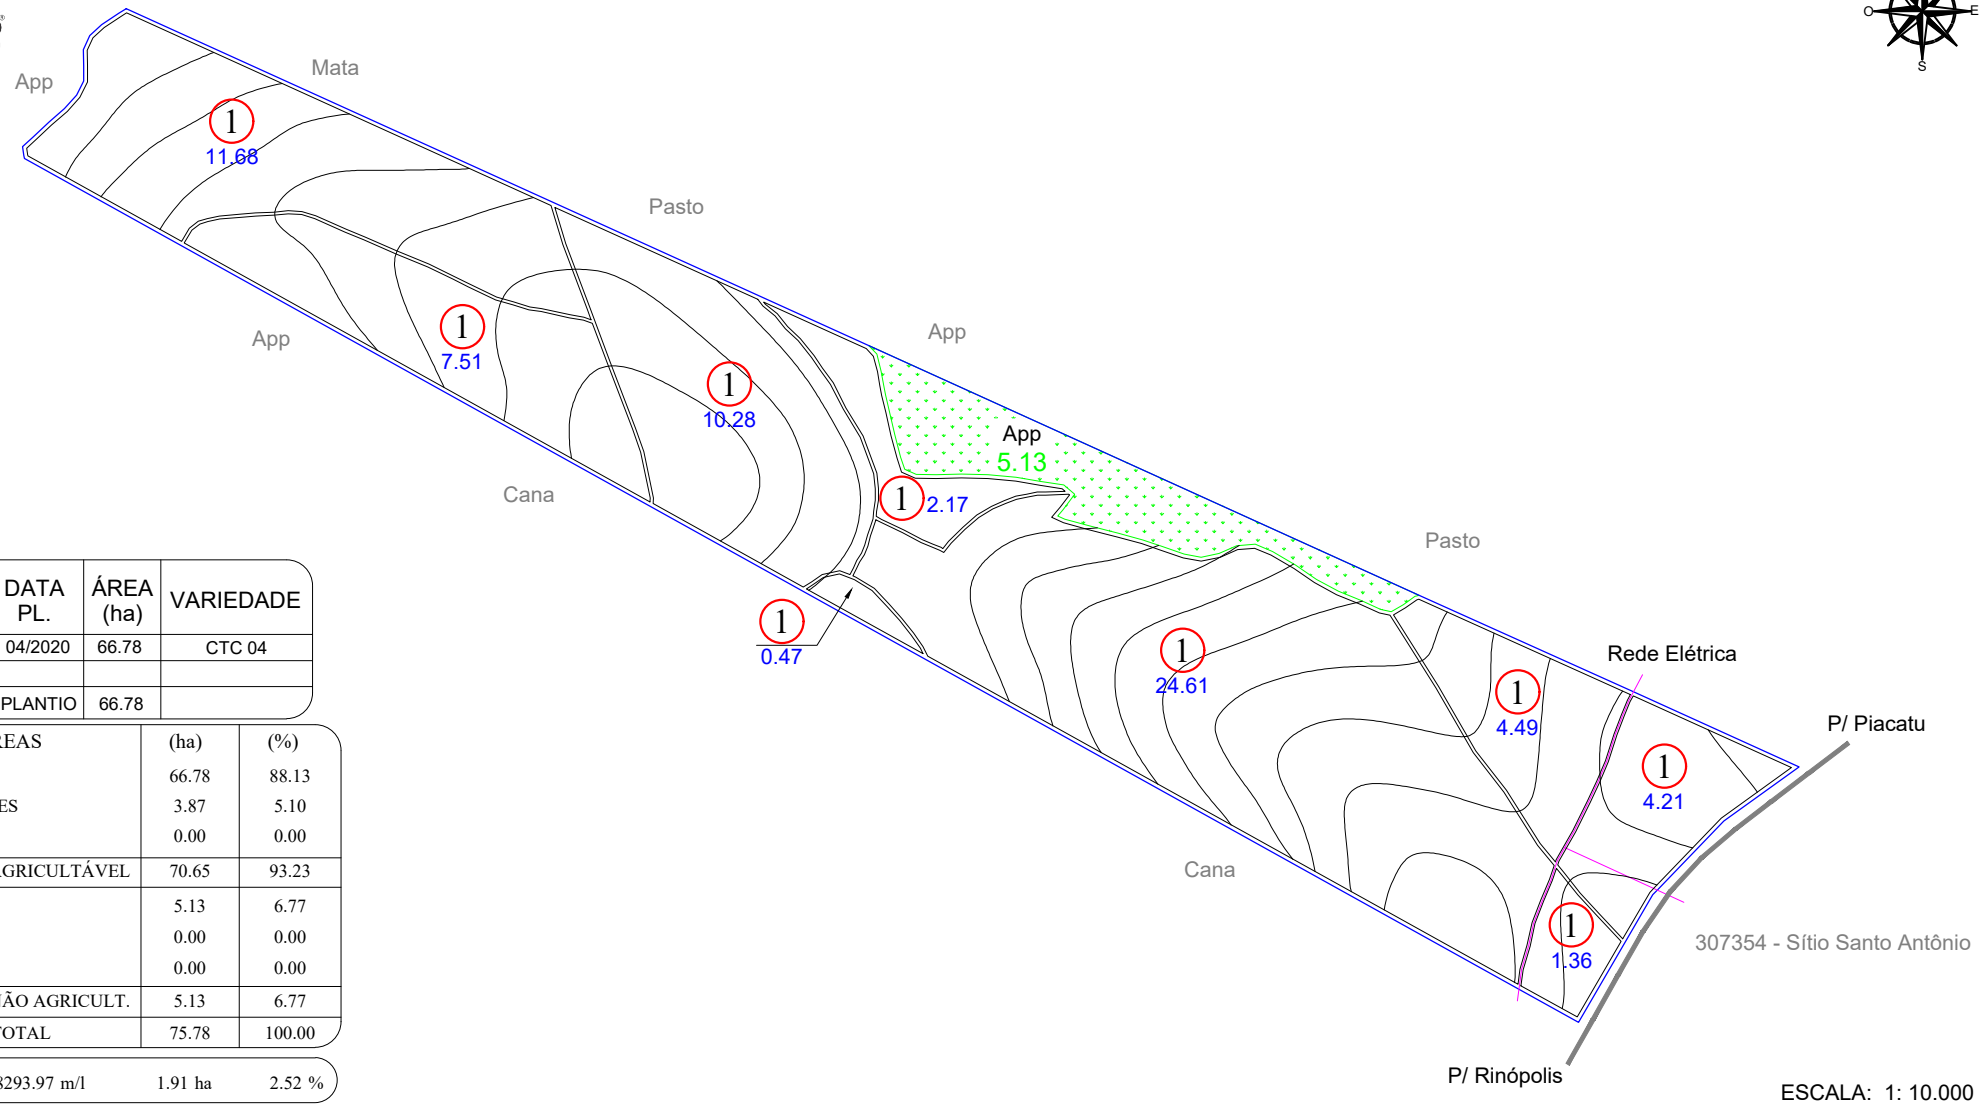


| ZONA | Nº TAL. | DATA PL. | ÁREA (ha) | VARIEDADE |
|---|---|---|---|---|
| 999 | 1 | 04/2020 | 66.78 | CTC 04 |
| | | | | |
| | TOTAL PLANTIO | | 66.78 | |

| ÁREAS | (ha) | (%) |
|---|---|---|
| PLANTIO | 66.78 | 88.13 |
| CARREADORES | 3.87 | 5.10 |
| OUTROS | 0.00 | 0.00 |
| SUB TOTAL AGRICULTÁVEL | 70.65 | 93.23 |
| AP.P. | 5.13 | 6.77 |
| ÁRVORES | 0.00 | 0.00 |
| OUTROS | 0.00 | 0.00 |
| SUB TOTAL NÃO AGRICULT. | 5.13 | 6.77 |
| ÁREA TOTAL | 75.78 | 100.00 |

| C. NÍVEL: | 8293.97 m/l | 1.91 ha | 2.52 % |
|---|---|---|---|


ESCALA: 1: 10.000

LEGENDA

- FAZENDA
- TALHÃO
- REDE ELÉTRICA
- TERRAÇO BASE LARGA
- TERRAÇO EMBUTIDO
- VAZIO
- CARREGADO

ESPAÇAMENTO: 1.50 x 1.50
TIRO MÉDIO ESTIMADO: 000.00 m
D.V: 0.00 %

CROQUI DE ACESSO

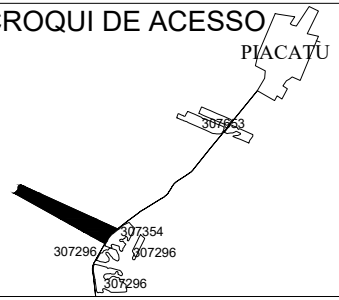


# SÍTIO BELA VISTA

PROPRIETÁRIO: JOSE ANTONIO ALVES
COMPRADOR: CLEALCO
MUNICÍPIO: PIACATU - SP

DISTÂNCIAS (km):
UNID. I - Asfalto: 24.20 Terra.: 4.00
UNID.I I - Asfalto: 62.00 Terra.: 2.00

COORDENADAS: E(X): 536852.89 N(Y): 7608844.08
LAT: -21°37'23.2692" LONG: -50°38'38.0592"
CLEALCO - AÇÚCAR E ALCOOL S/A - DEPARTAMENTO DE GEOTECNOLOGIA

LEVANTAMENTO VIA:
SATÉLITE
GPS / VANT
GOOGLE

UNIDADE: I
PARTE: A/A
FUNDO AGRÍCOLA: 303604

Bruno Gamboa 14/07/26

M:\01-Mapa de safra\Mapas Atualizados\Terceiro\303604 - Sitio Bela Vista (José Antonio Alves)\303604 - Sitio Bela Vista (José Antonio Alves).dwg