
Clealco
Açúcar, Etanol e Energia

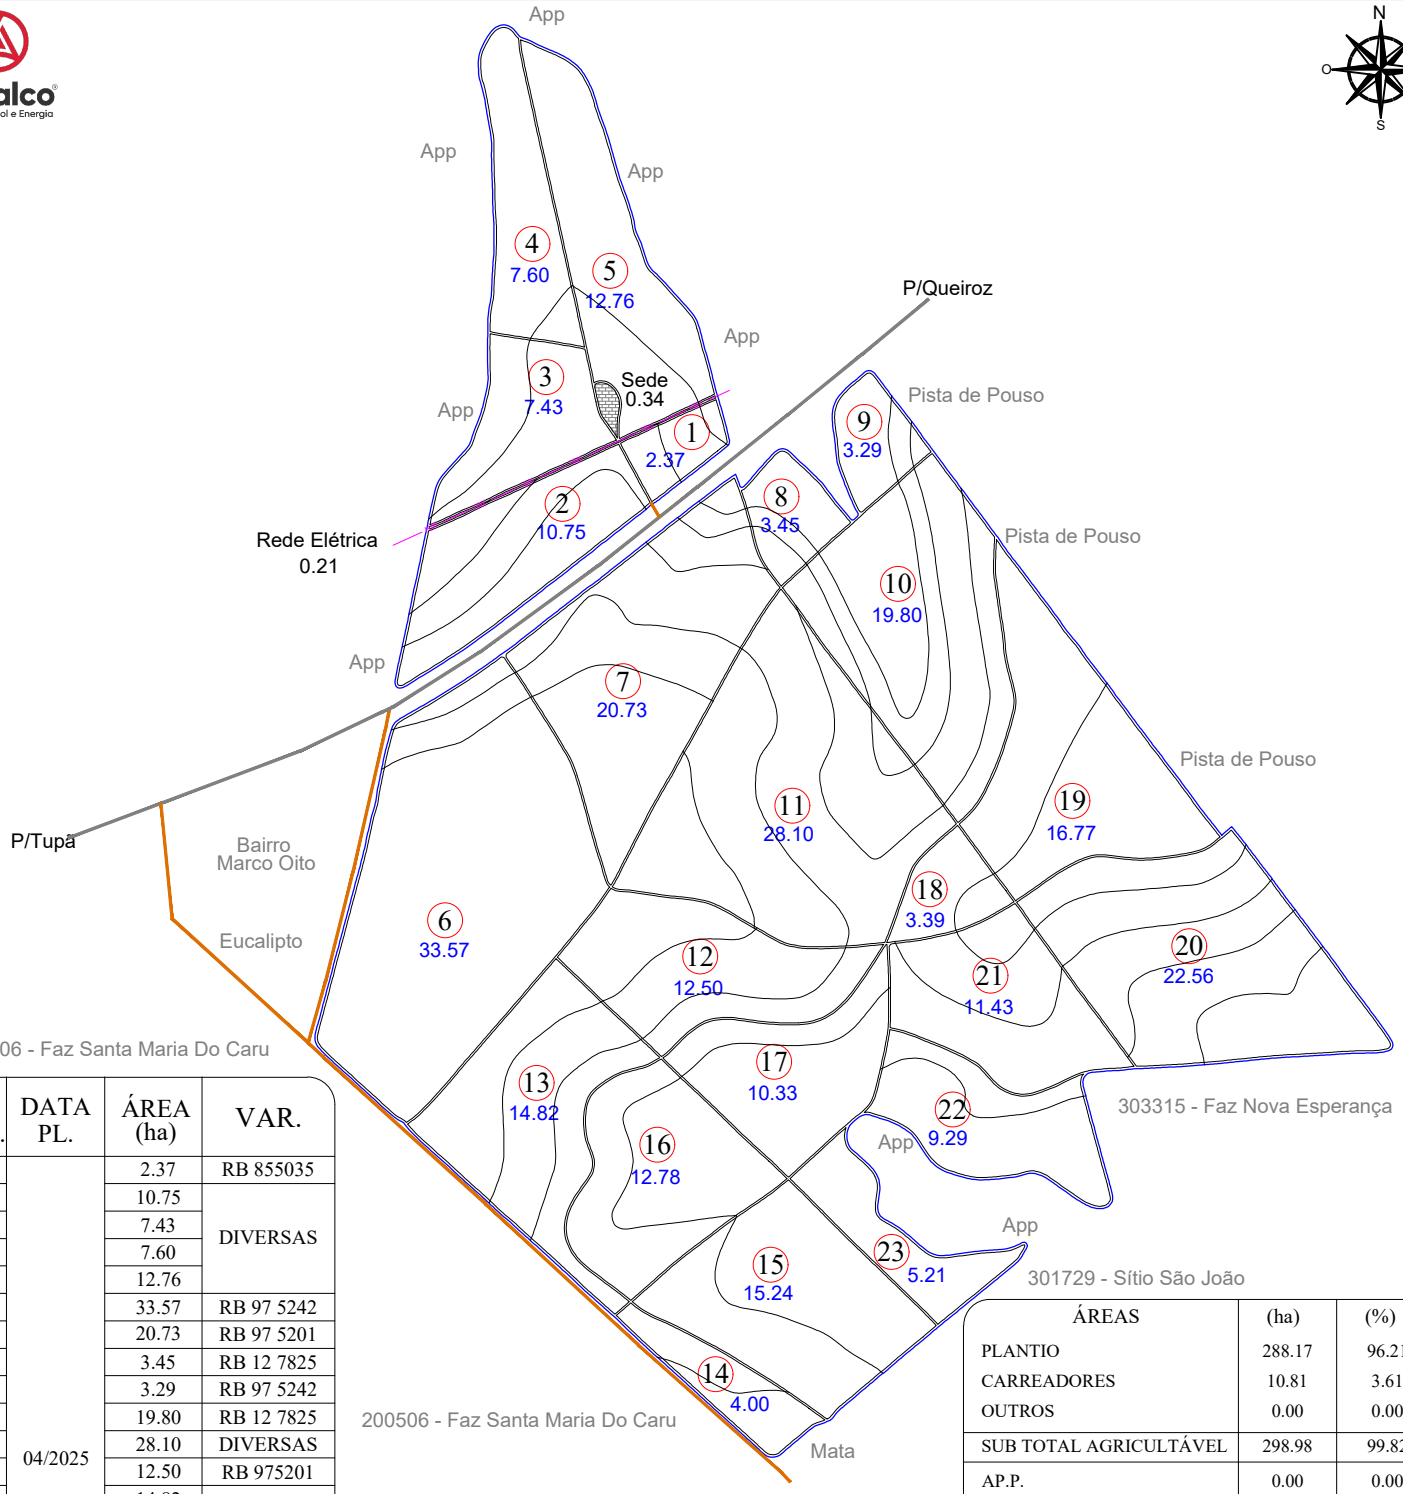

Nº TAL.	DATA PL.	ÁREA (ha)	VAR.
1	04/2025	2.37	RB 855035
2		10.75	DIVERSAS
3		7.43	
4		7.60	
5		12.76	
6		33.57	RB 97 5242
7		20.73	RB 97 5201
8		3.45	RB 12 7825
9		3.29	RB 97 5242
10		19.80	RB 12 7825
11		28.10	DIVERSAS
12		12.50	RB 975201
13		14.82	RB 07 5322
14		4.00	
15		15.24	RB 97 5242
16		12.78	RB 07 5322
17		10.33	RB 97 5242
18		3.39	RB 12 7825
19		16.77	RB 07 5322
20		22.56	CV 7870
21		11.43	
22		9.29	RB 97 5242
23		5.21	
TOTAL PLANTIO		288.17	--------

ESCALA: 1: 16.000

ÁREAS	(ha)	(%)
PLANTIO	288.17	96.21
CARREADORES	10.81	3.61
OUTROS	0.00	0.00
SUB TOTAL AGRICULTÁVEL	298.98	99.82
AP.P.	0.00	0.00
ÁRVORES	0.00	0.00
OUTROS	0.55	0.18
SUB TOTAL NÃO AGRICULT.	0.55	0.18
ÁREA TOTAL	299.53	100.00


C. NÍVEL: 17443.13 m/l 4.01 ha 1.34 %

LEGENDA

- FAZENDA
- TALHÃO
- REDE ELÉTRICA
- VAZIO
- TERRAÇO BASE LARGA
- TERRAÇO EMBUTIDO
- (P.O.A) PATIO DE OPERAÇÃO
- CARREGADO

ESPAÇAMENTO: 1.50 x 1.50
TIRO MÉDIO ESTIMADO: 000.00 m
D.V: 5.12 %

CROQUI DE ACESSO

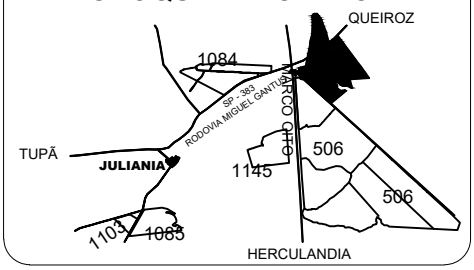

FAZENDA CHAPADÃO

PROPRIETÁRIO: FELIPE FERRAZ
COMPRADOR: CLEALCO
MUNICÍPIO: QUEIROZ - SP

DISTÂNCIAS (km):
UNID. I - Asfalto: 67.60 Terra.: 1.00
UNID.I I - Asfalto: 16.00 Terra.: 1.00

COORDENADAS: E(X): 570382.70 N(Y): 7582066.81
LAT: -21°51'50.5163" LONG: -50°19'7.6581"

CLEALCO - AÇÚCAR E ALCOOL S/A - DEPARTAMENTO DE GEOTECNOLOGIA

LEVANTAMENTO VIA:
SATÉLITE
GPS / VANT
GOOGLE

UNIDADE: II
PARTE: A/A
FUNDO AGRÍCOLA: 303621

M:\01-Mapa de safra\Mapas Atualizados\Terceiro\303621 - Fazenda Chapadão (Felipe Ferraz)\303621 - Fazenda Chapadão (Felipe Ferraz).dwg

Bruno Gamboa 24/03/26