ZONA D.V.	Nº TAL.	DATA PL.	ÁREA (ha)	VARIEDADE
999 5.39 %	1	05/2023	12.53	RB 975201
	2		7.49	
	3		10.71	
	4		8.91	
TOTAL PLANTIO			39.64	--------


ÁREAS	(ha)	(%)
PLANTIO	39.64	93.42
CARREADORES	2.76	6.51
OUTROS	0.00	0.00
SUB TOTAL AGRICULTÁVEL	42.40	99.93
AP.P.	0.00	0.00
ÁRVORES	0.03	0.07
OUTROS	0.00	0.00
SUB TOTAL NÃO AGRICULT.	0.03	0.07
ÁREA TOTAL	42.43	100.00

C. NÍVEL: 4264.78 m/l 0.98 ha 2.31 %

LEGENDA


- FAZENDA
- TALHÃO
- CURVA DE NÍVEL
- CARREADOR
- CONFRONTANTE
- REDE ELÉTRICA
- TRAJETO VAZIO
- TRAJETO CARREGADO

PLANTIO MANUAL - ESPAÇAMENTO: 1.50 X 1.50

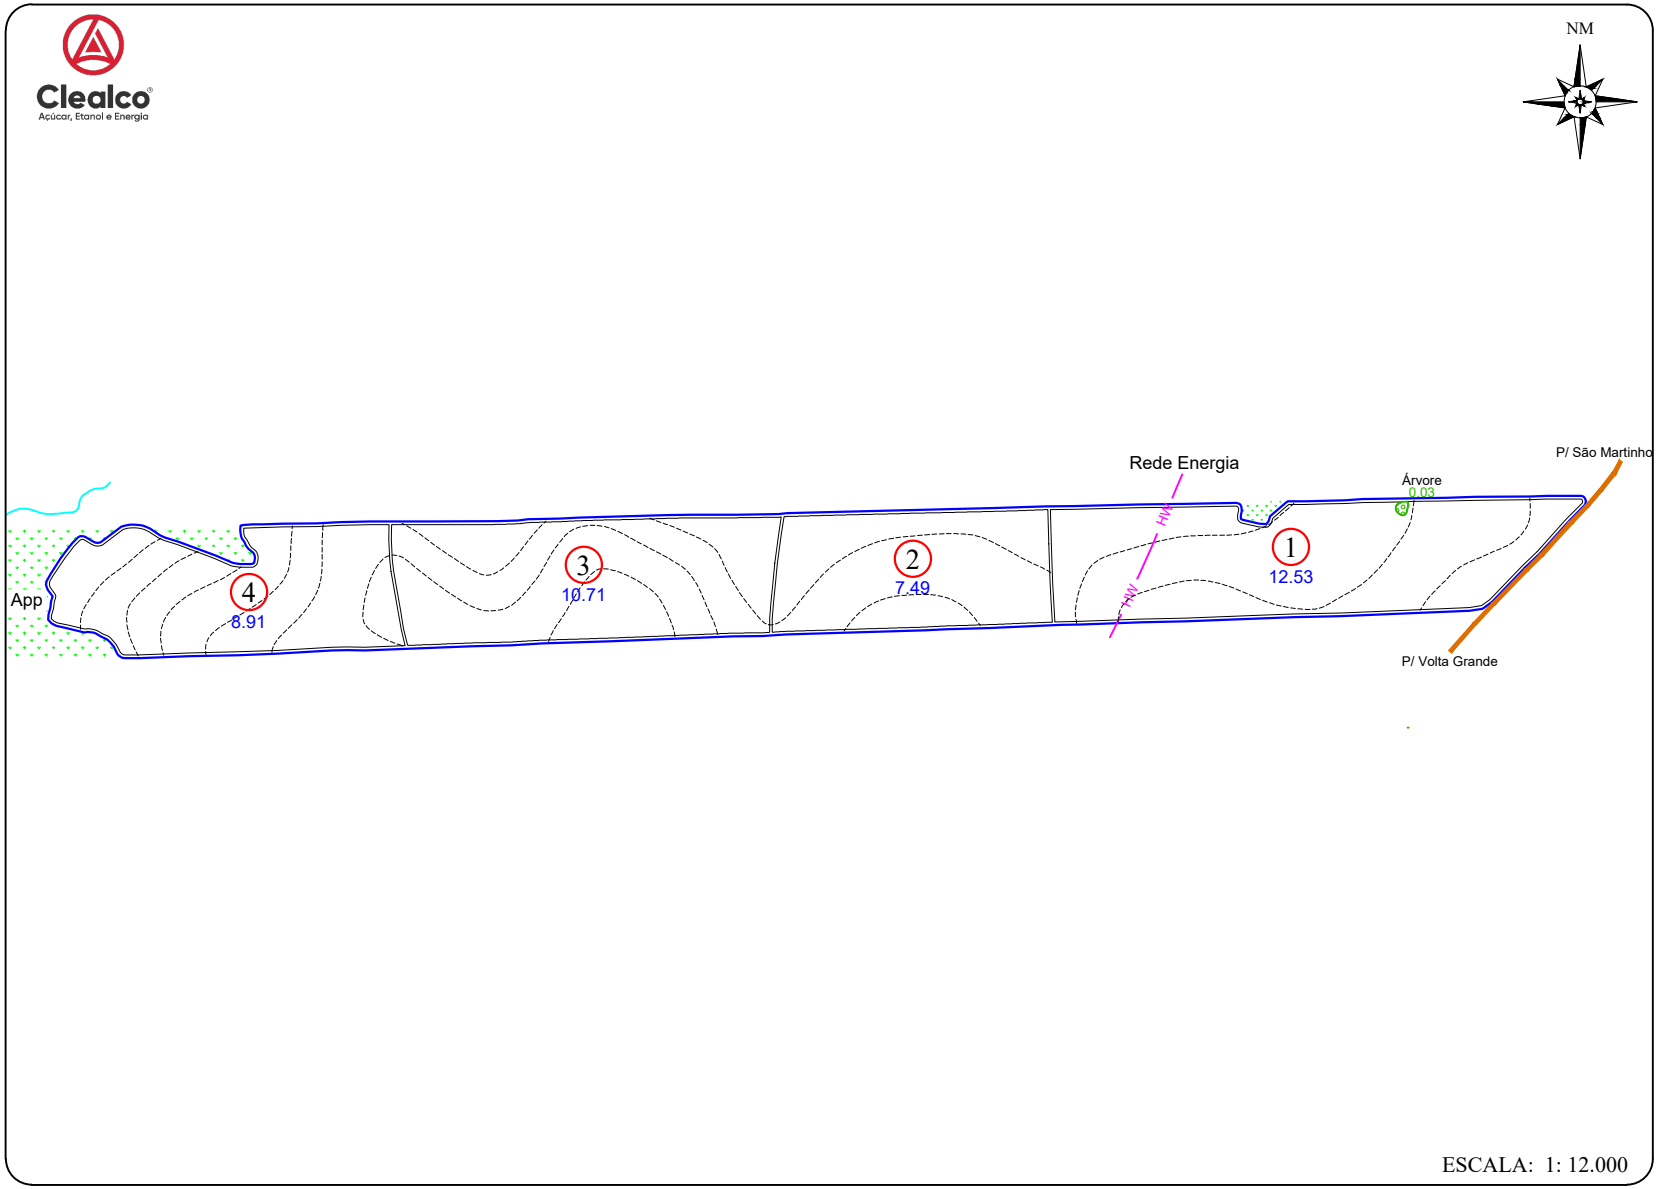

ESCALA: 1: 12.000

CROQUI DE ACESSO

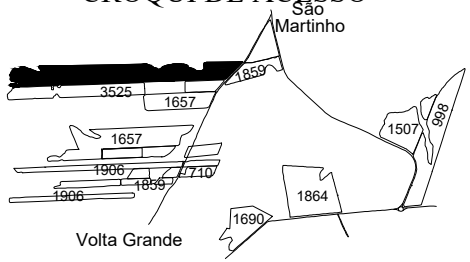

SÍTIO SÃO MARTINHO

PROPRIETÁRIO: GENILSON A. DOS SANTOS
COMPRADOR: CLEALCO S/A
MUNICÍPIO: ALTO ALEGRE

DISTÂNCIAS (km):

UNID. I - Asfalto:	43.00	Terra.:	5.00
UNID.I I - Asfalto:	38.00	Terra.:	0.90
UNID. III -Asfalto:	31.30	Terra.:	1.00

COORDENADAS: E(X): 573747.99 N(Y): 7612625.93
LAT: -21°35'16.1461" LONG: -50°17'15.3089"

CLEALCO - AÇÚCAR E ALCOOL S/A - DEPARTAMENTO DE TOPOGRAFIA

UNIDADE: I

PARTE: A/A

FUNDO AGRÍCOLA: 303657