ZONA D.V.	Nº TAL.	DATA PL.	ÁREA (ha)	VAR.
999	1	04/2022	12.16	CTC 04
	2		10.89	
	3		23.75	
	4		18.49	
	5		24.02	
TOTAL PLANTIO			89.31	--------


ÁREAS	(ha)	(%)
PLANTIO	89.31	96.25
CARREADORES	3.46	3.73
OUTROS	0.00	0.00
SUB TOTAL AGRICULTÁVEL	92.77	99.98
AP.P.	0.00	0.00
ÁRVORES	0.02	0.02
OUTROS	0.00	0.00
SUB TOTAL NÃO AGRICULT.	0.02	0.02
ÁREA TOTAL	92.79	100.00

C. NÍVEL: 12925.41 m/l 2.97 ha 3.20 %


LEGENDA

- FAZENDA
- TALHÃO
- CURVA DE NÍVEL
- CARREADOR
- CONFRONTANTE
- REDE ELÉTRICA
- TRAJETO VAZIO
- TRAJETO CARREGADO

PLANTIO MANUAL - ESPAÇAMENTO: 1.50 X 1.50

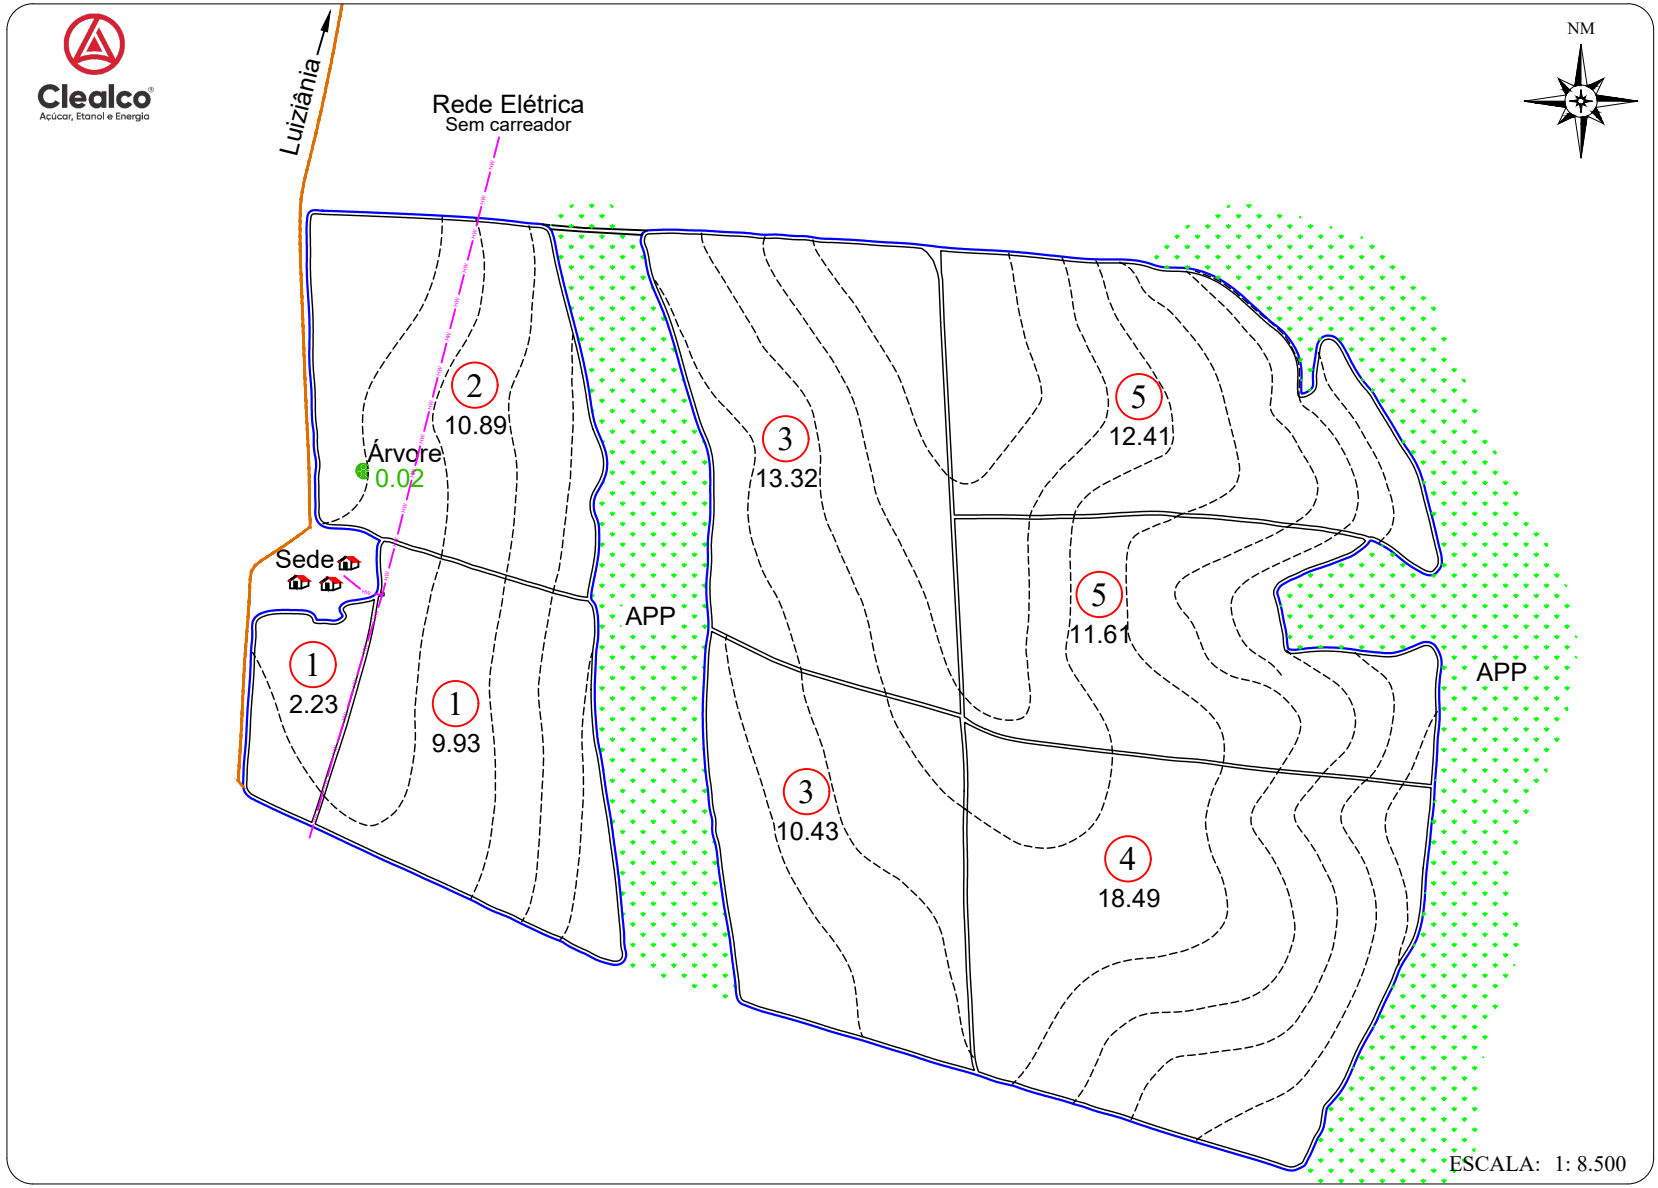

CROQUI DE ACESSO

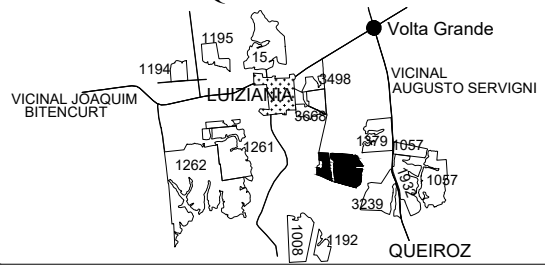

FAZENDA SANTA LÚCIA

PROPRIETÁRIO: CLÉZIO HUNGARO
COMPRADOR: CLEALCO S/A
MUNICÍPIO: LUIZIÂNIA

DISTÂNCIAS (km):
UNID. I - Asfalto: 29.00 Terra.: 3.10
UNID.I I - Asfalto: 26.00 Terra.: 2.60
UNID. III -Asfalto: 40.00 Terra.: 00.00

COORDENADAS: E(X): 571414 N(Y): 7600434
LAT: 21° 41' 53,01201" LONG: 50° 18' 34,58806"

CLEALCO - AÇÚCAR E ALCOOL S/A - DEPARTAMENTO DE TOPOGRAFIA

UNIDADE: I
PARTE: A/A
FUNDO AGRÍCOLA: 303667

M:\01-Mapa de safra\Mapas Atualizados\Terceiro\303667 - Fazenda Santa Lúcia (Clezio Hungaro)\303667 - Fazenda Santa Lúcia (Clezio Hungaro).dwg

Bruno Gamboa 22/11/2022