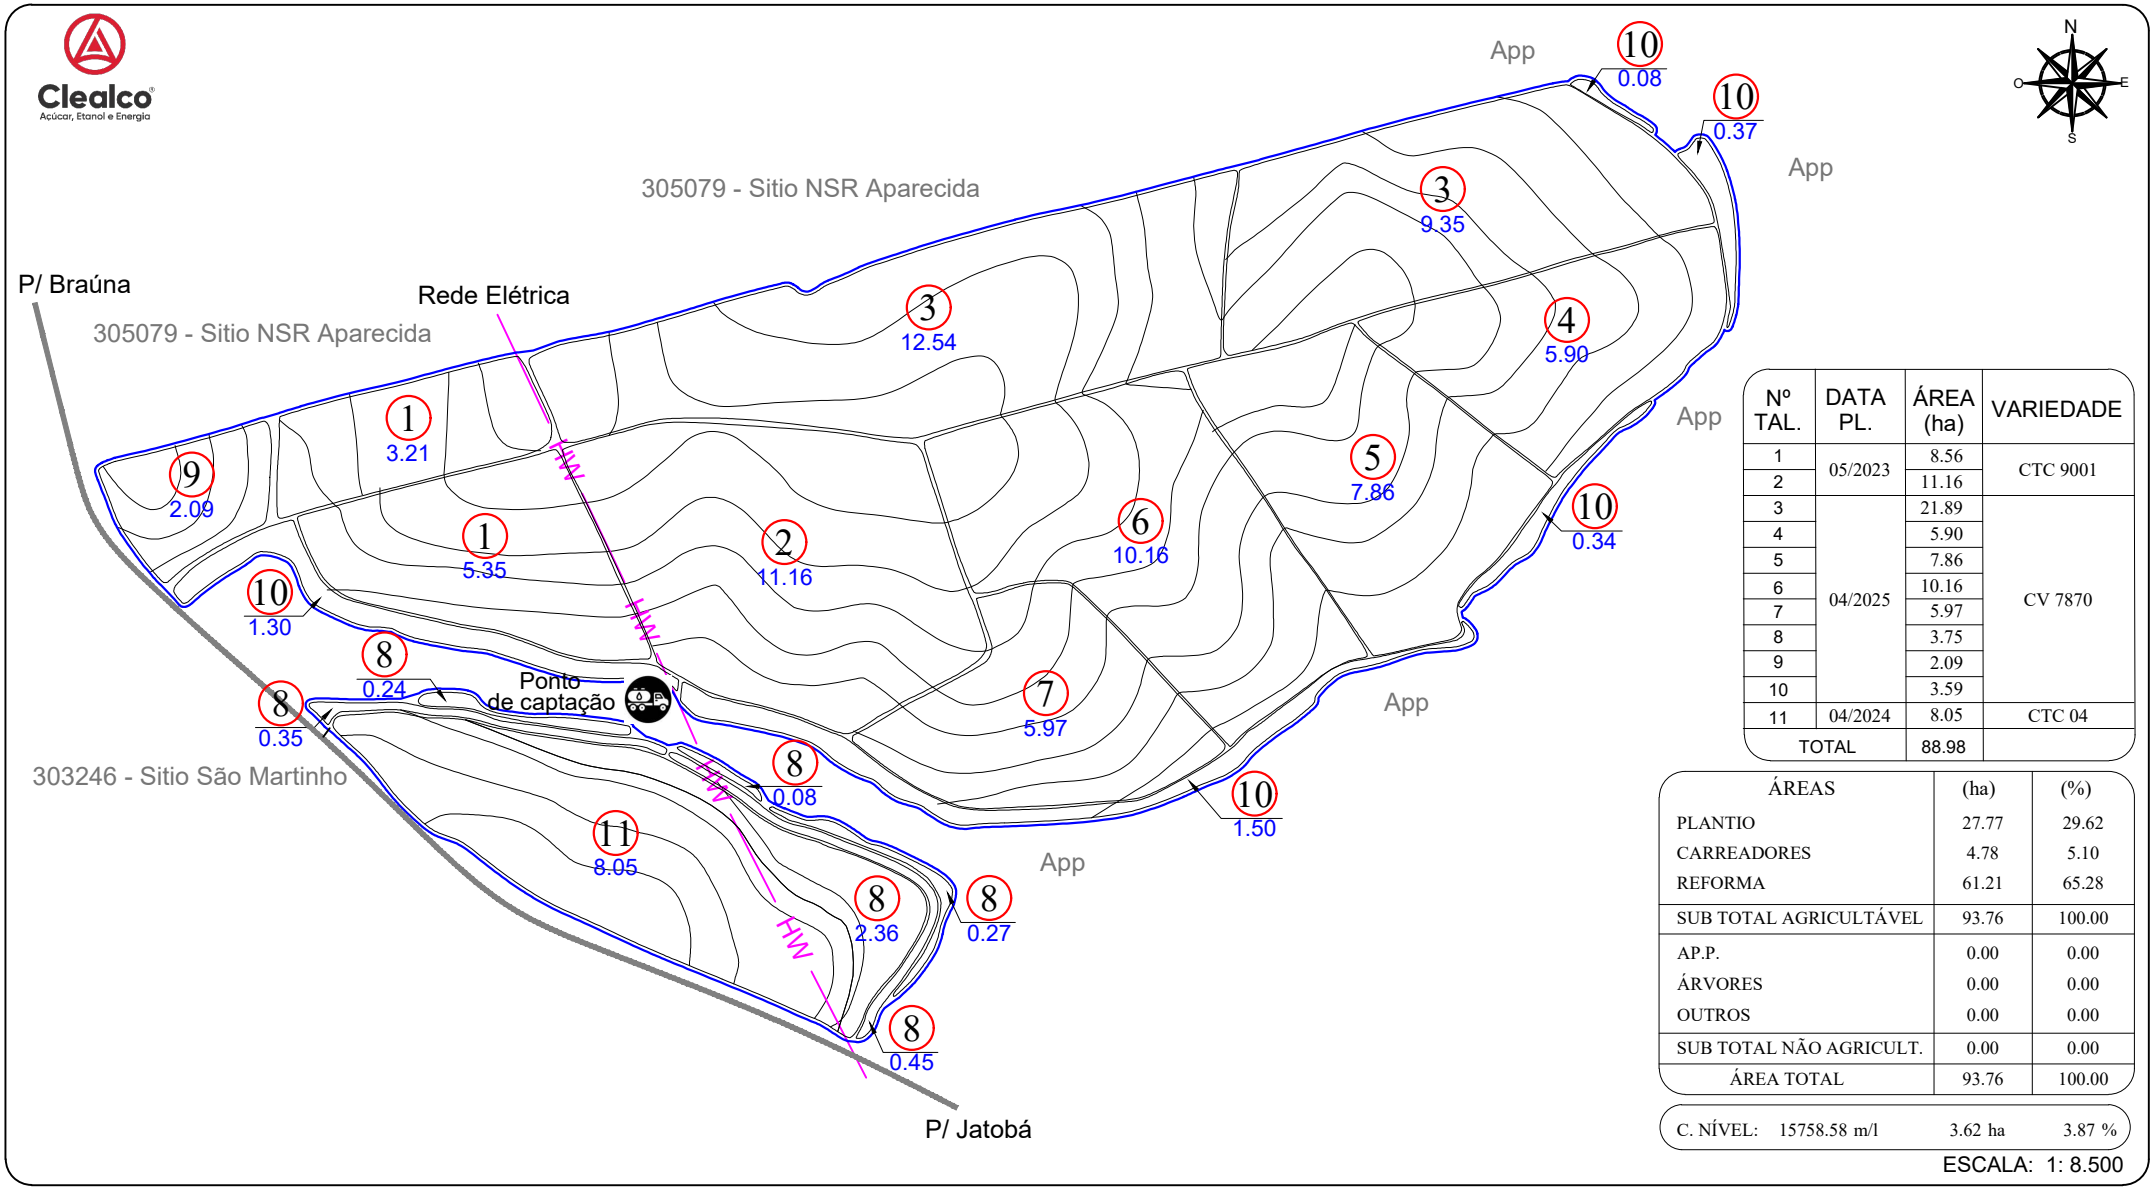


Nº TAL.	DATA PL.	ÁREA (ha)	VARIEDADE
1	05/2023	8.56	CTC 9001
2		11.16	
3	04/2025	21.89	CV 7870
4		5.90	
5		7.86	
6		10.16	
7		5.97	
8		3.75	
9		2.09	
10		3.59	
11	04/2024	8.05	CTC 04
TOTAL		88.98	

ÁREAS	(ha)	(%)
PLANTIO	27.77	29.62
CARREADORES	4.78	5.10
REFORMA	61.21	65.28
SUB TOTAL AGRICULTÁVEL	93.76	100.00
AP.P.	0.00	0.00
ÁRVORES	0.00	0.00
OUTROS	0.00	0.00
SUB TOTAL NÃO AGRICULT.	0.00	0.00
ÁREA TOTAL	93.76	100.00

C. NÍVEL: 15758.58 m/l 3.62 ha 3.87 %


ESCALA: 1: 8.500

LEGENDA

- FAZENDA
- TALHÃO
- REDE ELÉTRICA
- TERRAÇO BASE LARGA
- TERRAÇO EMBUTIDO

ESPAÇAMENTO: 1.50 x 1.50
TIRO MÉDIO ESTIMADO: 000.00 m
D.V: 6.50 %

CROQUI DE ACESSO

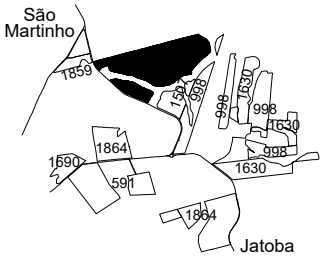

ESTÂNCIA PRINCESA

PROPRIETÁRIO: WILLIAN ÁVILA PEREIRA
COMPRADOR: CLEALCO
MUNICÍPIO: ALTO ALEGRE - SP

DISTÂNCIAS (km):
UNID. I - Asfalto: 25.90 Terra.: 14.30
UNID.I I - Asfalto: 38.50 Terra.: 0.00

COORDENADAS: E(X): 576126.80 N(Y): 7612241.46
LAT: -21°35'28.2909" LONG: -50°15'52.5246"

CLEALCO - AÇÚCAR E ALCOOL S/A - DEPARTAMENTO DE GEOTECNOLOGIA

LEVANTAMENTO VIA:
SATÉLITE
GPS / VANT
GOOGLE

UNIDADE: I
PARTE: A/A
FUNDO AGRÍCOLA: 303675

M:\01-Mapa de safra\Mapas Atualizados\Terceiro\303675 - Estância Princesa (Willian Ávila Pereira)\303675 - Estância Princesa (Willian Ávila Pereira).dwg

Bruno Gamboa 23/07/25