ZONA D.V.	Nº TAL.	DATA PL.	ÁREA (ha)	VARIEDADE
999 4.58%	1	07/2021	23.24	CTC 04
	2	05/2023	11.24	RB 975242
	3		16.10	
	4	04/2022	10.24	
TOTAL PLANTIO			60.82	--------


ÁREAS	(ha)	(%)
PLANTIO	60.82	93.03
CARREADORES	3.13	4.78
OUTROS	0.00	0.00
SUB TOTAL AGRICULTÁVEL	63.95	97.81
AP.P.	0.00	0.00
ÁRVORES	1.43	2.19
OUTROS	0.00	0.00
SUB TOTAL NÃO AGRICULT.	1.43	2.19
ÁREA TOTAL	65.38	100.00

C. NÍVEL: 9342.46 m/l 2.15 ha 3.29 %


LEGENDA

- FAZENDA
- TALHÃO
- CURVA DE NÍVEL
- CARREADOR
- CONFRONTANTE
- REDE ELÉTRICA
- TRAJETO VAZIO
- TRAJETO CARREGADO

PLANTIO MANUAL - ESPAÇAMENTO: 1.50 X 1.50
TIRO MÉDIO ESTIMADO: 000.00 m

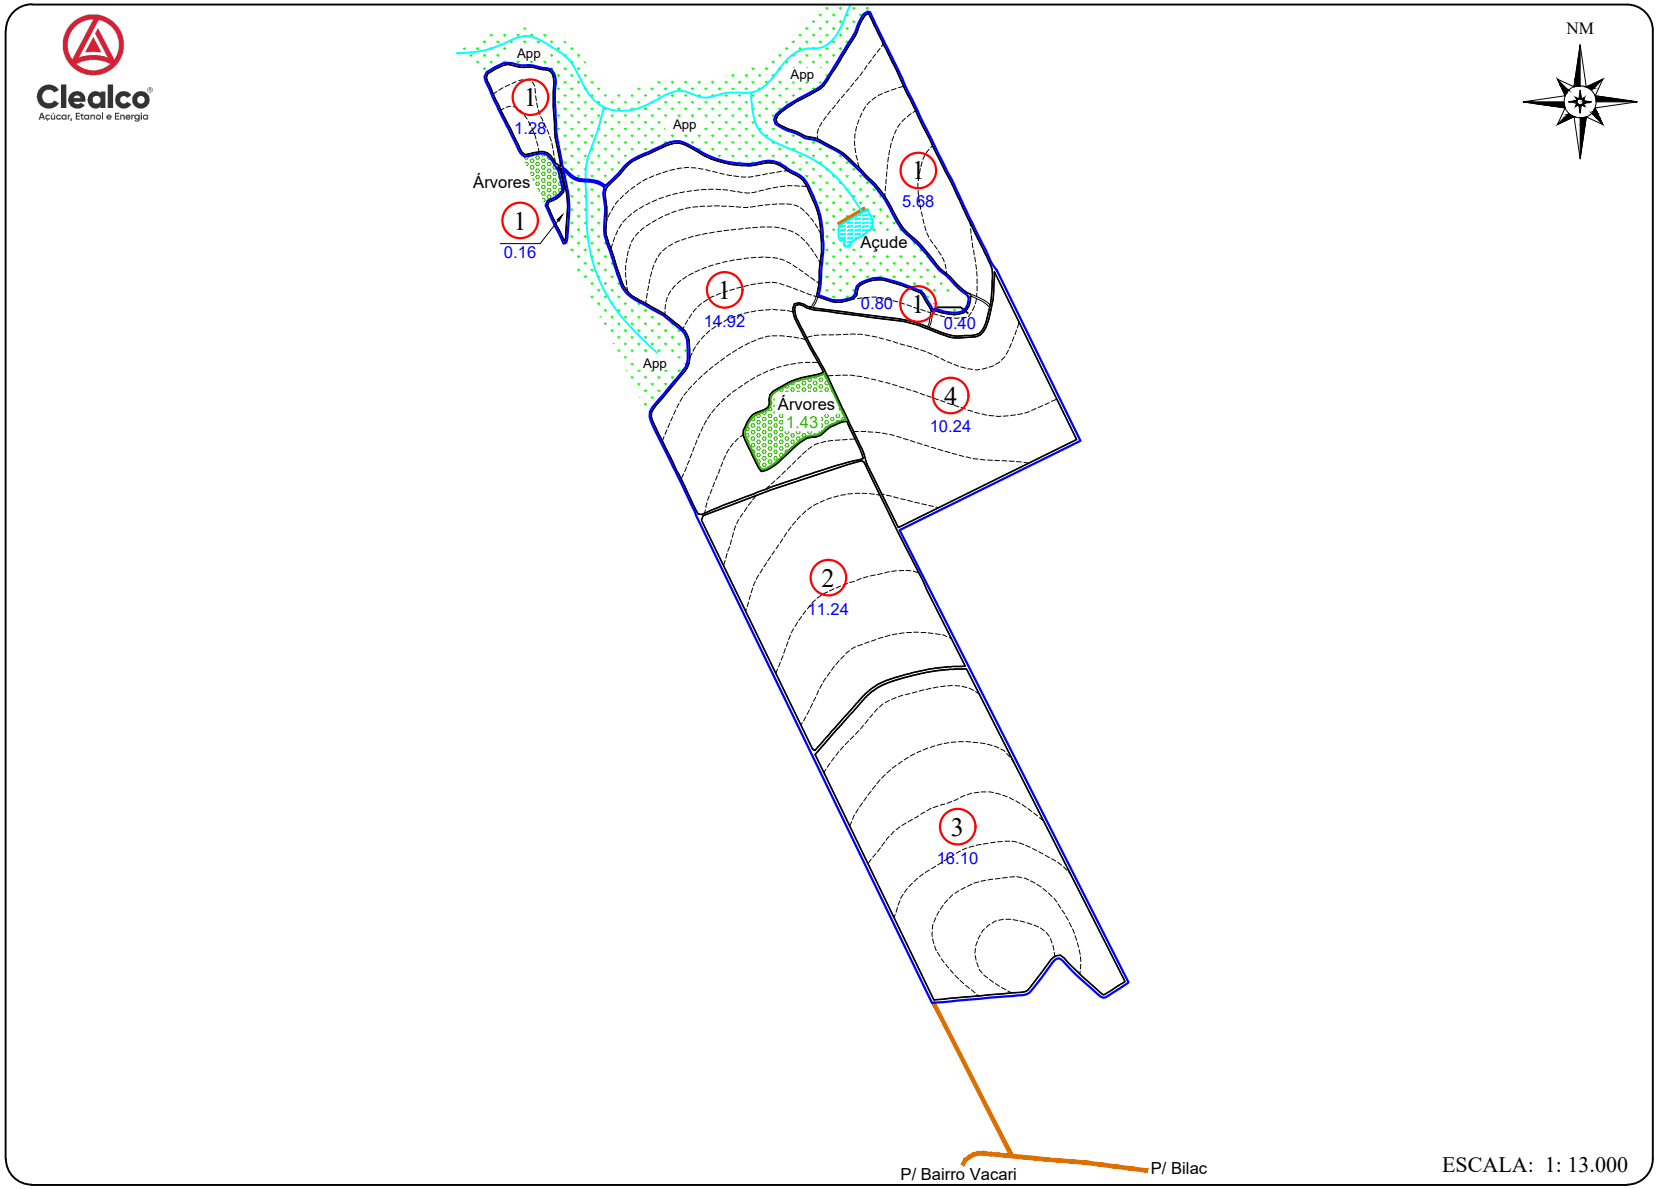

CROQUI DE ACESSO

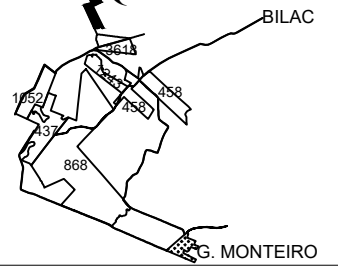

SÍTIO BELA VISTA

PROPRIETÁRIO: JAUDIR ROSSETTO
COMPRADOR: CLEALCO S/A
MUNICÍPIO: GABRIEL MONTEIRO

DISTÂNCIAS (km):
UNID. I - Asfalto: 34.00 Terra.: 9.50
UNID.I I - Asfalto: 57.00 Terra.: 18.00
UNID. III -Asfalto: 60.50 Terra.: 9.50

COORDENADAS: E(X): 542800.05 N(Y): 7627973.22
LAT: -21°27'0.6071" LONG: -50°35'12.9502"

CLEALCO - AÇÚCAR E ALCOOL S/A - DEPARTAMENTO DE TOPOGRAFIA

UNIDADE: I
PARTE: A/A
FUNDO AGRÍCOLA: 303723