
Clealco
Açúcar, Etanol e Energia

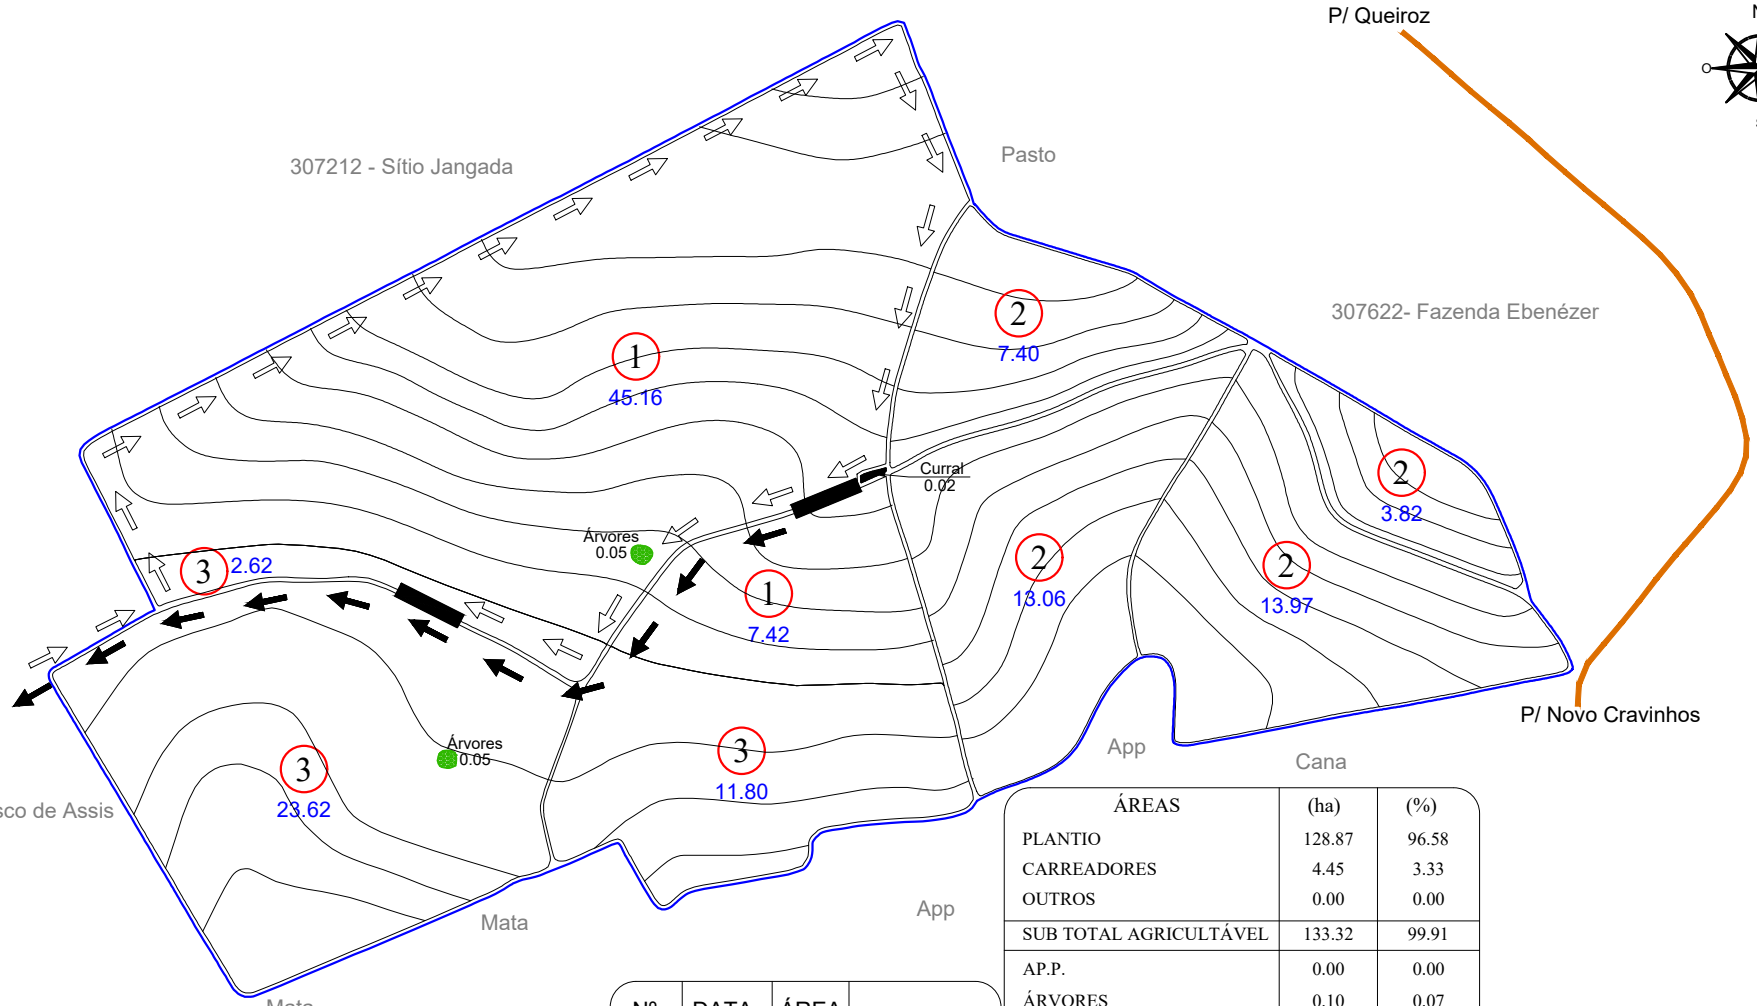

Nº TAL.	DATA PL.	ÁREA (ha)	VARIEDADE
1	05/2022	52.58	RB97 5242
2	05/2024	38.25	CV 7870
3	05/2025	38.04	RB07 5322
TOTAL PLANTIO		128.87	

ÁREAS	(ha)	(%)
PLANTIO	128.87	96.58
CARREADORES	4.45	3.33
OUTROS	0.00	0.00
SUB TOTAL AGRICULTÁVEL	133.32	99.91
AP.P.	0.00	0.00
ÁRVORES	0.10	0.07
OUTROS	0.02	0.01
SUB TOTAL NÃO AGRICULT.	0.12	0.09
ÁREA TOTAL	133.44	100.00

C. NÍVEL: 19231.11 m/l 4.42 ha 3.31 %


ESCALA: 1: 10.000

LEGENDA

- FAZENDA
- TALHÃO
- REDE ELÉTRICA
- TERRAÇO BASE LARGA
- TERRAÇO EMBUTIDO
- VAZIO
- CARREGADO

ESPAÇAMENTO: 1.50 x 1.50
TIRO MÉDIO ESTIMADO: 000.00 m
D.V: 5.30%

CROQUI DE ACESSO

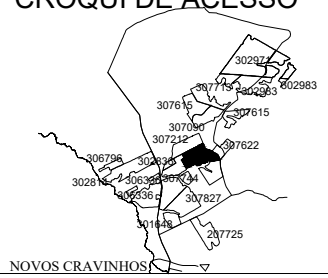

SÍTIO SANTA CRUZ

PROPRIETÁRIO: MILTON ZANCHETTIN
COMPRADOR: CLEALCO
MUNICÍPIO: POMPÉIA - SP

DISTÂNCIAS (km):
UNID. I - Asfalto: 82.50 Terra.: 7.00
UNID.I I - Asfalto: 19.00 Terra.: 8.00

COORDENADAS: E(X): 591675.88 N(Y): 7574049.66
LAT: -21°56'7.7115" LONG: -50°6'44.1865"
CLEALCO - AÇÚCAR E ALCOOL S/A - DEPARTAMENTO DE GEOTECNOLOGIA

LEVANTAMENTO VIA:
SATÉLITE
GPS / VANT
GOOGLE

UNIDADE: II
PARTE: A/A
FUNDO AGRÍCOLA: 303767

M:\01-Mapa de safra\Mapas Atualizados\Terceiro\303767 - Sítio Santa Cruz (Milton Zanchettin)\303767 - Sítio Santa Cruz (Milton Zanchettin).dwg

Bruno Gamboa 03/12/25