
Clealco
Açúcar, Etanol e Energia

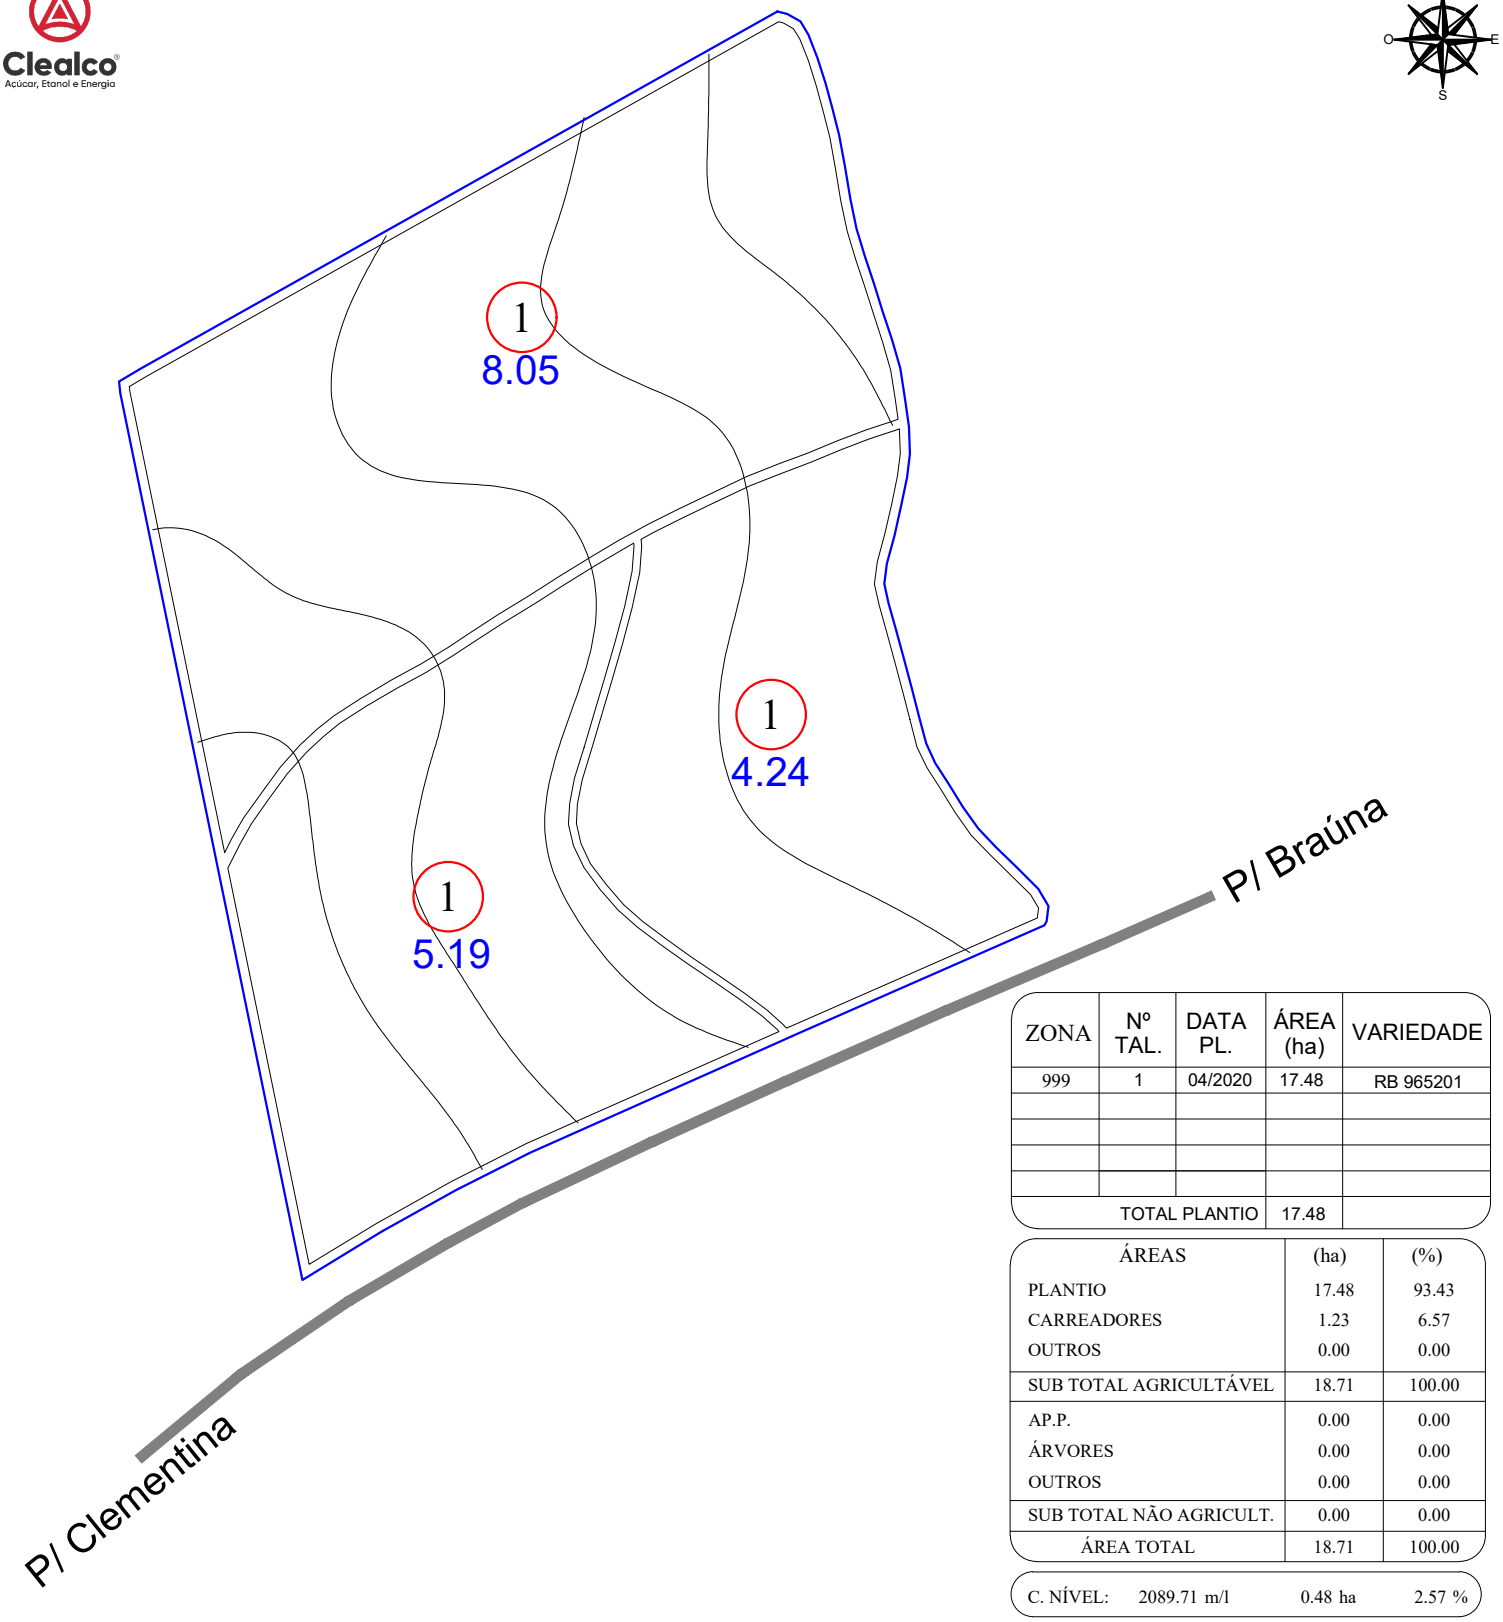

ZONA	Nº TAL.	DATA PL.	ÁREA (ha)	VARIEDADE
999	1	04/2020	17.48	RB 965201
		TOTAL PLANTIO	17.48	

ÁREAS	(ha)	(%)
PLANTIO	17.48	93.43
CARREADORES	1.23	6.57
OUTROS	0.00	0.00
SUB TOTAL AGRICULTÁVEL	18.71	100.00
AP.P.	0.00	0.00
ÁRVORES	0.00	0.00
OUTROS	0.00	0.00
SUB TOTAL NÃO AGRICULT.	0.00	0.00
ÁREA TOTAL	18.71	100.00

C. NÍVEL: 2089.71 m/l 0.48 ha 2.57 %


LEGENDA

- FAZENDA
- TALHÃO
- REDE ELÉTRICA
- TERRAÇO BASE LARGA
- TERRAÇO EMBUTIDO
- (P.O.A) PATIO DE OPERAÇÃO

ESPAÇAMENTO: 1.50 x 1.50
TIRO MÉDIO ESTIMADO: 191.46 m
D.V: 6.48%

ESCALA: 1: 4.000

CROQUI DE ACESSO

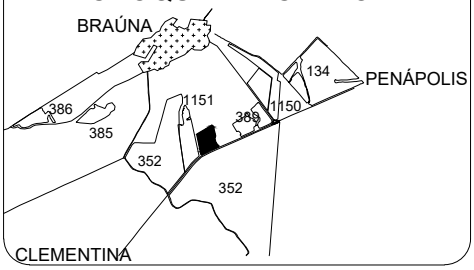

SÍTIO LUIZ XV

PROPRIETÁRIO: JAIME LUIZ DE ROSSI
COMPRADOR: CLEALCO
MUNICÍPIO: BRAÚNA - SP

DISTÂNCIAS (km):
UNID. I - Asfalto: 18.50 Terra.: 0.00
UNID.I I - Asfalto: 40.00 Terra.: 0.00

COORDENADAS: E(X): 571079.06 N(Y): 7619920.15
LAT: -21°31'19.3000" LONG: -50°18'49.2360"

CLEALCO - AÇÚCAR E ALCOOL S/A - DEPARTAMENTO DE GEOTECNOLOGIA

LEVANTAMENTO VIA:
- SATÉLITE
- GPS / VANT
- GOOGLE

UNIDADE: I
PARTE: A/A
FUNDO AGRÍCOLA: 303828

M:\01-Mapa de safra\Mapas Atualizados\Terceiro\303828 - Sítio Luiz XV (Jaime Luiz de Rossi)\303828 - Sítio Luiz XV (Jaime Luiz de Rossi).dwg

Bruno Gamboa 21/08/25