

Clealco
Açúcar, Etanol e Energia

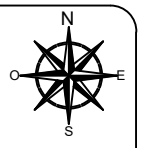

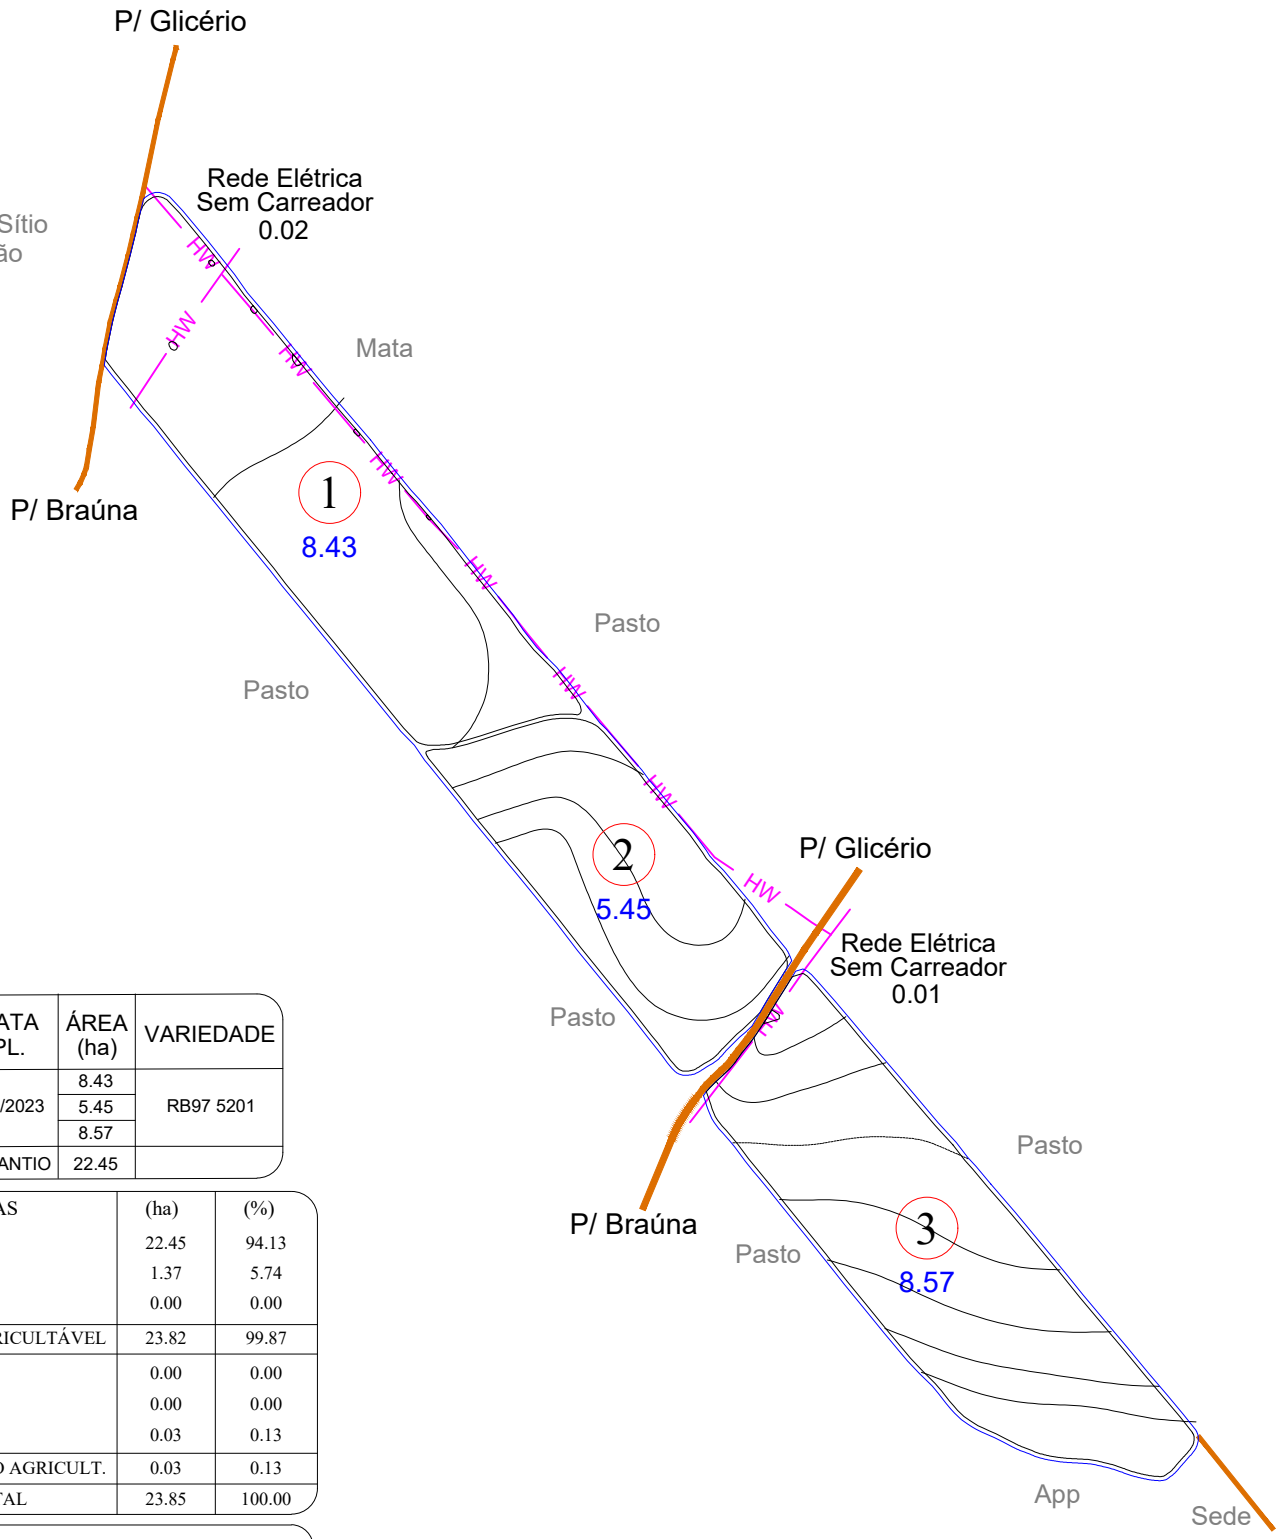

ZONA	Nº TAL.	DATA PL.	ÁREA (ha)	VARIEDADE
999	1	05/2023	8.43	RB97 5201
	2		5.45	
	3		8.57	
TOTAL PLANTIO			22.45	

ÁREAS	(ha)	(%)
PLANTIO	22.45	94.13
CARREADORES	1.37	5.74
OUTROS	0.00	0.00
SUB TOTAL AGRICULTÁVEL	23.82	99.87
AP.P.	0.00	0.00
ÁRVORES	0.00	0.00
OUTROS	0.03	0.13
SUB TOTAL NÃO AGRICULT.	0.03	0.13
ÁREA TOTAL	23.85	100.00

C. NÍVEL: 2839.89 m/l 0.65 ha 2.74 %


LEGENDA

- FAZENDA
- TALHÃO
- REDE ELÉTRICA
- TERRAÇO BASE LARGA
- TERRAÇO EMBUTIDO
- (P.O.A) PATIO DE OPERAÇÃO

ESPAÇAMENTO: 1.50 x 1.50
TIRO MÉDIO ESTIMADO: 170.69 m
D.V: 5.55 %

ESCALA: 1: 0.000

CROQUI DE ACESSO

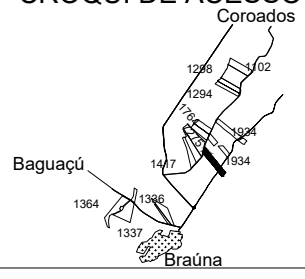

SÍTIO SANTO ANTONIO II

PROPRIETÁRIO: GILBERTO DIAS AVELHAN
COMPRADOR: CLEALCO
MUNICÍPIO: BRAUNA - SP

DISTÂNCIAS (km):
UNID. I - Asfalto: 26.50 Terra.: 1.70
UNID.I I - Asfalto: 80.00 Terra.: 1.50

COORDENADAS: E(X): 572776.99 N(Y): 7624885.92
LAT: -21°28'37.5481" LONG: -50°17'50.9936"

CLEALCO - AÇÚCAR E ALCOOL S/A - DEPARTAMENTO DE GEOTECNOLOGIA

LEVANTAMENTO VIA:
- SATÉLITE
- GPS / VANT
- GOOGLE

UNIDADE: I
PARTE: A/A
FUNDO AGRÍCOLA: 303941

M:\01-Mapa de safra\Mapas Atualizados\Terceiro\303941 - Sítio Santo Antonio II (Gilberto Dias Avelhan)\303941 - Sítio Santo Antonio II (Gilberto Dias Avelhan).dwg

Bruno Gamboa 19/09/2025