Clealco
Açúcar, Etanol e Energia


ÁREAS	(ha)	(%)
PLANTIO	318.26	95.47
CARREADORES	14.63	4.39
OUTROS	0.00	0.00
SUB TOTAL AGRICULTÁVEL	332.89	99.86
AP.P.	0.00	0.00
ÁRVORES	0.48	0.14
OUTROS	0.00	0.00
SUB TOTAL NÃO AGRICULT.	0.48	0.14
ÁREA TOTAL	333.37	100.00

C. NÍVEL: 27542.75 m/l 6.33 ha 1.90 %

LEGENDA
- FAZENDA
- TALHÃO
- REDE ELÉTRICA
- TERRAÇO BASE LARGA
- TERRAÇO EMBUTIDO
- (P.O.A) PATIO DE OPERAÇÃO


ESPAÇAMENTO: 1.50 x 1.50
TIRO MÉDIO ESTIMADO: 000.00 m
D.V: 3.68 %

Nº TAL.	DATA PL.	ÁREA (ha)	VARIEDADE
1	04/2023	13.61	CTC 04
2		4.98	
3	05/2026	4.34	RB96 6928
4	04/2024	4.05	RB 975201
5		7.11	RB 075322
6		6.48	CTC 04
7	03/2019	2.95	RB 975201
8		27.37	CTC 04
9	05/2026	15.36	RB96 6928
10		66.82	
11		38.29	
12		21.36	
13		35.82	
14		11.48	
15		4.49	
16		35.98	
17		17.77	
TOTAL PLANTIO		318.26	

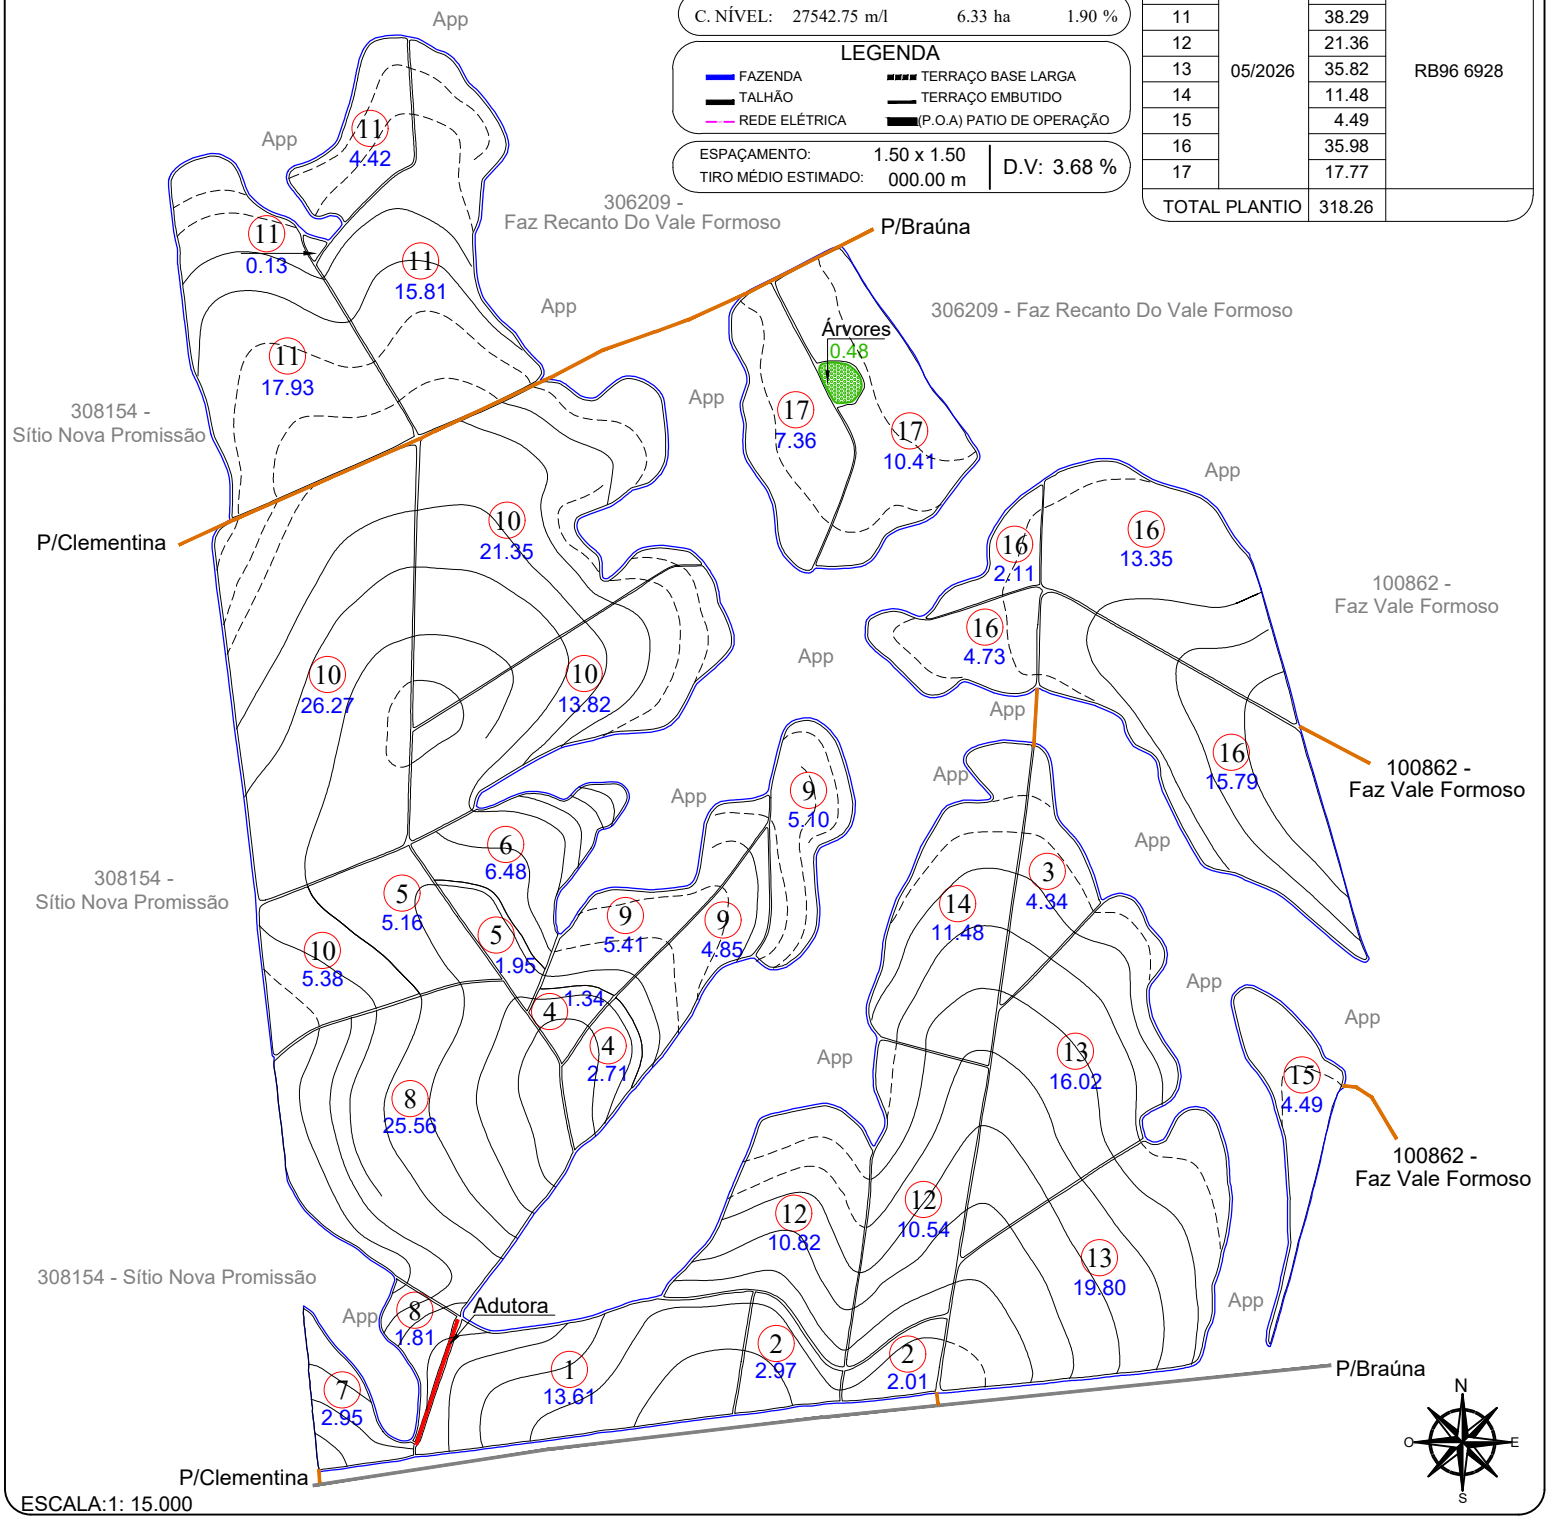

ESCALA:1: 15.000

CROQUI DE ACESSO

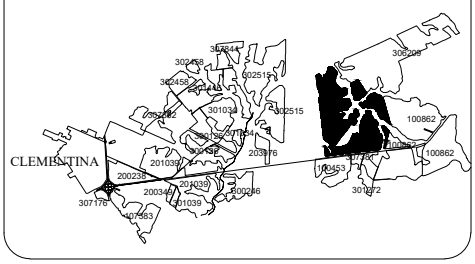

FAZENDA FLÓRIDA

PROPRIETÁRIO: FERNANDO B. AVELHAN
COMPRADOR: CLEALCO
MUNICÍPIO: BRAÚNA - SP

DISTÂNCIAS (km):
UNID. I - Asfalto: 8.60 Terra.: 1.60
UNID.I I - Asfalto: 65.40 Terra.: 1.60

COORDENADAS: E(X): 566708.17 N(Y): 7617159.41
LAT: -21°32'49.6964" LONG: -50°21'20.7682"

CLEALCO - AÇÚCAR E ALCOOL S/A - DEPARTAMENTO DE GEOTECNOLOGIA

LEVANTAMENTO VIA:
- SATÉLITE
- GPS / VANT
- GOOGLE

UNIDADE: I
PARTE: A/A
FUNDO AGRÍCOLA: 303944

M:\01-Mapa de safra\Mapas Atualizados\Terceiro\303944 - Fazenda Florida (Fernado Avelhan)\303944 - Fazenda Florida (Fernado Avelhan).dwg

Bruno Gamboa 09/09/26