

Clealco
Açúcar, Etanol e Energia

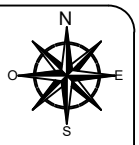

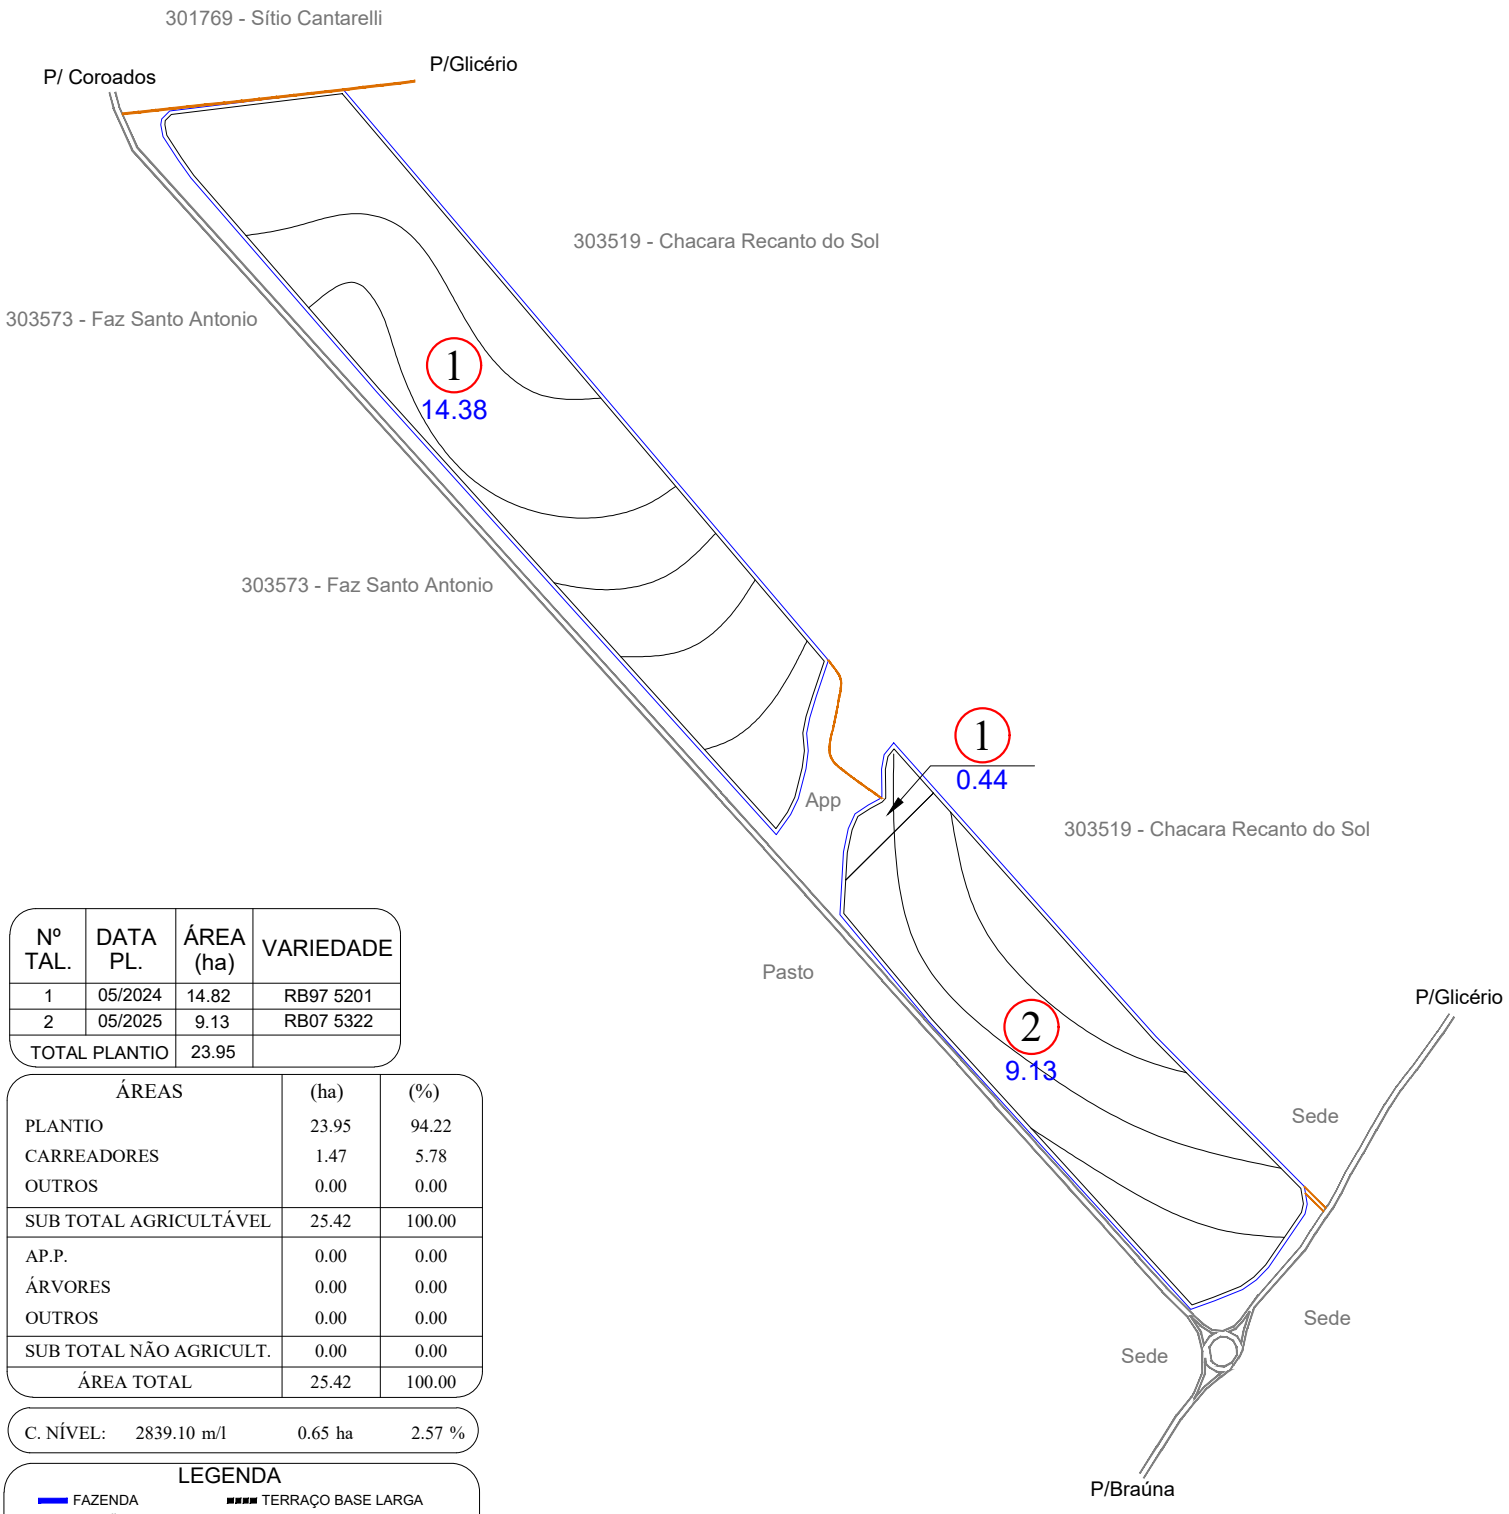

Nº TAL.	DATA PL.	ÁREA (ha)	VARIEDADE
1	05/2024	14.82	RB97 5201
2	05/2025	9.13	RB07 5322
TOTAL PLANTIO		23.95	

ÁREAS	(ha)	(%)
PLANTIO	23.95	94.22
CARREADORES	1.47	5.78
OUTROS	0.00	0.00
SUB TOTAL AGRICULTÁVEL	25.42	100.00
AP.P.	0.00	0.00
ÁRVORES	0.00	0.00
OUTROS	0.00	0.00
SUB TOTAL NÃO AGRICULT.	0.00	0.00
ÁREA TOTAL	25.42	100.00

C. NÍVEL: 2839.10 m/l 0.65 ha 2.57 %


LEGENDA

- FAZENDA
- TALHÃO
- REDE ELÉTRICA
- TERRAÇO BASE LARGA
- TERRAÇO EMBUTIDO
- (P.O.A) PATIO DE OPERAÇÃO

ESPAÇAMENTO: 1.50 x 1.50
TIRO MÉDIO ESTIMADO: 214.93 m
D.V: 6.23 %

ESCALA: 1: 8.000

CROQUI DE ACESSO

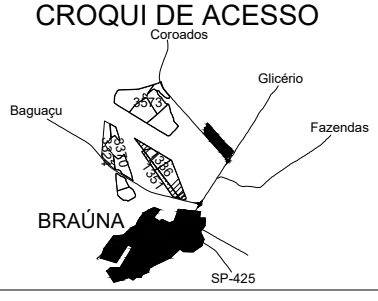

SÍTIO SÃO JOSÉ

PROPRIETÁRIO: PAULO BENTO BOGO
COMPRADOR: CLEALCO
MUNICÍPIO: BRAÚNA - SP

DISTÂNCIAS (km):
UNID. I - Asfalto: 27.50 Terra.: 1.00
UNID.I I - Asfalto: 76.00 Terra.: 3.00

COORDENADAS: E(X): 571431.82 N(Y): 7623896.53
LAT: -21°29'9.9218" LONG: -50°18'37.5843"

CLEALCO - AÇÚCAR E ALCOOL S/A - DEPARTAMENTO DE GEOTECNOLOGIA

LEVANTAMENTO VIA:
- SATÉLITE
- GPS / VANT
- GOOGLE

UNIDADE: I
PARTE: A/A
FUNDO AGRÍCOLA: 303958

M:\01-Mapa de safra\Mapas Atualizados\Terceiro\303958 - Sítio São Jose (Paulo Bento Bogo)\303958 - Sítio São Jose (Paulo Bento Bogo).dwg

Peterson Santos 12/03/2025