
Clealco
Açúcar, Etanol e Energia

Santa America

N
O E
S

307313
FAZENDA CANAA

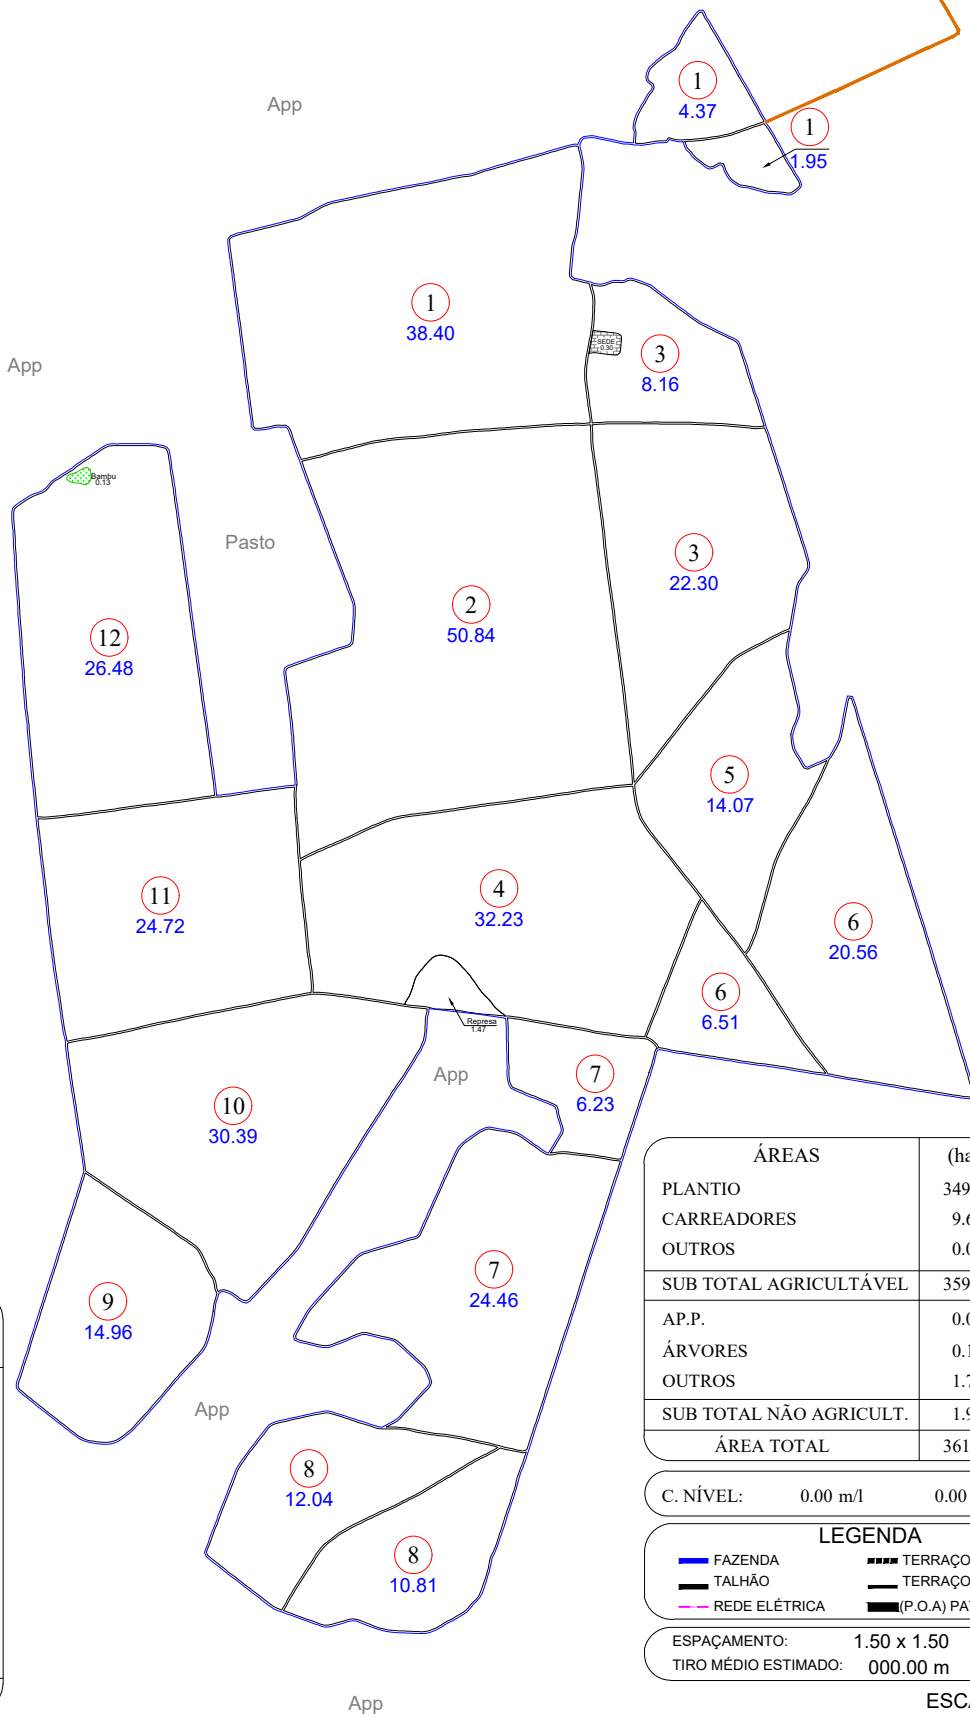

Nº TAL.	DATA PL.	ÁREA (ha)	VARIEDADE
1	2026	44.72	REFORMA
2		50.84	
3		30.46	
4		32.23	
5		14.07	
6		27.07	
7		30.69	
8		22.85	
9		14.96	
10		30.39	
11		24.72	
12		26.48	
TOTAL PLANTIO		349.48	

ÁREAS	(ha)	(%)
PLANTIO	349.48	96.80
CARREADORES	9.65	2.67
OUTROS	0.00	0.00
SUB TOTAL AGRICULTÁVEL	359.13	99.47
AP.P.	0.00	0.00
ÁRVORES	0.13	0.04
OUTROS	1.77	0.49
SUB TOTAL NÃO AGRICULT.	1.90	0.53
ÁREA TOTAL	361.03	100.00

C. NÍVEL: 0.00 m/l 0.00 ha 0.00 %


LEGENDA

- FAZENDA
- TALHÃO
- REDE ELÉTRICA
- TERRAÇO BASE LARGA
- TERRAÇO EMBUTIDO
- (P.O.A) PATIO DE OPERAÇÃO

ESPAÇAMENTO: 1.50 x 1.50
TIRO MÉDIO ESTIMADO: 000.00 m
D.V: 0.00 %

ESCALA: 1: 16.500

CROQUI DE ACESSO

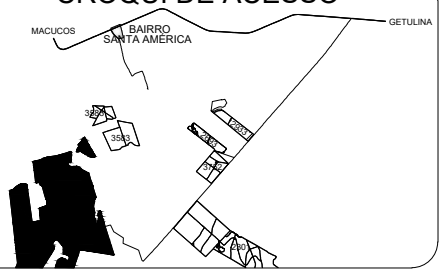

FAZENDA CACHOEIRINHA

PROPRIETÁRIO: WILLIAN AVILA PEREIRA E OUTRO
COMPRADOR: CLEALCO
MUNICÍPIO: GETULINA - SP

DISTÂNCIAS (km):
UNID. I - Asfalto: 84.50 Terra.: 13.60
UNID.I I - Asfalto: 31.50 Terra.: 13.60

COORDENADAS: E(X): 596050.71 N(Y): 7584789.66
LAT: -21°50'17.5973" LONG: -50°4'13.9594"

CLEALCO - AÇÚCAR E ALCOOL S/A - DEPARTAMENTO DE GEOTECNOLOGIA

LEVANTAMENTO VIA:
- SATÉLITE
- GPS / VANT
- GOOGLE

UNIDADE: II
PARTE: A/A
FUNDO AGRÍCOLA: 303963

M:\01-Mapa de safra\Mapas Atualizados\Terceiro\303963 - Fazenda Cachoeirinha (Willian Avila Pereira)\303963 - Fazenda Cachoeirinha (Willian Avila Pereira).dwg

Fabiano Castro 06/03/26