
Clealco
Açúcar, Etanol e Energia



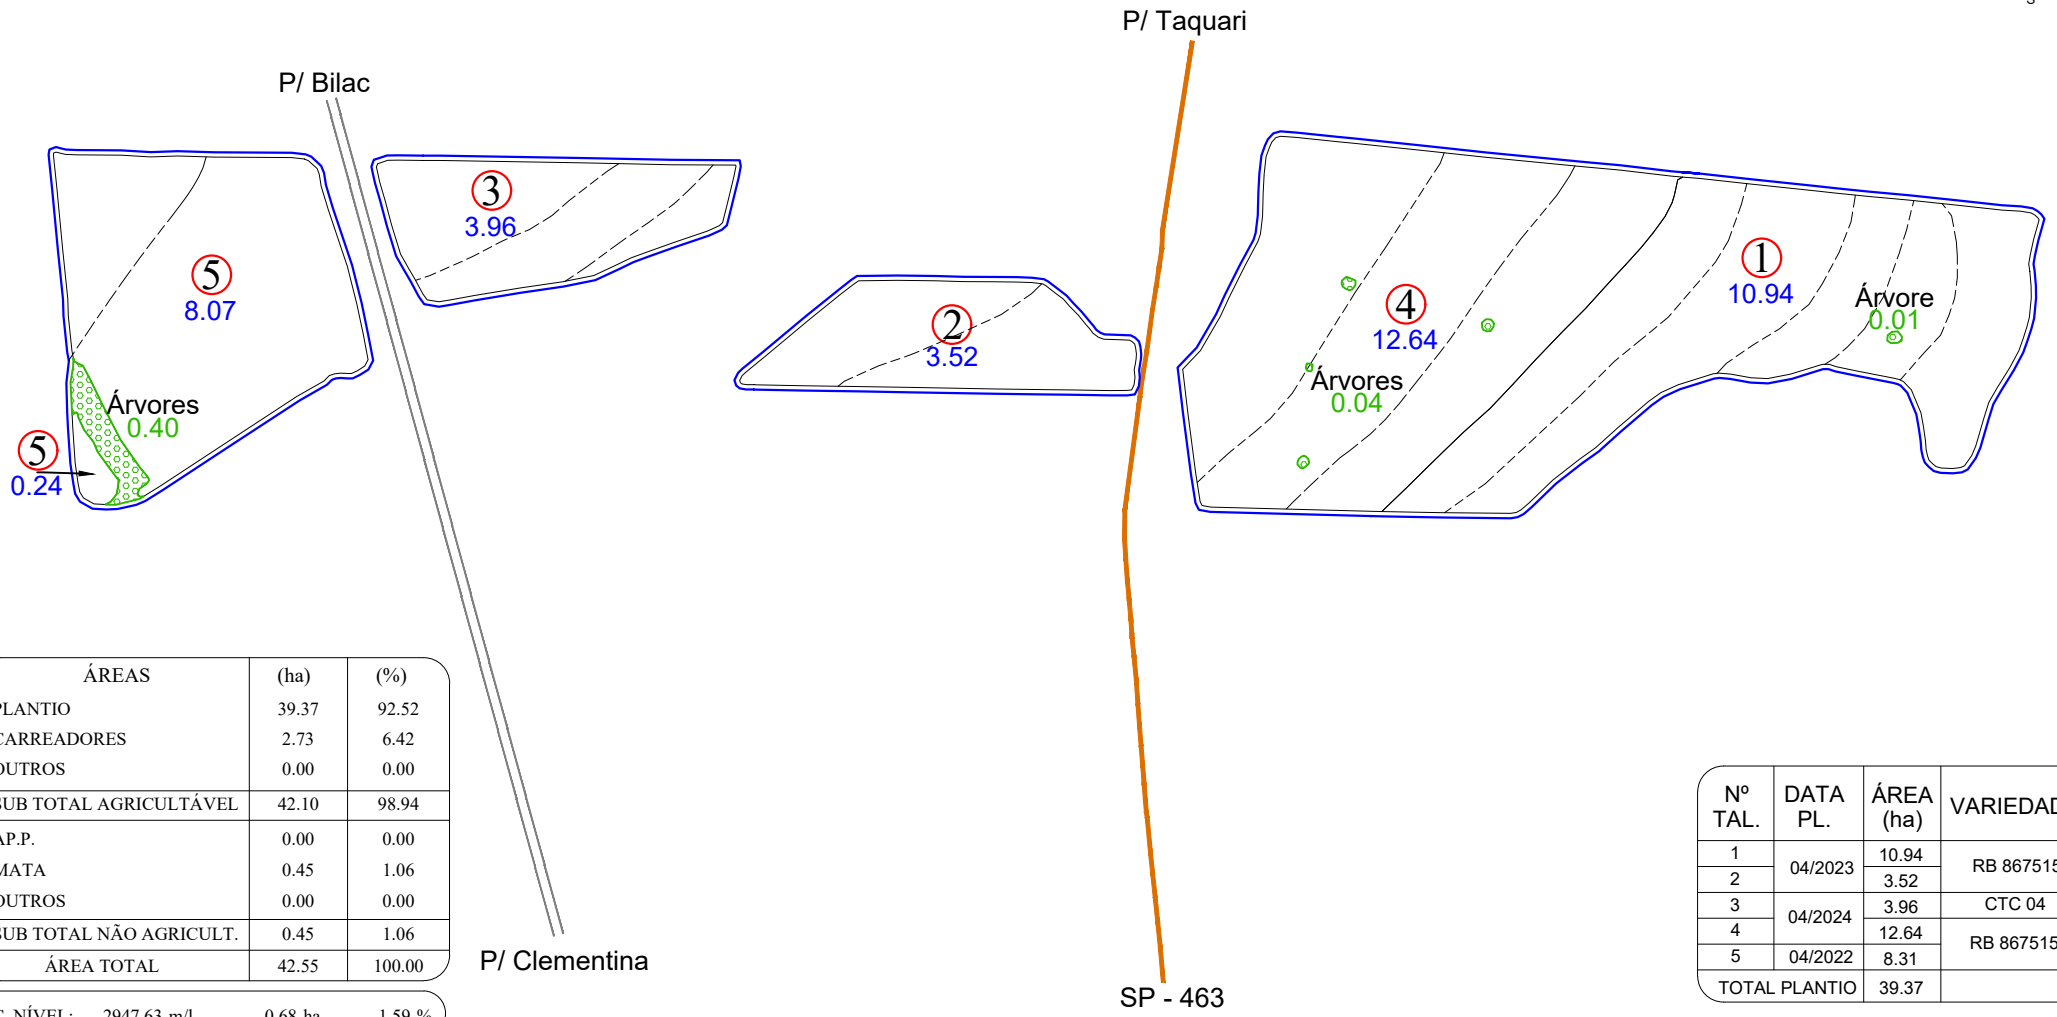

ÁREAS	(ha)	(%)
PLANTIO	39.37	92.52
CARREADORES	2.73	6.42
OUTROS	0.00	0.00
SUB TOTAL AGRICULTÁVEL	42.10	98.94
AP.P.	0.00	0.00
MATA	0.45	1.06
OUTROS	0.00	0.00
SUB TOTAL NÃO AGRICULT.	0.45	1.06
ÁREA TOTAL	42.55	100.00

C. NÍVEL: 2947.63 m/l 0.68 ha 1.59 %


Nº TAL.	DATA PL.	ÁREA (ha)	VARIEDADE
1	04/2023	10.94	RB 867515
2		3.52	
3	04/2024	3.96	CTC 04
4		12.64	RB 867515
5	04/2022	8.31	
TOTAL PLANTIO		39.37	

ESCALA: 1: 8.000

LEGENDA
- FAZENDA
- TALHÃO
- REDE ELÉTRICA
- TERRAÇO BASE LARGA
- TERRAÇO EMBUTIDO

ESPAÇAMENTO: 1.50 x 1.50
TIRO MÉDIO ESTIMADO: 000.00 m
D.V: 4.25 %

CROQUI DE ACESSO

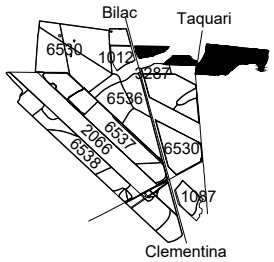

SÍTIO SÃO JUDAS TADEU

PROPRIETÁRIO: PAULO BENTO BOGO
COMPRADOR: CLEALCO
MUNICÍPIO: BILAC - SP

DISTÂNCIAS (km):
UNID. I - Asfalto: 14.30 Terra.: 1.60
UNID.I I - Asfalto: 71.50 Terra.: 1.60

COORDENADAS: E(X): 558142.62 N(Y): 7629001.26
LAT: -21°26'25.6187" LONG: -50°26'20.0308"

CLEALCO - AÇÚCAR E ALCOOL S/A - DEPARTAMENTO DE GEOTECNOLOGIA

LEVANTAMENTO VIA:
- SATÉLITE
- GPS / VANT
- GOOGLE

UNIDADE: I
PARTE: A/A
FUNDO AGRÍCOLA: 303968

M:\01-Mapa de safra\Mapas Atualizados\Terceiro\303968 - Sítio Sao Judas Tadeu (Paulo Bento Bogo)\303968 - Sítio Sao Judas Tadeu (Paulo Bento Bogo).dwg

Benati 11/11/2025