
Clealco
Açúcar, Etanol e Energia

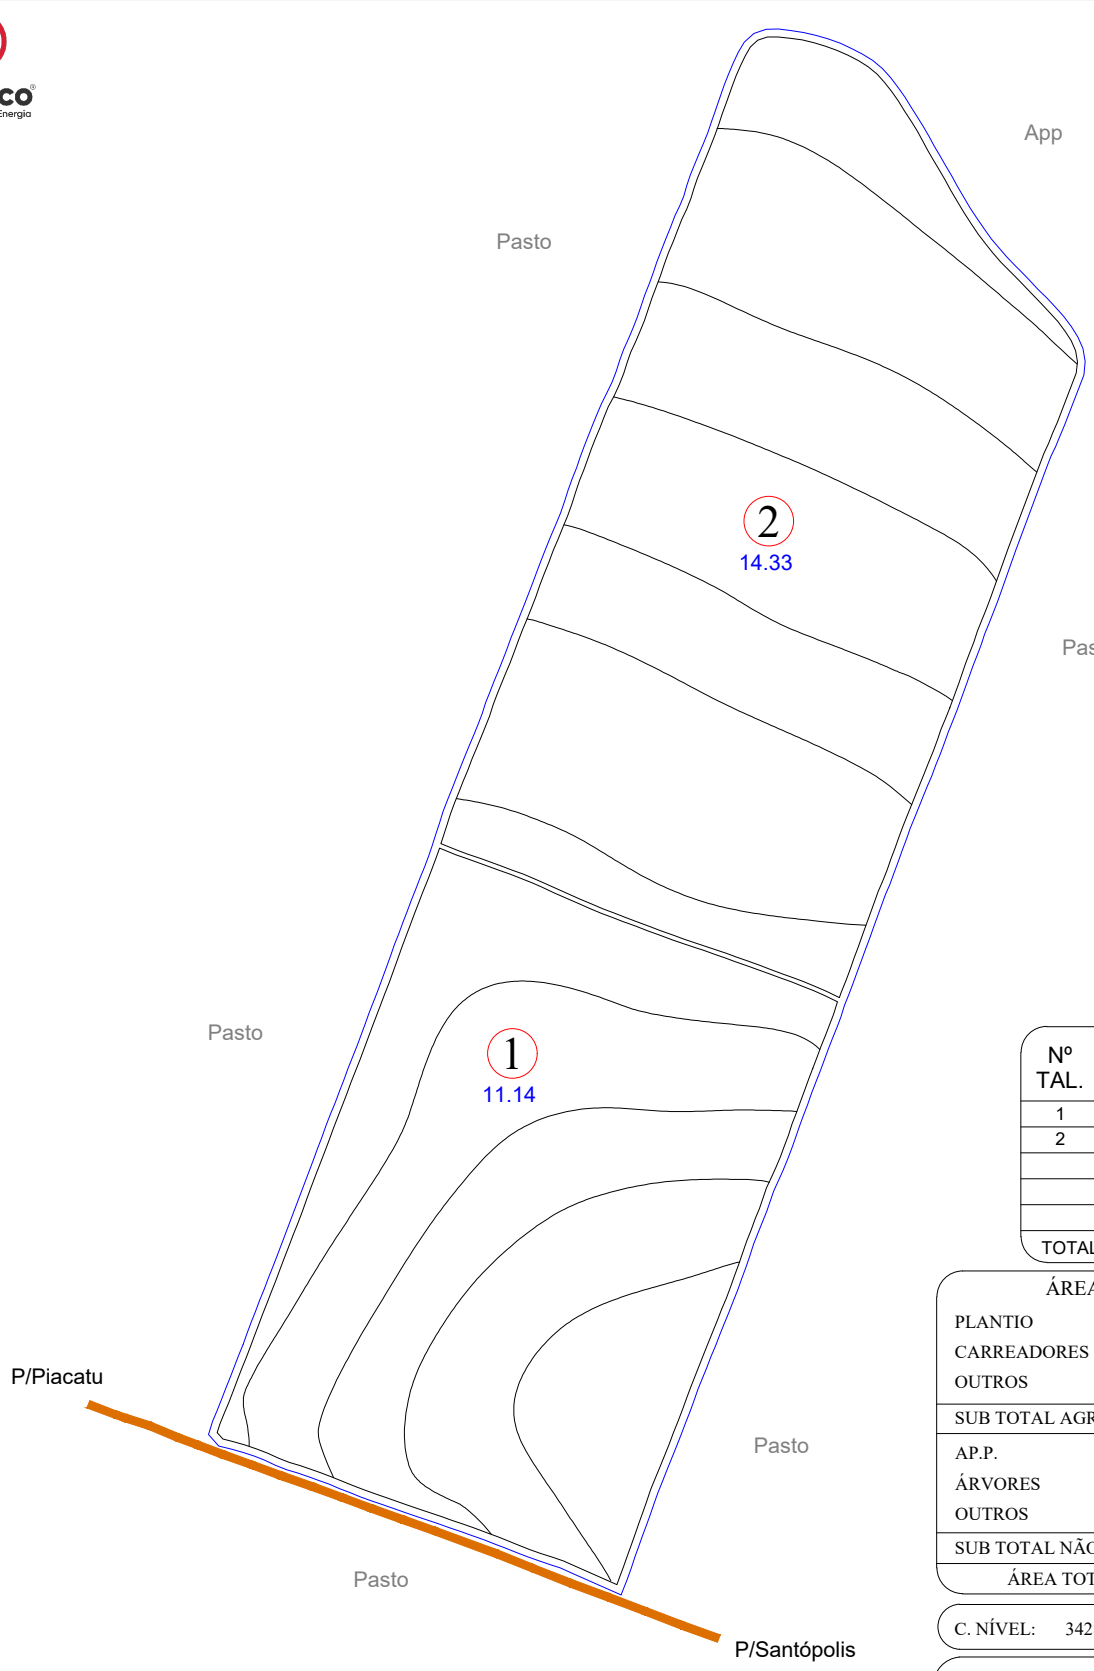

Nº TAL.	DATA PL.	ÁREA (ha)	VARIEDADE
1	07/2019	11.14	CTC 04
2		14.33	
TOTAL PLANTIO		25.47	

ÁREAS	(ha)	(%)
PLANTIO	25.47	95.17
CARREADORES	1.29	4.83
OUTROS	0.00	0.00
SUB TOTAL AGRICULTÁVEL	26.76	100.00
AP.P.	0.00	0.00
ÁRVORES	0.00	0.00
OUTROS	0.00	0.00
SUB TOTAL NÃO AGRICULT.	0.00	0.00
ÁREA TOTAL	26.76	100.00

C. NÍVEL: 3428.03 m/l 0.79 ha 2.95 %


LEGENDA

- FAZENDA
- TALHÃO
- REDE ELÉTRICA
- VAZIO
- TERRAÇO BASE LARGA
- TERRAÇO EMBUTIDO
- (P.O.A) PATIO DE OPERAÇÃO
- CARREGADO

ESPAÇAMENTO: 1.50 x 1.50
TIRO MÉDIO ESTIMADO: 232.25 m
D.V: 5.41 %

ESCALA: 1: 5.000

CROQUI DE ACESSO

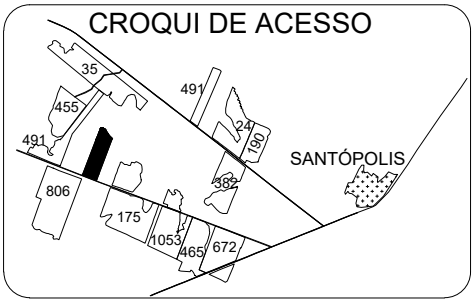

SÍTIO VIRGEM DE GUADALUPE

PROPRIETÁRIO: JOSE HONORIO GASTALDI
COMPRADOR: CLEALCO
MUNICÍPIO: SANTÓPOLIS - SP

DISTÂNCIAS (km):
UNID. I - Asfalto: 17.50 Terra.: 4.50
UNID.I I - Asfalto: 52.00 Terra.: 4.50

COORDENADAS: E(X): 546509.14 N(Y): 7607654.60
LAT: -21°38'1.1434" LONG: -50°33'2.0506"

CLEALCO - AÇÚCAR E ALCOOL S/A - DEPARTAMENTO DE GEOTECNOLOGIA

LEVANTAMENTO VIA:
- SATÉLITE
- GPS / VANT
- GOOGLE

UNIDADE: I
PARTE: A/A
FUNDO AGRÍCOLA: 303987

M:\01-Mapa de safra\Mapas Atualizados\Terceiro\303987 - Sítio Virgem de Guadalupe (Jose Honorio Gastaldi)\303987 - Sítio Virgem de Guadalupe (Jose Honorio Gastaldi).dwg

Bruno Gamboa 23/03/26