
Clealco
Açúcar, Etanol e Energia

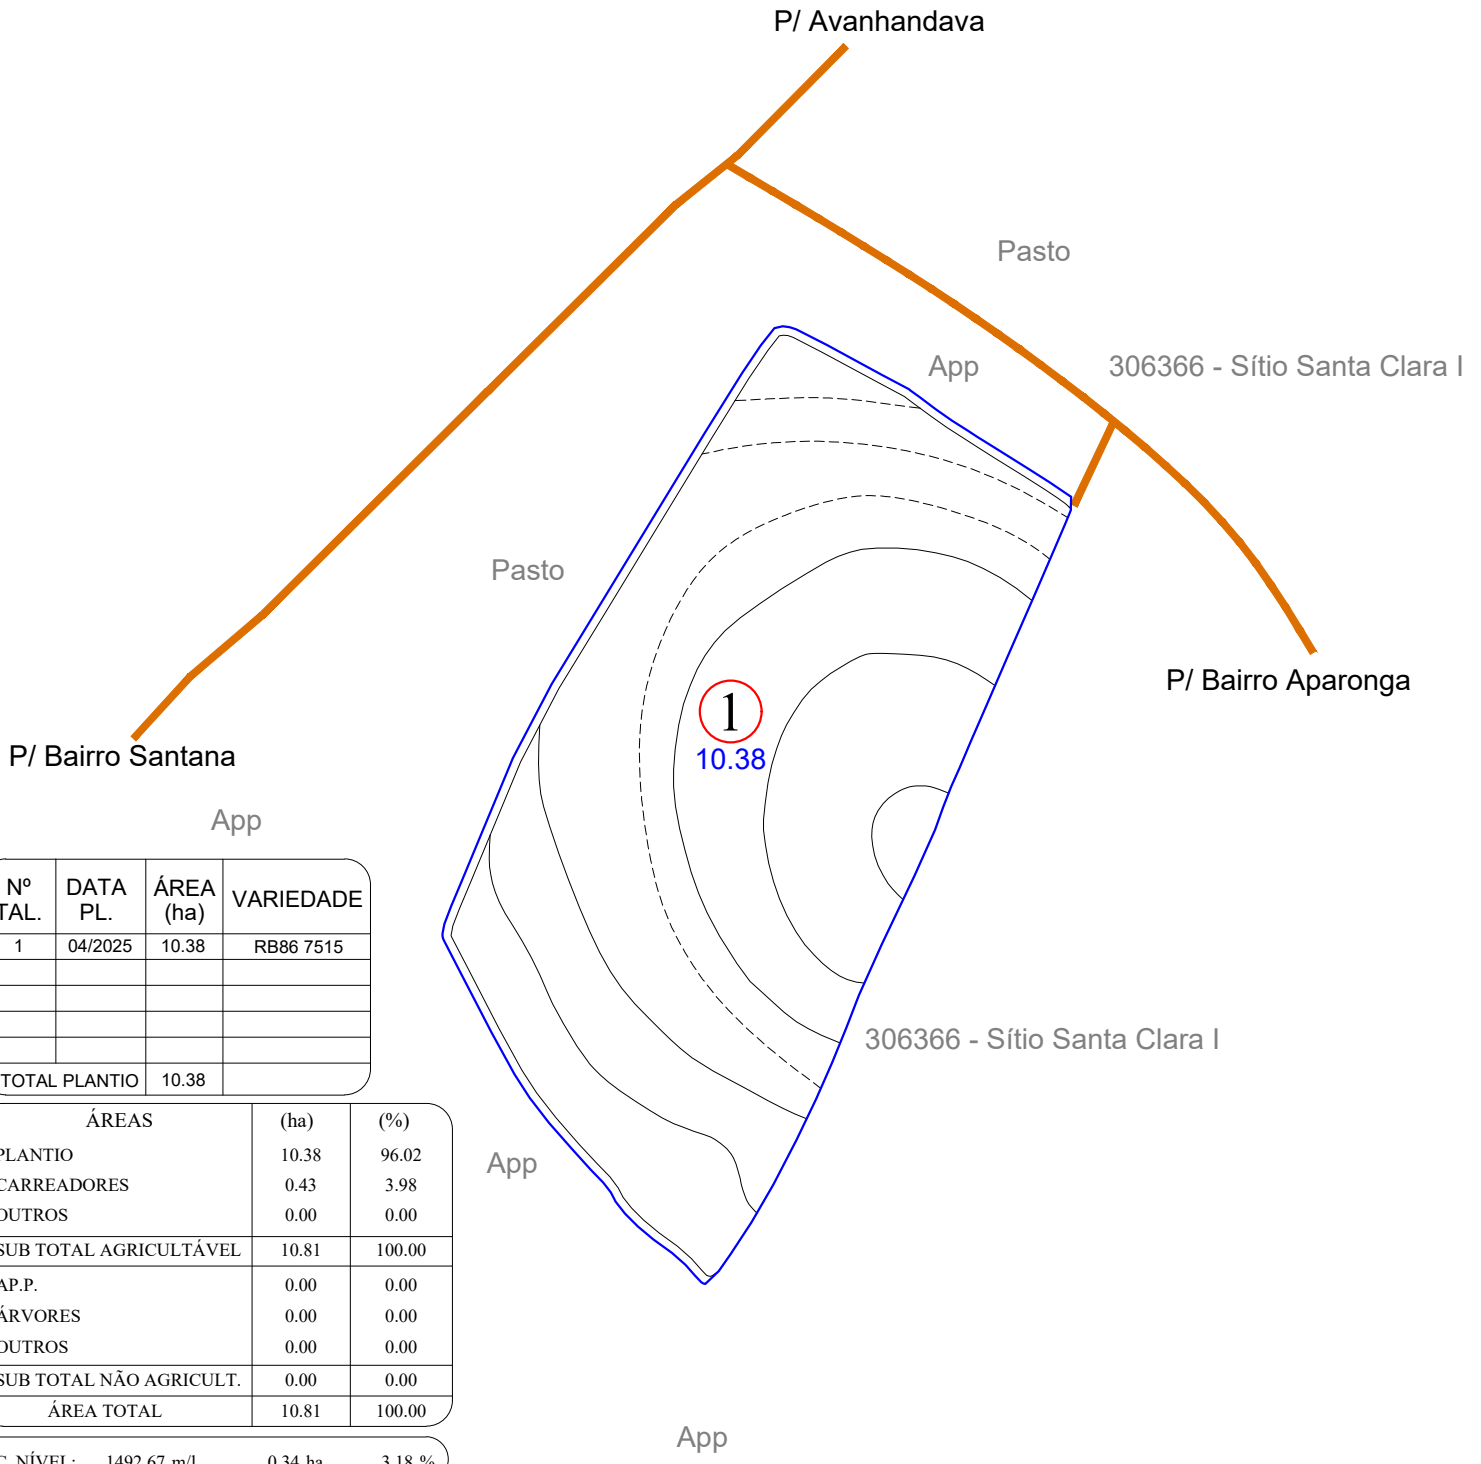

Nº TAL.	DATA PL.	ÁREA (ha)	VARIEDADE
1	04/2025	10.38	RB86 7515
TOTAL PLANTIO		10.38	

ÁREAS	(ha)	(%)
PLANTIO	10.38	96.02
CARREADORES	0.43	3.98
OUTROS	0.00	0.00
SUB TOTAL AGRICULTÁVEL	10.81	100.00
AP.P.	0.00	0.00
ÁRVORES	0.00	0.00
OUTROS	0.00	0.00
SUB TOTAL NÃO AGRICULT.	0.00	0.00
ÁREA TOTAL	10.81	100.00

C. NÍVEL: 1492.67 m/l 0.34 ha 3.18 %


LEGENDA

- FAZENDA
- TALHÃO
- REDE ELÉTRICA
- TERRAÇO BASE LARGA
- TERRAÇO EMBUTIDO
- (P.O.A) PATIO DE OPERAÇÃO

ESPAÇAMENTO: 1.50 x 1.50
TIRO MÉDIO ESTIMADO: 000.00 m
D.V: 4.55 %

ESCALA: 1: 4.500

CROQUI DE ACESSO

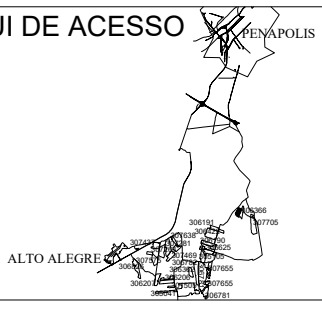

SÍTIO SÃO JOÃO

PROPRIETÁRIO: ALDO CESAR CRIVELLARO
COMPRADOR: CLEALCO
MUNICÍPIO: PENÁPOLIS- SP

DISTÂNCIAS (km):
UNID. I - Asfalto: 48.50 Terra.: 3.00
UNID.I I - Asfalto: 49.50 Terra.: 5.50

COORDENADAS: E(X): 594690.03 N(Y): 7615838.41
LAT: -21°33'28.1116" LONG: -50°5'7.7384"

CLEALCO - AÇÚCAR E ALCOOL S/A - DEPARTAMENTO DE GEOTECNOLOGIA

LEVANTAMENTO VIA:
- SATÉLITE
- GPS / VANT
- GOOGLE

UNIDADE: II
PARTE: A/A
FUNDO AGRÍCOLA: 305077

M:\01-Mapa de safra\Mapas Atualizados\Terceiro\305077 - Sitio São João (Aldo Cesar Crivellaro)\305077 - Sitio São João (Aldo Cesar Crivellaro).dwg

Bruno Gamboa 03/12/25