ZONA D.V.	Nº TAL.	DATA PL.	ÁREA (ha)	VARIEDADE
999 7.69 %	1	06/2023	6.75	CV 7870
	2		6.60	
	3		6.98	RB 975242
	4		9.81	
	5	04/2021	7.71	CTC 04
	6		0.81	
	7	06/2023	2.79	RB 975242
TOTAL PLANTIO			41.45	--------

ÁREAS	(ha)	(%)
PLANTIO	41.45	96.68
CARREADORES	1.42	3.32
OUTROS	0.00	0.00
SUB TOTAL AGRICULTÁVEL	42.87	100.00
AP.P.	0.00	0.00
ÁRVORES	0.00	0.00
OUTROS	0.00	0.00
SUB TOTAL NÃO AGRICULT.	0.00	0.00
ÁREA TOTAL	42.87	100.00

C. NÍVEL: 7362.00 m/l 1.69 ha 3.95 %


LEGENDA

- FAZENDA
- TALHÃO
- CURVA DE NÍVEL
- CARREADOR
- CONFRONTANTE
- REDE ELÉTRICA
- TRAJETO VAZIO
- TRAJETO CARREGADO

PLANTIO MANUAL - ESPAÇAMENTO: 1.50 X 1.50
TIRO MÉDIO ESTIMADO: 191.66m


Clealco
Açúcar, Etanol e Energia

NM

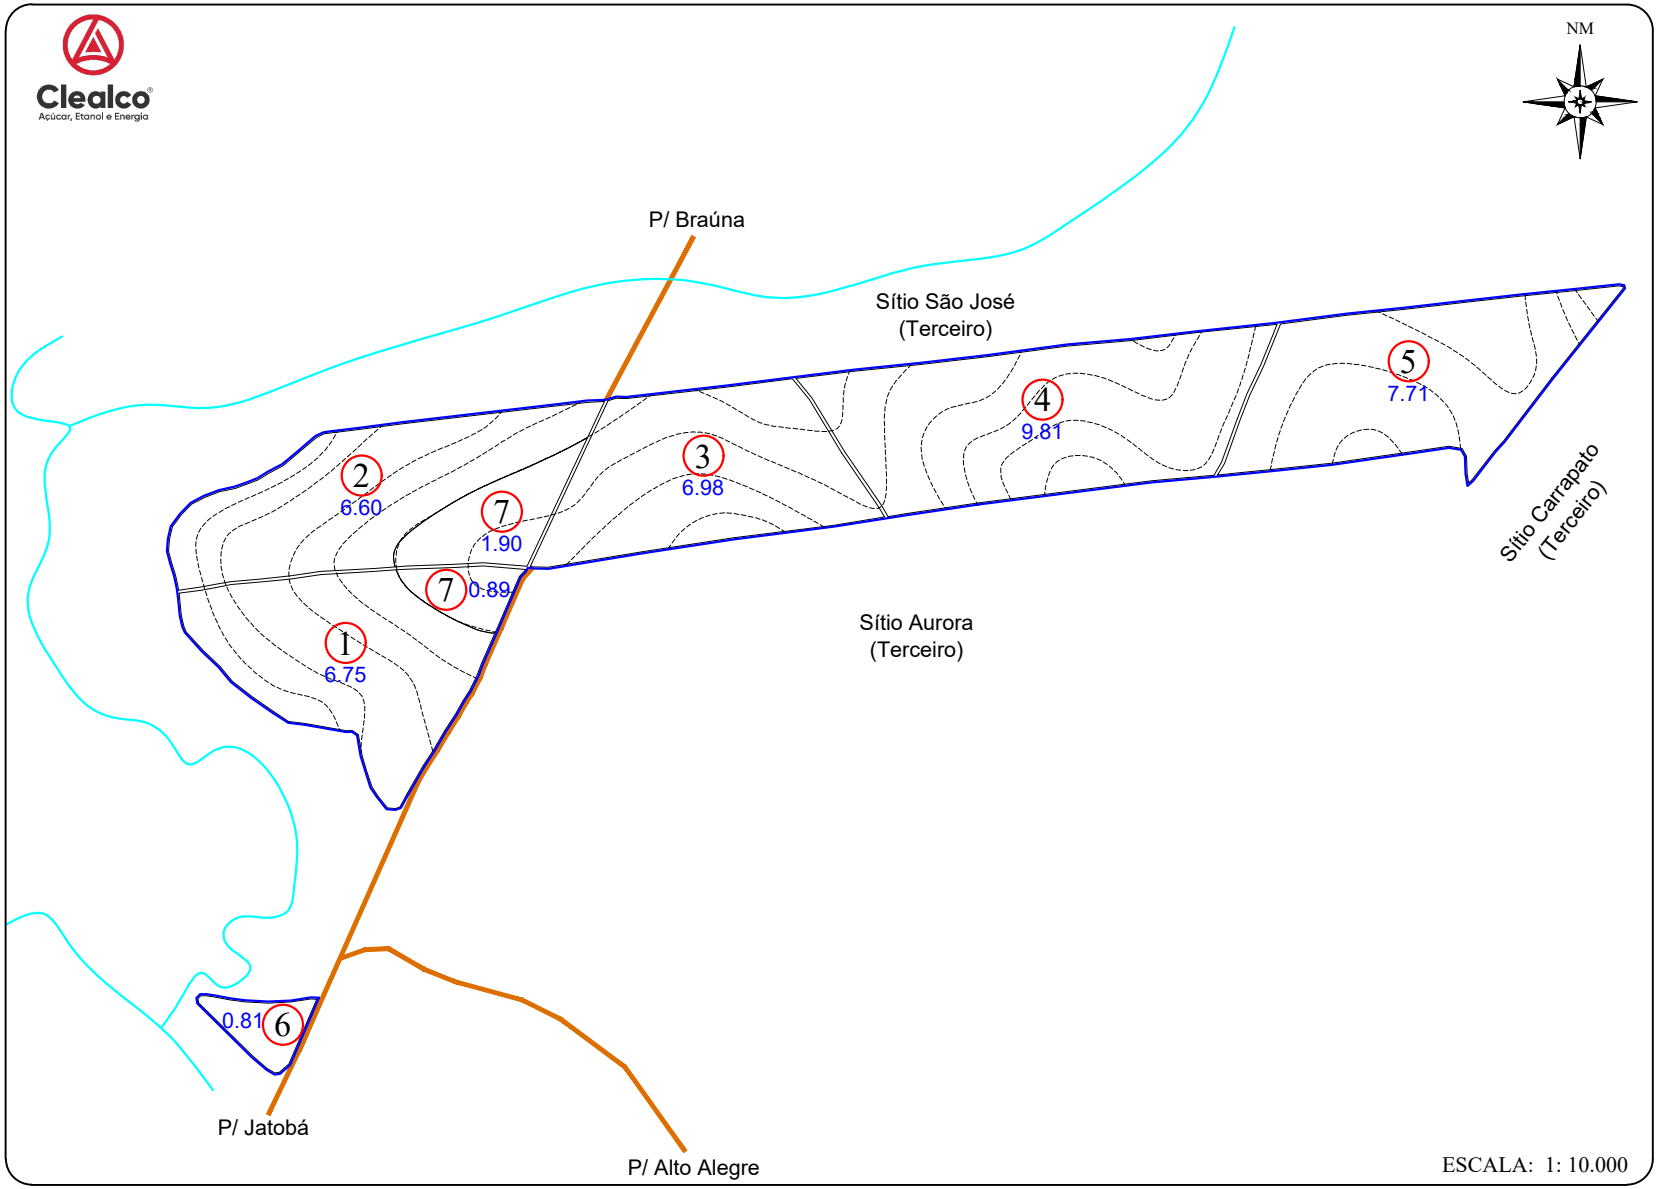

ESCALA: 1: 10.000

CROQUI DE ACESSO

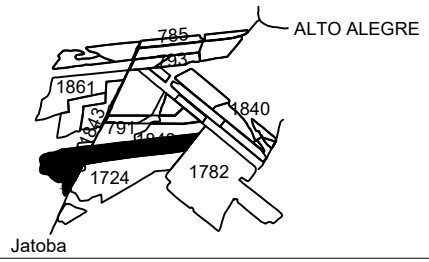

SÍTIO AURORA

PROPRIETÁRIO: PEDRO MIGUEL D. CRUZ
COMPRADOR: CLEALCO S/A
MUNICÍPIO: ALTO ALEGRE

DISTÂNCIAS (km):
UNID. I - Asfalto: 42.90 Terra.: 4.70
UNID.I I - Asfalto: 31.00 Terra.: 4.70
UNID. III -Asfalto: 17.70 Terra.: 9.40

COORDENADAS: E(X): 579748.83 N(Y): 7611518.18
LAT: -21°35'51.2445" LONG: -50°13'46.4445"

CLEALCO - AÇÚCAR E ALCOOL S/A - DEPARTAMENTO DE TOPOGRAFIA

UNIDADE: I
PARTE: A/A
FUNDO AGRÍCOLA: 305093