| ZONA DV | Nº TAL. | DATA PL. | ÁREA (ha) | VAR. |
|---|---|---|---|---|
| 999<br>5.18 % | 1 | 03/2022 | 10.39 | CTC 9001 |
| TOTAL PLANTIO | | | 10.39 | -------- |

| ÁREAS | (ha) | (%) |
|---|---|---|
| PLANTIO | 10.39 | 96.07 |
| CARREADORES | 0.42 | 3.93 |
| OUTROS | 0.00 | 0.00 |
| SUB TOTAL AGRICULTÁVEL | 10.81 | 100.00 |
| AP.P. | 0.00 | 0.00 |
| ÁRVORES | 0.00 | 0.00 |
| OUTROS | 0.00 | 0.00 |
| SUB TOTAL NÃO AGRICULT. | 0.00 | 0.00 |
| ÁREA TOTAL | 10.81 | 100.00 |

| | | | |
|---|---|---|---|
| C. NÍVEL: | 1964.36 m/l | 0.45 ha | 4.18 % |

## LEGENDA

| | |
|---|---|
| FAZENDA | CONFRONTANTE |
| TALHÃO | REDE ELÉTRICA |
| CURVA DE NÍVEL | TRAJETO VAZIO |
| CARREADOR | TRAJETO CARREGADO |

PLANTIO MANUAL - ESPAÇAMENTO: 1.50 X 1.50
TIRO MÉDIO ESTIMADO: 146.99 m

Clealco
Açúcar, Etanol e Energia

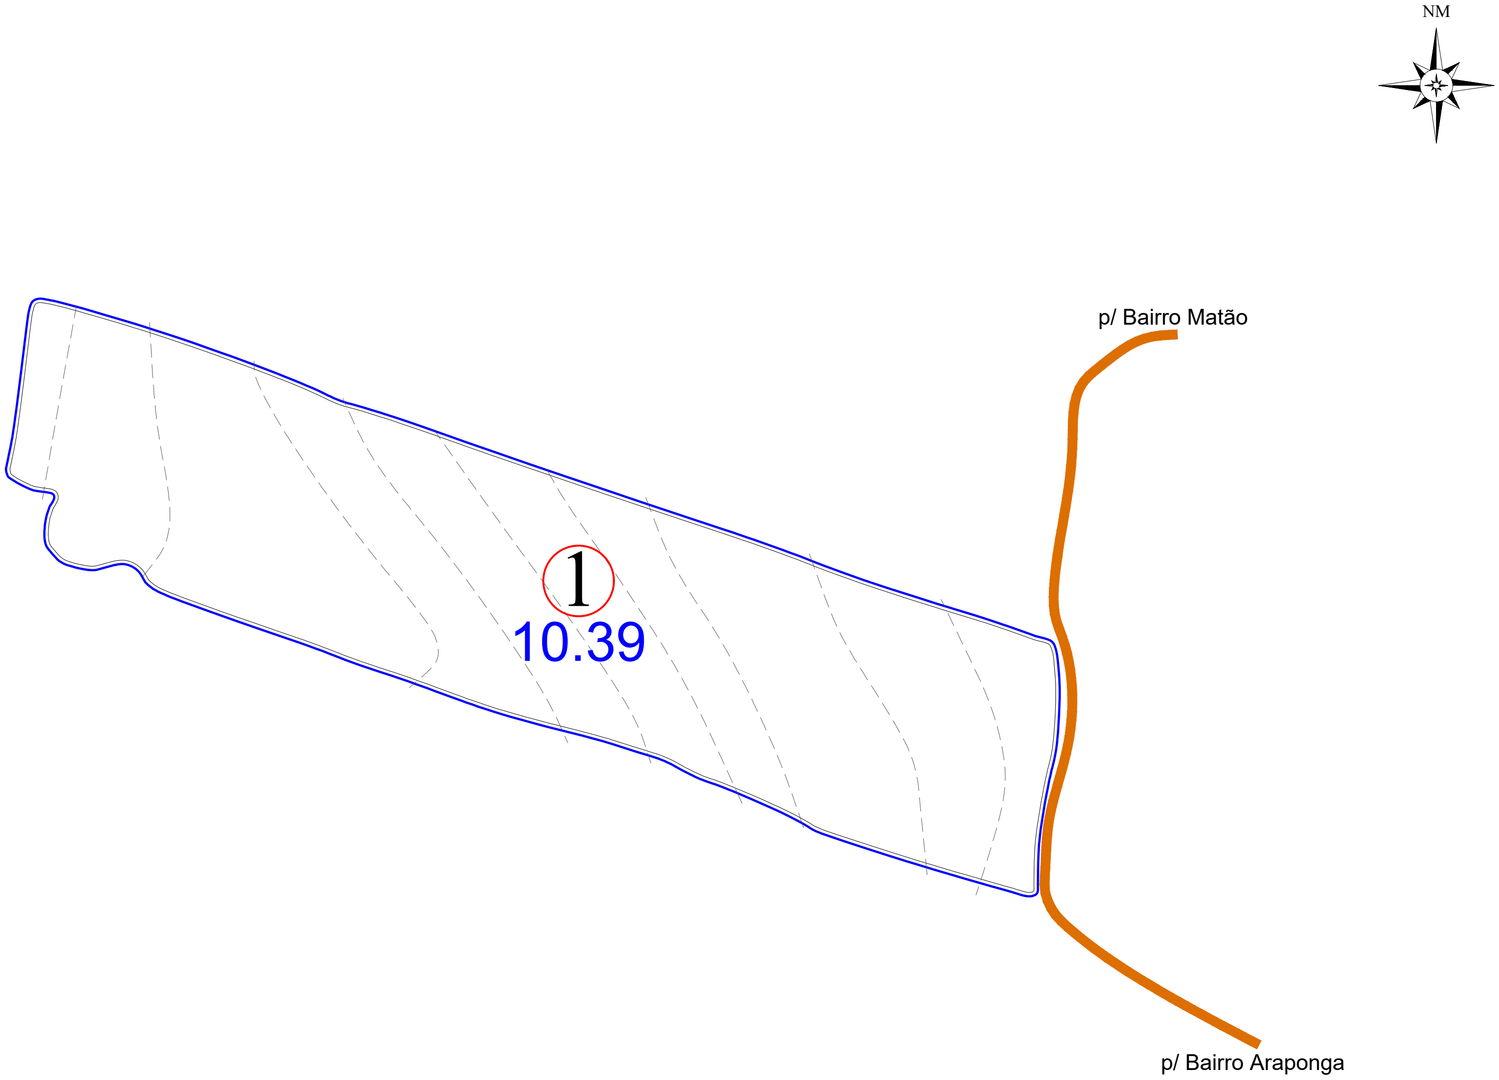

ESCALA: 1: 8.000

## CROQUI DE ACESSO

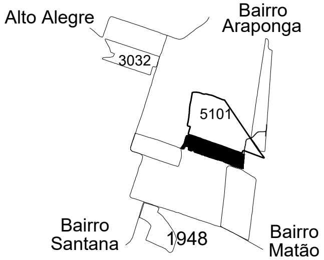

## SITIO SANTA CLARA II

| | |
|---|---|
| PROPRIETÁRIO: | ANTONIO I. DE ANDRADE |
| COMPRADOR: | CLEALCO S/A |
| MUNICÍPIO: | PENÁPOLIS |

DISTÂNCIAS (km):

| | Asfalto: | | Terra.: | |
|---|---|---|---|---|
| UNID. I - | Asfalto: | 51.60 | Terra.: | 6.50 |
| UNID.I I - | Asfalto: | 46.50 | Terra.: | 6.50 |
| UNID. III - | Asfalto: | 6.00 | Terra.: | 8.00 |

COORDENADAS: E(X): 594128 N(Y): 7613727
LAT: 21° 34' 36,61793" LONG: 50° 05' 26,86284"

CLEALCO - AÇÚCAR E ALCOOL S/A - DEPARTAMENTO DE TOPOGRAFIA

UNIDADE:
II

PARTE:
A/A

FUNDO AGRÍCOLA:
305184

M:\01-Mapa de safra\Mapas Atualizados\Terceiro\305184 - Sitio Santa Clara II - (Antonio I. de Andrade)\305184 - Sitio Santa Clara II - (Antonio I. de Andrade).dwg

Benati 13/04/2023