
Clealco
Açúcar, Etanol e Energia

Nº TAL.	DATA PL.	ÁREA (ha)	VARIEDADE
1	05/2025	16.99	RB975242 / RB075322
2	2026	7.79	REFORMA
3		3.84	
4	04/2023	7.50	RB 975242
5		7.18	
TOTAL PLANTIO		43.30	

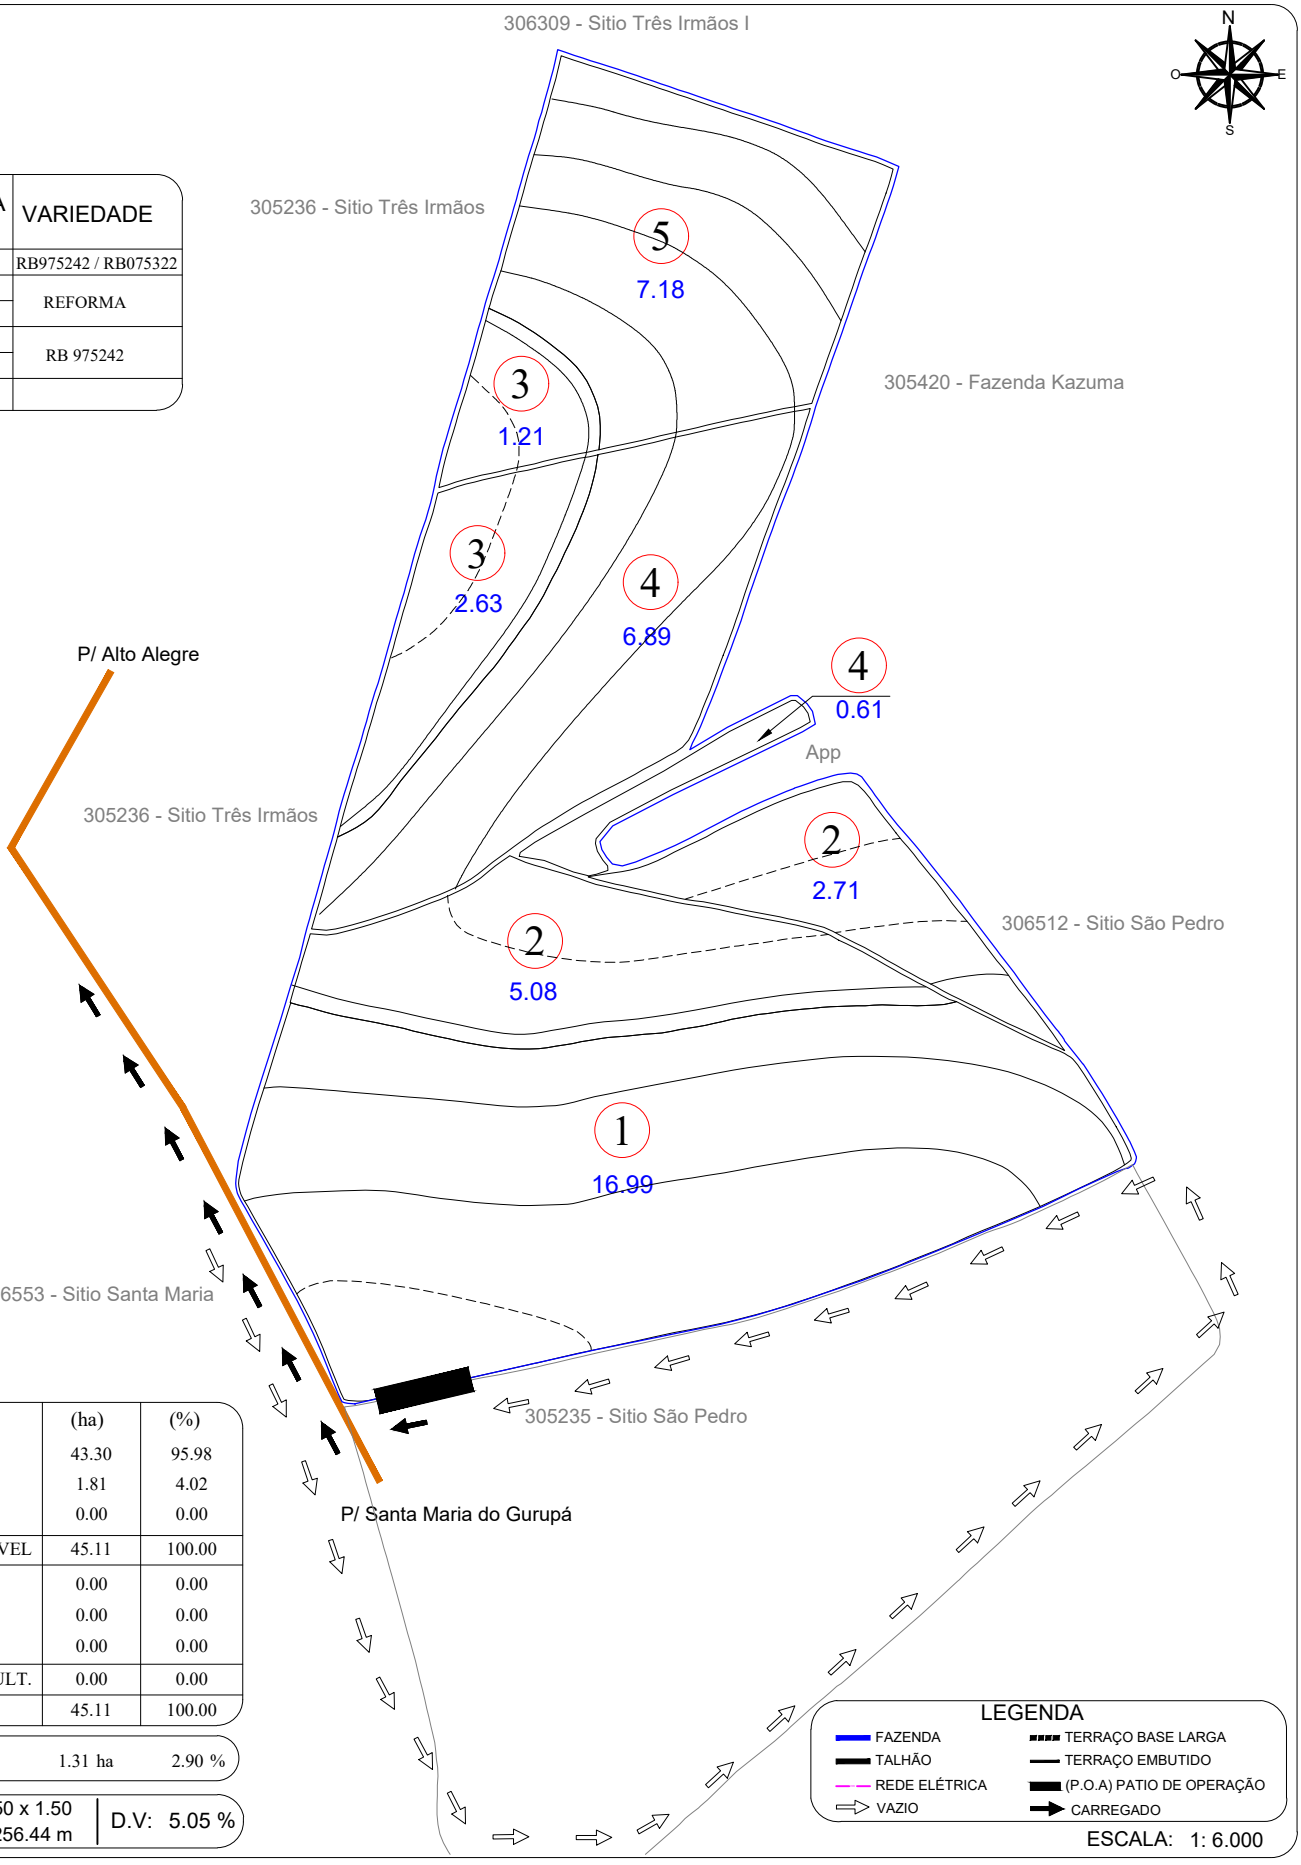

ÁREAS	(ha)	(%)
PLANTIO	43.30	95.98
CARREADORES	1.81	4.02
OUTROS	0.00	0.00
SUB TOTAL AGRICULTÁVEL	45.11	100.00
AP.P.	0.00	0.00
ÁRVORES	0.00	0.00
OUTROS	0.00	0.00
SUB TOTAL NÃO AGRICULT.	0.00	0.00
ÁREA TOTAL	45.11	100.00


C. NÍVEL: 5693.52 m/l 1.31 ha 2.90 %

ESPAÇAMENTO: 1.50 x 1.50
TIRO MÉDIO ESTIMADO: 256.44 m
D.V: 5.05 %

LEGENDA
- FAZENDA
- TALHÃO
- REDE ELÉTRICA
- VAZIO
- TERRAÇO BASE LARGA
- TERRAÇO EMBUTIDO
- (P.O.A) PATIO DE OPERAÇÃO
- CARREGADO

ESCALA: 1: 6.000

CROQUI DE ACESSO

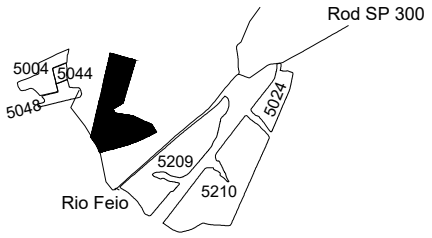

SÍTIO SANTA MARIA

PROPRIETÁRIO: JOSE LUIZ PONTIN
COMPRADOR: CLEALCO
MUNICÍPIO: PROMISSAO - SP

DISTÂNCIAS (km):
UNID. I - Asfalto: 70.00 Terra.: 0.60
UNID.I I - Asfalto: 48.00 Terra.: 14.50

COORDENADAS: E(X): 597809.62 N(Y): 7611029.66
LAT: -21°36'3.8954" LONG: -50°3'18.2706"

LEVANTAMENTO VIA:
- SATÉLITE
- GPS / VANT
- GOOGLE

CLEALCO - AÇÚCAR E ALCOOL S/A - DEPARTAMENTO DE GEOTECNOLOGIA

UNIDADE: II
PARTE: A/A
FUNDO AGRÍCOLA: 305237

M:\01-Mapa de safra\Mapas Atualizados\Terceiro\305237 - Sitio Santa Maria (Jose Luiz Pontin)\305237 - Sitio Santa Maria (Jose Luiz Pontin).dwg

Bruno Gamboa 27/01/26