
Clealco
Açúcar, Etanol e Energia

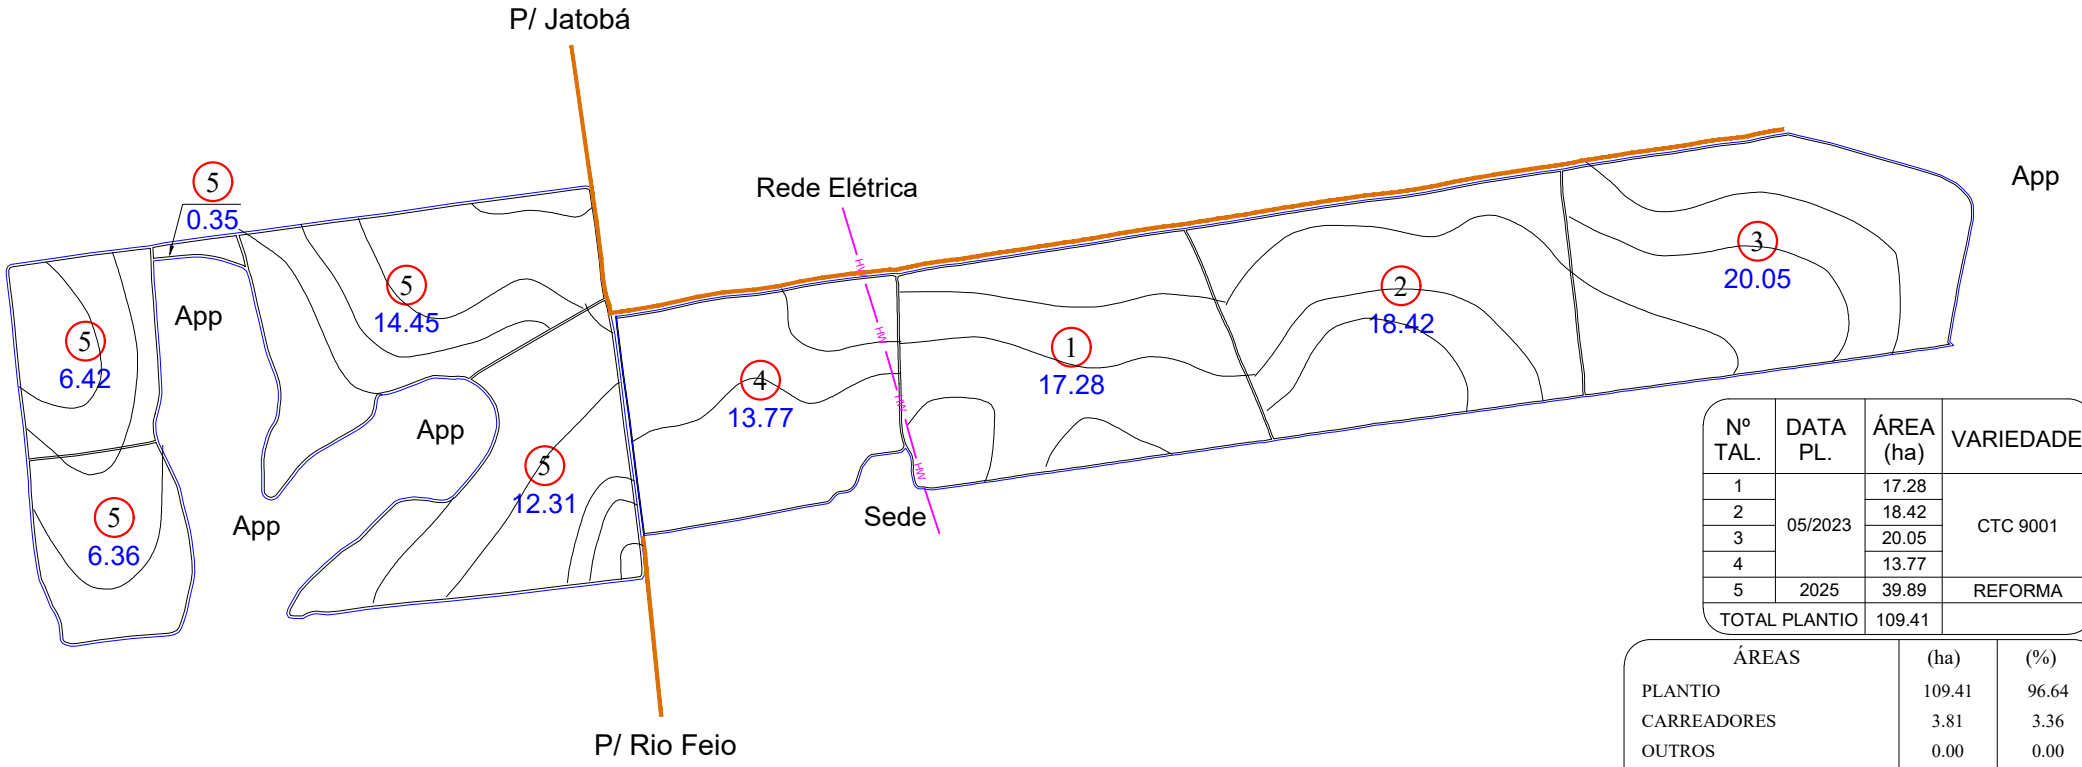

Nº TAL.	DATA PL.	ÁREA (ha)	VARIEDADE
1	05/2023	17.28	CTC 9001
2		18.42	
3		20.05	
4		13.77	
5	2025	39.89	REFORMA
TOTAL PLANTIO		109.41	

ÁREAS	(ha)	(%)
PLANTIO	109.41	96.64
CARREADORES	3.81	3.36
OUTROS	0.00	0.00
SUB TOTAL AGRICULTÁVEL	113.22	100.00
AP.P.	0.00	0.00
ÁRVORES	0.00	0.00
OUTROS	0.00	0.00
SUB TOTAL NÃO AGRICULT.	0.00	0.00
ÁREA TOTAL	113.22	100.00


C. NÍVEL: 9610.89 m/l 2.21 ha 1.95 %

ESCALA: 1: 12.000

LEGENDA
- FAZENDA
- TALHÃO
- REDE ELÉTRICA
- TERRAÇO BASE LARGA
- TERRAÇO EMBUTIDO
- VAZIO
- CARREGADO

ESPAÇAMENTO: 1.50 x 1.50 D.V: 4.51 %
TIRO MÉDIO ESTIMADO: 321.98 m

CROQUI DE ACESSO

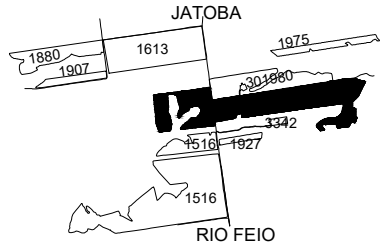

SITIO RIBEIRÃO GRANDE

PROPRIETÁRIO: WILLIAN AVILA PEREIRA
COMPRADOR: CLEALCO
MUNICÍPIO: ALTO ALEGRE - SP

DISTÂNCIAS (km):
UNID. I - Asfalto: 43.00 Terra.: 5.00
UNID.I I - Asfalto: 31.00 Terra.: 4.70

COORDENADAS: E(X): 578906.39 N(Y): 7603812.41
LAT: -21°40'1.9940" LONG: -50°14'14.4264"
CLEALCO - AÇÚCAR E ALCOOL S/A - DEPARTAMENTO DE GEOTECNOLOGIA

LEVANTAMENTO VIA:
- SATÉLITE
- GPS / VANT
- GOOGLE

UNIDADE: I
PARTE: A/A
FUNDO AGRÍCOLA: 305252

M:\01-Mapa de safra\Mapas Atualizados\Terceiro\305252 - Sitio Ribeirao Grande (Willian Avila Pereira)\305252 - Sitio Ribeirao Grande (Willian Avila Pereira).dwg

Bruno Gamboa 10/04/26