
Clealco
Açúcar, Etanol e Energia

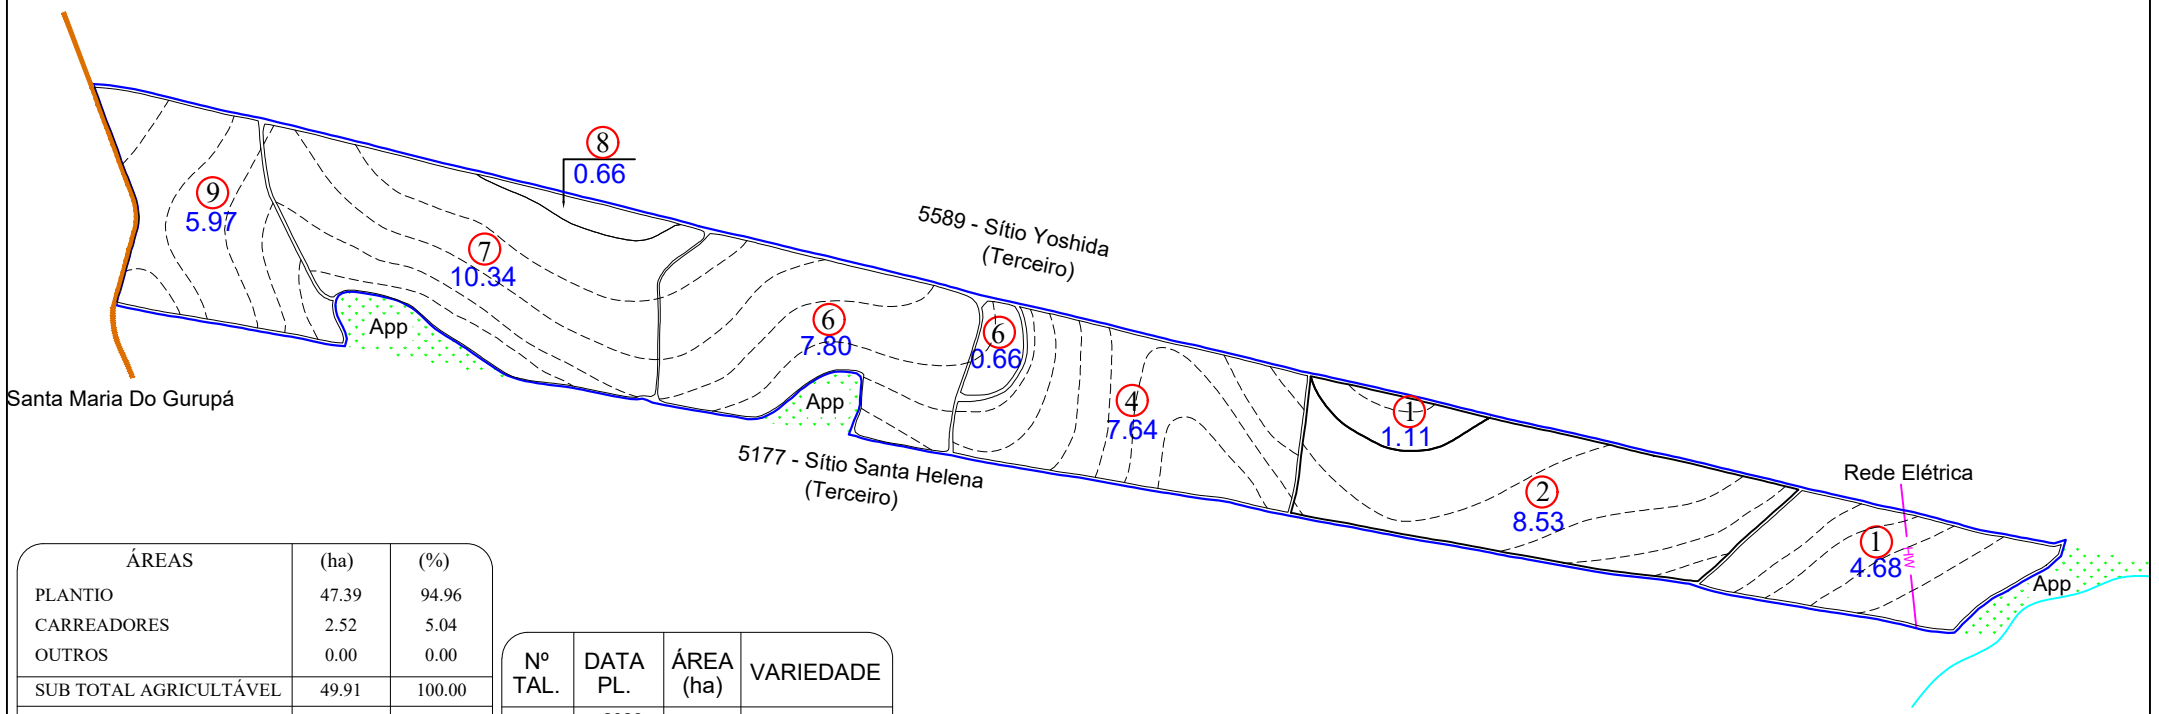

ÁREAS	(ha)	(%)
PLANTIO	47.39	94.96
CARREADORES	2.52	5.04
OUTROS	0.00	0.00
SUB TOTAL AGRICULTÁVEL	49.91	100.00
AP.P.	0.00	0.00
ÁRVORES	0.00	0.00
OUTROS	0.00	0.00
SUB TOTAL NÃO AGRICULT.	0.00	0.00
ÁREA TOTAL	49.91	100.00

C. NÍVEL: 0.00 m/l 0.00 ha 0.00 %

Nº TAL.	DATA PL.	ÁREA (ha)	VARIEDADE
1	2026	5.79	REFORMA
2	04/2021	8.53	CTC 04
4	04/2019	7.64	
6	05/2023	8.46	RB 975242
7		10.34	
8	04/2020	0.66	CTC 04
9	2026	5.97	REFORMA
TOTAL PLANTIO		47.39	


ESCALA: 1: 10.000

LEGENDA

- FAZENDA
- TALHÃO
- REDE ELÉTRICA
- TERRAÇO BASE LARGA
- TERRAÇO EMBUTIDO

ESPAÇAMENTO: 1.50 x 1.50
TIRO MÉDIO ESTIMADO: 000.00 m
D.V: 0.00 %

CROQUI DE ACESSO

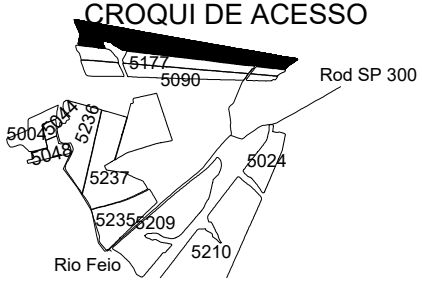

SÍTIO SANTA HELENA

PROPRIETÁRIO: JOSÉ CARLOS D. GILBEIRO
COMPRADOR: CLEALCO
MUNICÍPIO: PROMISSÃO

DISTÂNCIAS (km):
UNID. I - Asfalto: 70.00 Terra.: 0.00
UNID.I I - Asfalto: 48.00 Terra.: 7.00

COORDENADAS: E(X): 598456.15 N(Y): 7612290.22
LAT: -21°35'22.7718" LONG: -50°2'56.0553"

CLEALCO - AÇÚCAR E ALCOOL S/A - DEPARTAMENTO DE GEOTECNOLOGIA

LEVANTAMENTO VIA:
SATÉLITE
GPS / VANT
GOOGLE

UNIDADE: II
PARTE: A/A
FUNDO AGRÍCOLA: 305419

M:\01-Mapa de safra\Mapas Atualizados\Terceiro\305419 - Sítio Santa Helena (José Carlos Donisete Gilberto)\305419 - Sítio Santa Helena (José Carlos Donisete Gilberto).dwg

Benati 09/03/2026