ZONA DV	Nº TAL.	DATA PL.	ÁREA (ha)	VARIEDADE
999	1	04/2021	13.12	CTC 04
7.81%	2		2.46	
TOTAL PLANTIO			15.58	--------

ÁREAS	(ha)	(%)
PLANTIO	15.58	94.48
CARREADORES	0.91	5.52
OUTROS	0.00	0.00
SUB TOTAL AGRICULTÁVEL	16.49	100.00
AP.P.	0.00	0.00
ÁRVORES	0.00	0.00
OUTROS	0.00	0.00
SUB TOTAL NÃO AGRICULT.	0.00	0.00
ÁREA TOTAL	16.49	100.00


C. NÍVEL: 0.00 m/l 0.00 ha 0.00 %

LEGENDA

- FAZENDA
- TALHÃO
- CURVA DE NÍVEL
- CARREADOR
- CONFRONTANTE
- REDE ELÉTRICA
- TRAJETO VAZIO
- TRAJETO CARREGADO


PLANTIO MANUAL - ESPAÇAMENTO: 1.50 X 1.50
TIRO MÉDIO ESTIMADO: 186.83m

Clealco
Açúcar, Etanol e Energia

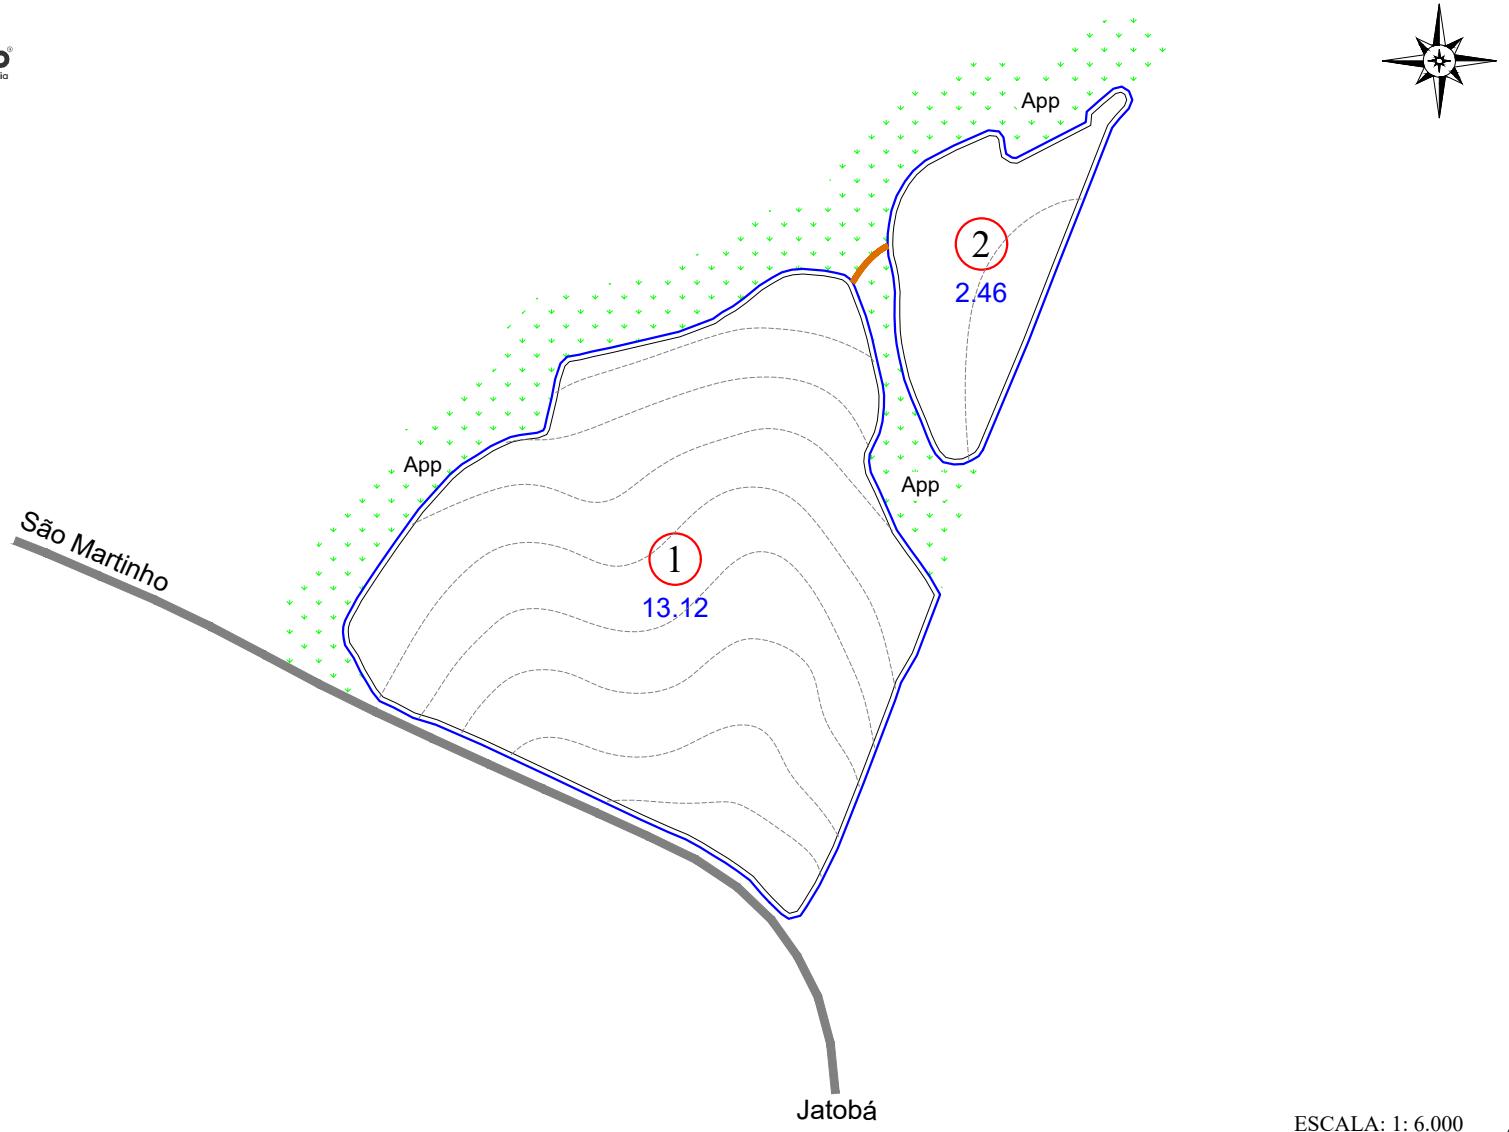

ESCALA: 1: 6.000

CROQUI DE ACESSO

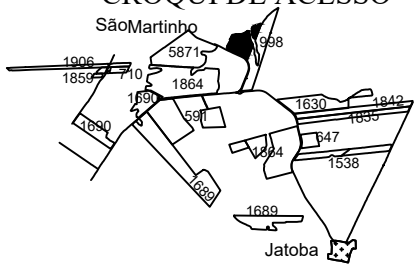

SÍTIO SÃO JOSÉ

PROPRIETÁRIO: JOSE DIAS FULANETI
COMPRADOR: CLEALCO S/A
MUNICÍPIO: ALTO ALEGRE

DISTÂNCIAS (km):
UNID. I - Asfalto: 32.50 Terra.: 00.00
UNID.I I - Asfalto: 40.00 Terra.: 00.00
UNID. III -Asfalto: 32.00 Terra.: 00.00

COORDENADAS: E(X): 576896.92 N(Y): 7612295.74
LAT: -21°35'26.4066" LONG: -50°15'25.7528"

CLEALCO - AÇÚCAR E ALCOOL S/A - DEPARTAMENTO DE TOPOGRAFIA

UNIDADE: I
PARTE: A/A
FUNDO AGRÍCOLA: 305620

M:\01-Mapa de safra\Mapas Atualizados\Terceiro\305620 - Sítio São José (José Dias Fulaneti e Outro)\305620 - Sítio São José (José Dias Fulaneti e Outro).dwg

Fernanda Bezerra 16/03/22