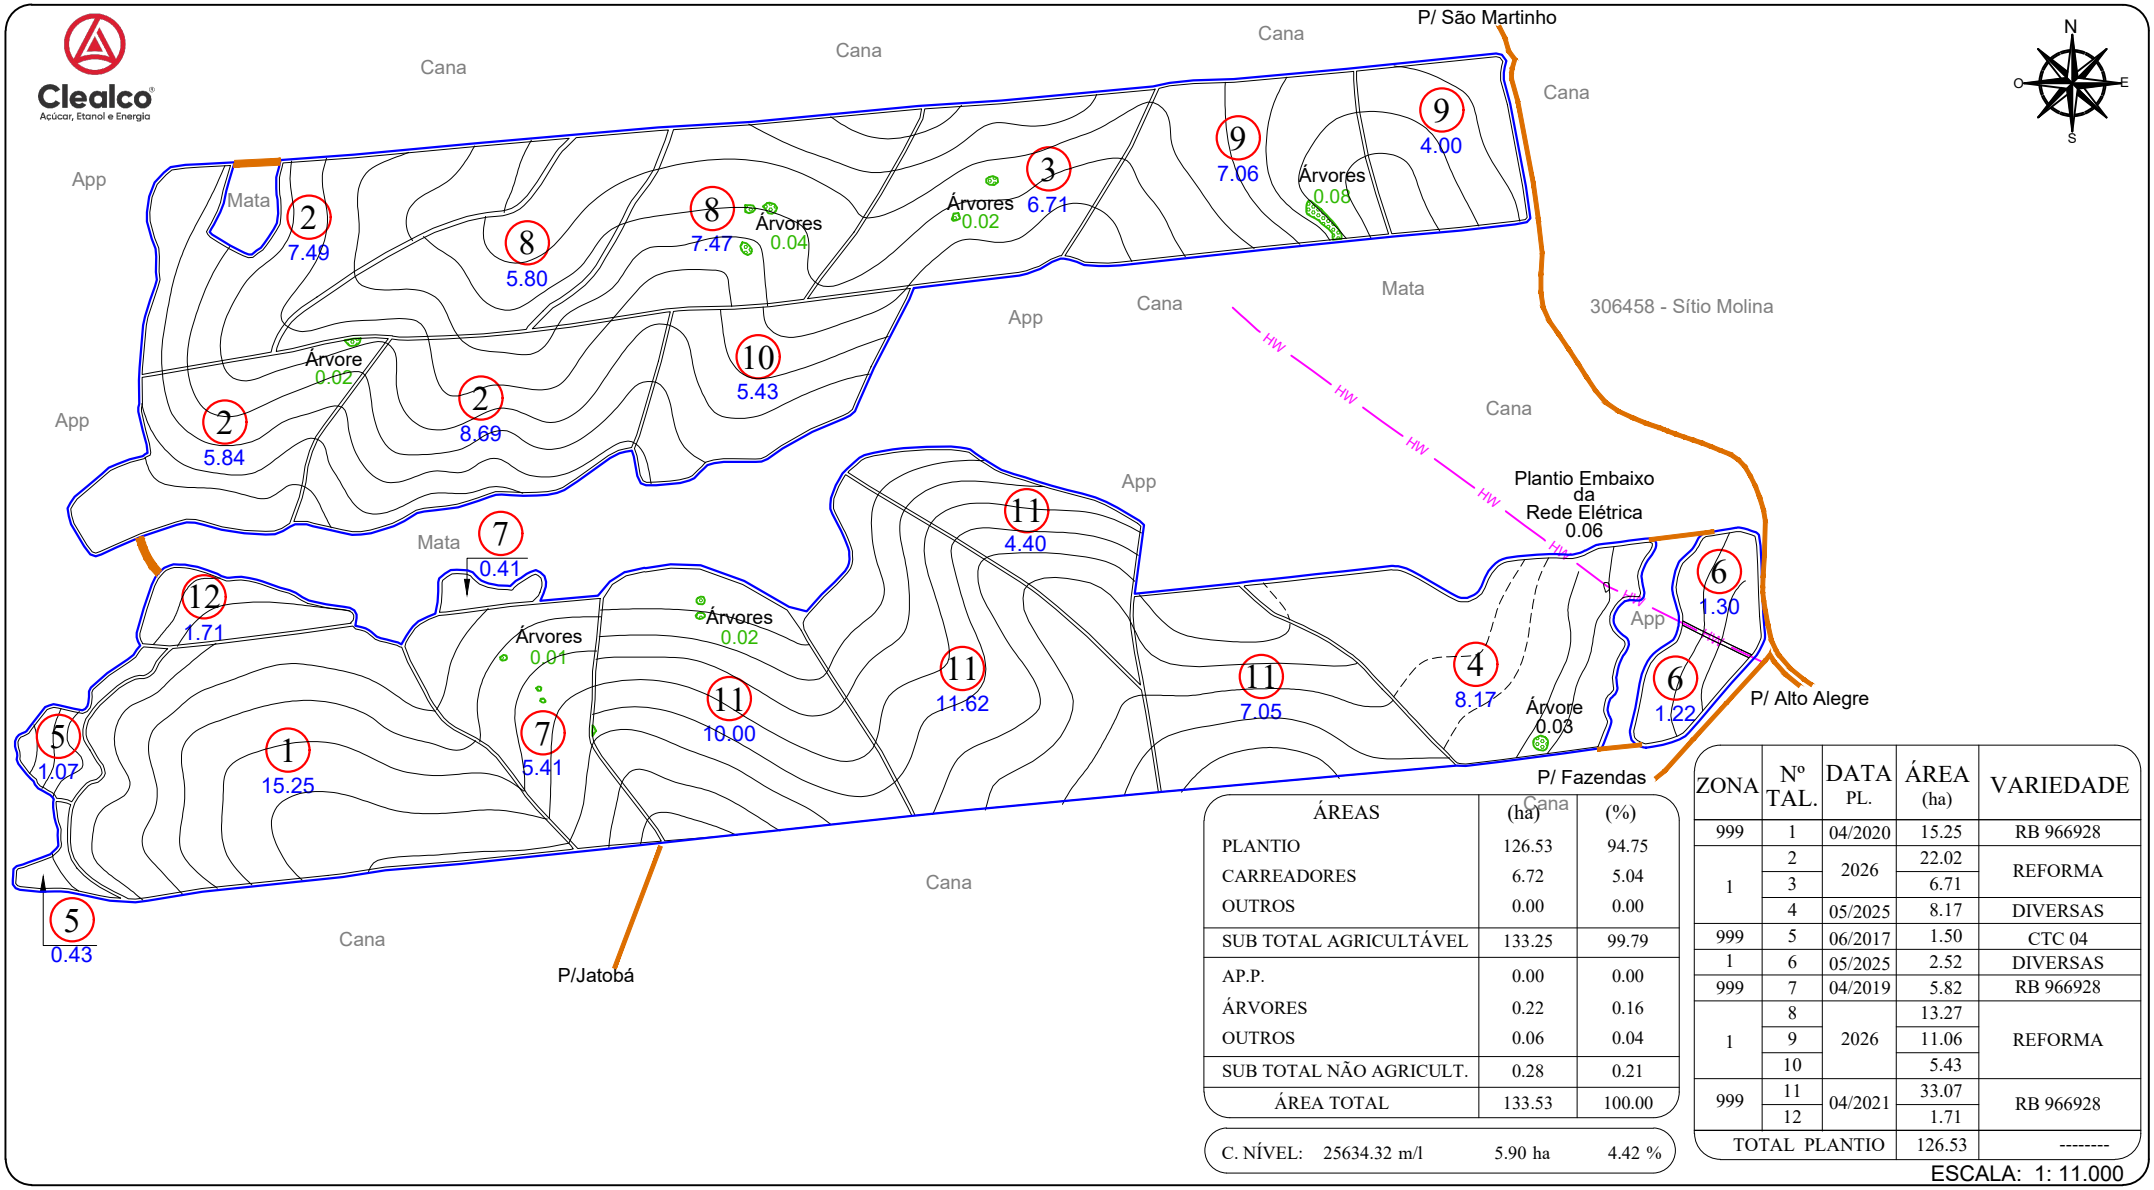


ÁREAS	(ha)	(%)
PLANTIO	126.53	94.75
CARREADORES	6.72	5.04
OUTROS	0.00	0.00
SUB TOTAL AGRICULTÁVEL	133.25	99.79
AP.P.	0.00	0.00
ÁRVORES	0.22	0.16
OUTROS	0.06	0.04
SUB TOTAL NÃO AGRICULT.	0.28	0.21
ÁREA TOTAL	133.53	100.00

C. NÍVEL: 25634.32 m/l 5.90 ha 4.42 %

ZONA	Nº TAL.	DATA PL.	ÁREA (ha)	VARIEDADE
999	1	04/2020	15.25	RB 966928
1	2	2026	22.02	REFORMA
	3		6.71	
	4	05/2025	8.17	DIVERSAS
999	5	06/2017	1.50	CTC 04
1	6	05/2025	2.52	DIVERSAS
999	7	04/2019	5.82	RB 966928
1	8	2026	13.27	REFORMA
	9		11.06	
	10		5.43	
999	11	04/2021	33.07	RB 966928
	12		1.71	
TOTAL PLANTIO			126.53	--------


ESCALA: 1: 11.000

LEGENDA

- FAZENDA
- TALHÃO
- REDE ELÉTRICA
- TERRAÇO BASE LARGA
- TERRAÇO EMBUTIDO

ESPAÇAMENTO: 1.50 x 1.50
TIRO MÉDIO ESTIMADO: 194.05 m
D.V: 5.55 %

CROQUI DE ACESSO

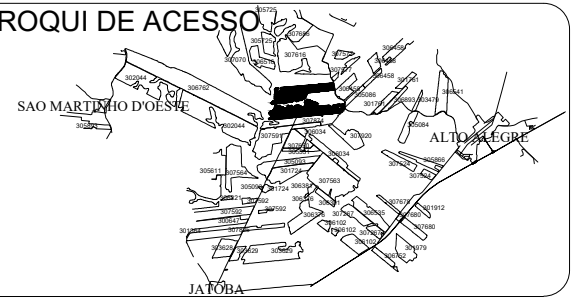

SÍTIO PADRE CLARO

PROPRIETÁRIO: JULIO CESAR DAS NEVES
COMPRADOR: CLEALCO
MUNICÍPIO: ALTO ALEGRE - SP

DISTÂNCIAS (km):
UNID. I - Asfalto: 61.00 Terra.: 7.00
UNID.I I - Asfalto: 34.00 Terra.: 6.00

COORDENADAS: E(X): 581068.95 N(Y): 7613850.71
LAT: -21°34'35.1693" LONG: -50°13'0.9436"
CLEALCO - AÇÚCAR E ALCOOL S/A - DEPARTAMENTO DE GEOTECNOLOGIA

LEVANTAMENTO VIA:
SATÉLITE
GPS / VANT
GOOGLE

UNIDADE: I
PARTE: A/A
FUNDO AGRÍCOLA: 305723

M:\01-Mapa de safra\Mapas Atualizados\Terceiro\305723 - Sítio Padre Claro (Julio Cesar das Neves)\305723 - Sítio Padre Claro (Julio Cesar das Neves).dwg

Bruno Gamboa 24/07/25