ZONA DV	Nº TAL.	DATA PL.	ÁREA (ha)	VARIEDADE
999 5.95 %	1	04/2021	27.21	CTC 04
	2		19.87	
TOTAL PLANTIO			47.08	--------


ÁREAS	(ha)	(%)
PLANTIO	47.08	94.39
CARREADORES	2.64	5.29
OUTROS	0.00	0.00
SUB TOTAL AGRICULTÁVEL	49.72	99.68
AP.P.	0.00	0.00
ÁRVORES	0.16	0.32
OUTROS	0.00	0.00
SUB TOTAL NÃO AGRICULT.	0.16	0.32
ÁREA TOTAL	49.88	100.00

C. NÍVEL: 0.00 m/l 0.00 ha 0.00 %


LEGENDA

- FAZENDA
- TALHÃO
- CURVA DE NÍVEL
- CARREADOR
- CONFRONTANTE
- REDE ELÉTRICA
- TRAJETO VAZIO
- TRAJETO CARREGADO

PLANTIO MANUAL - ESPAÇAMENTO: 1.50 X 1.50
TIRO MÉDIO ESTIMADO: 204.06 m

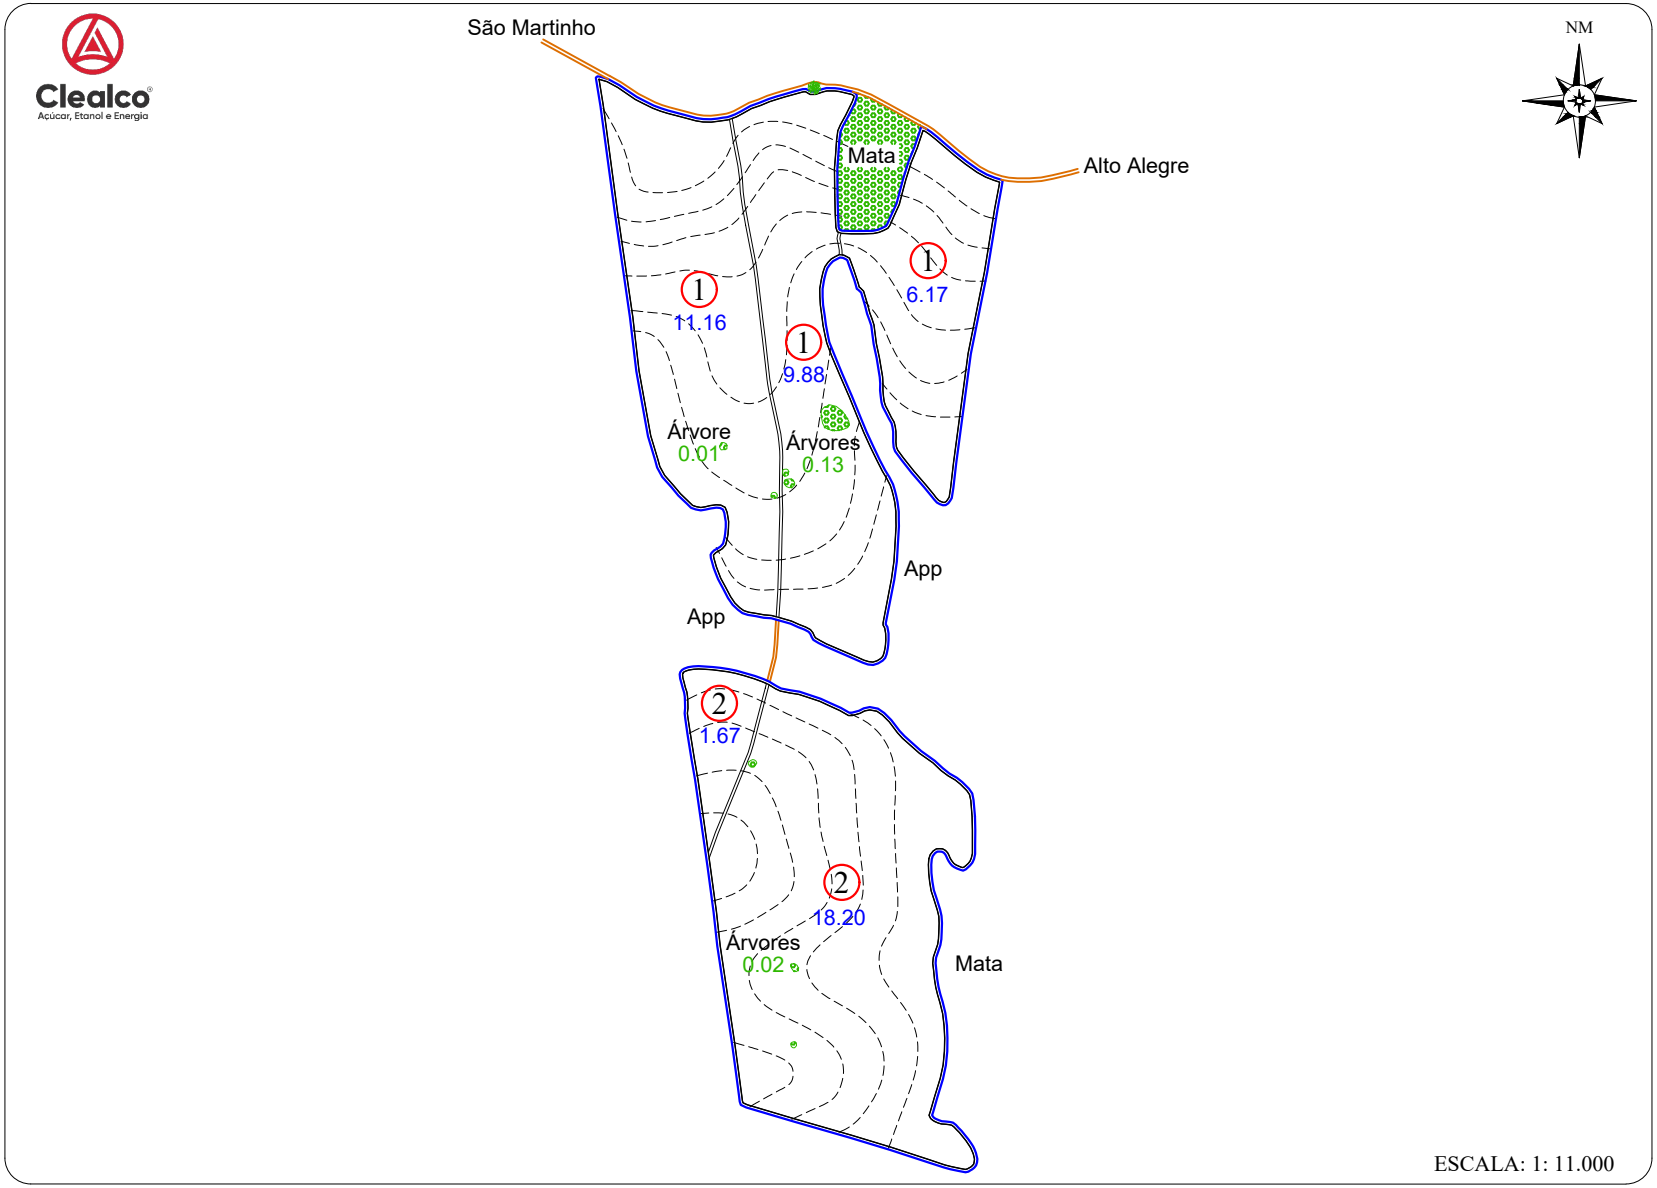

CROQUI DE ACESSO

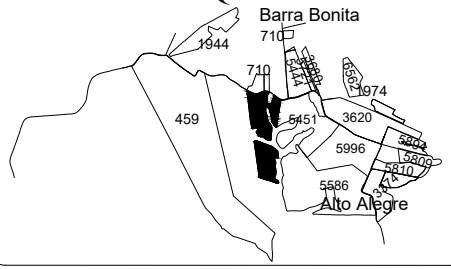

SÍTIO SÃO JOÃO

PROPRIETÁRIO: JULIO CESAR DAS NEVES
COMPRADOR: CLEALCO S/A
MUNICÍPIO: ALTO ALEGRE

DISTÂNCIAS (km):
UNID. I - Asfalto: 32.00 Terra.: 10.50
UNID.I I - Asfalto: 40.00 Terra.: 7.20
UNID. III -Asfalto: 16.00 Terra.: 7.00

COORDENADAS: E(X): 580000 N(Y): 7616000
LAT: 21° 33' 25,44115" LONG: 50° 13' 38,48278"

CLEALCO - AÇÚCAR E ALCOOL S/A - DEPARTAMENTO DE TOPOGRAFIA

UNIDADE: I
PARTE: A/A
FUNDO AGRÍCOLA: 305725

M:\01-Mapa de safra\Mapas Atualizados\Terceiro\305725 - Sítio São João (Juio Cesar das Neves)\305725 - Sítio São João (Juio Cesar das Neves).dwg

Fernanda Bezerra 02/02/22