ZONA DV	CLA	Nº TAL.	DATA PL.	ÁREA (ha)	VAR.
999		119	05/2019	4.50	DIVERSAS
TOTAL PLANTIO				4.54	--------

ÁREAS	(ha)	(%)
PLANTIO	4.54	92.21
CARREADORES	0.38	7.79
OUTROS	0.00	0.00
SUB TOTAL AGRICULTÁVEL	4.92	100.00
AP.P.	0.00	0.00
ÁRVORES	0.00	0.00
OUTROS	0.00	0.00
SUB TOTAL NÃO AGRICULT.	0.00	0.00
ÁREA TOTAL	4.92	100.00

C. NÍVEL: 0.00 m/l 0.00 ha 0.00 %

LEGENDA


- FAZENDA
- TALHÃO
- CURVA DE NÍVEL
- CARREADOR
- CONFRONTANTE
- REDE ELÉTRICA
- TRAJETO VAZIO
- TRAJETO CARREGADO

TIPO DE PLANTIO: CONVENCIONAL: 0.00 ha

ESPAÇAMENTO: 0.00 MECANIZADO: 0.00 ha


Clealco
Açúcar, Etanol e Energia

NM

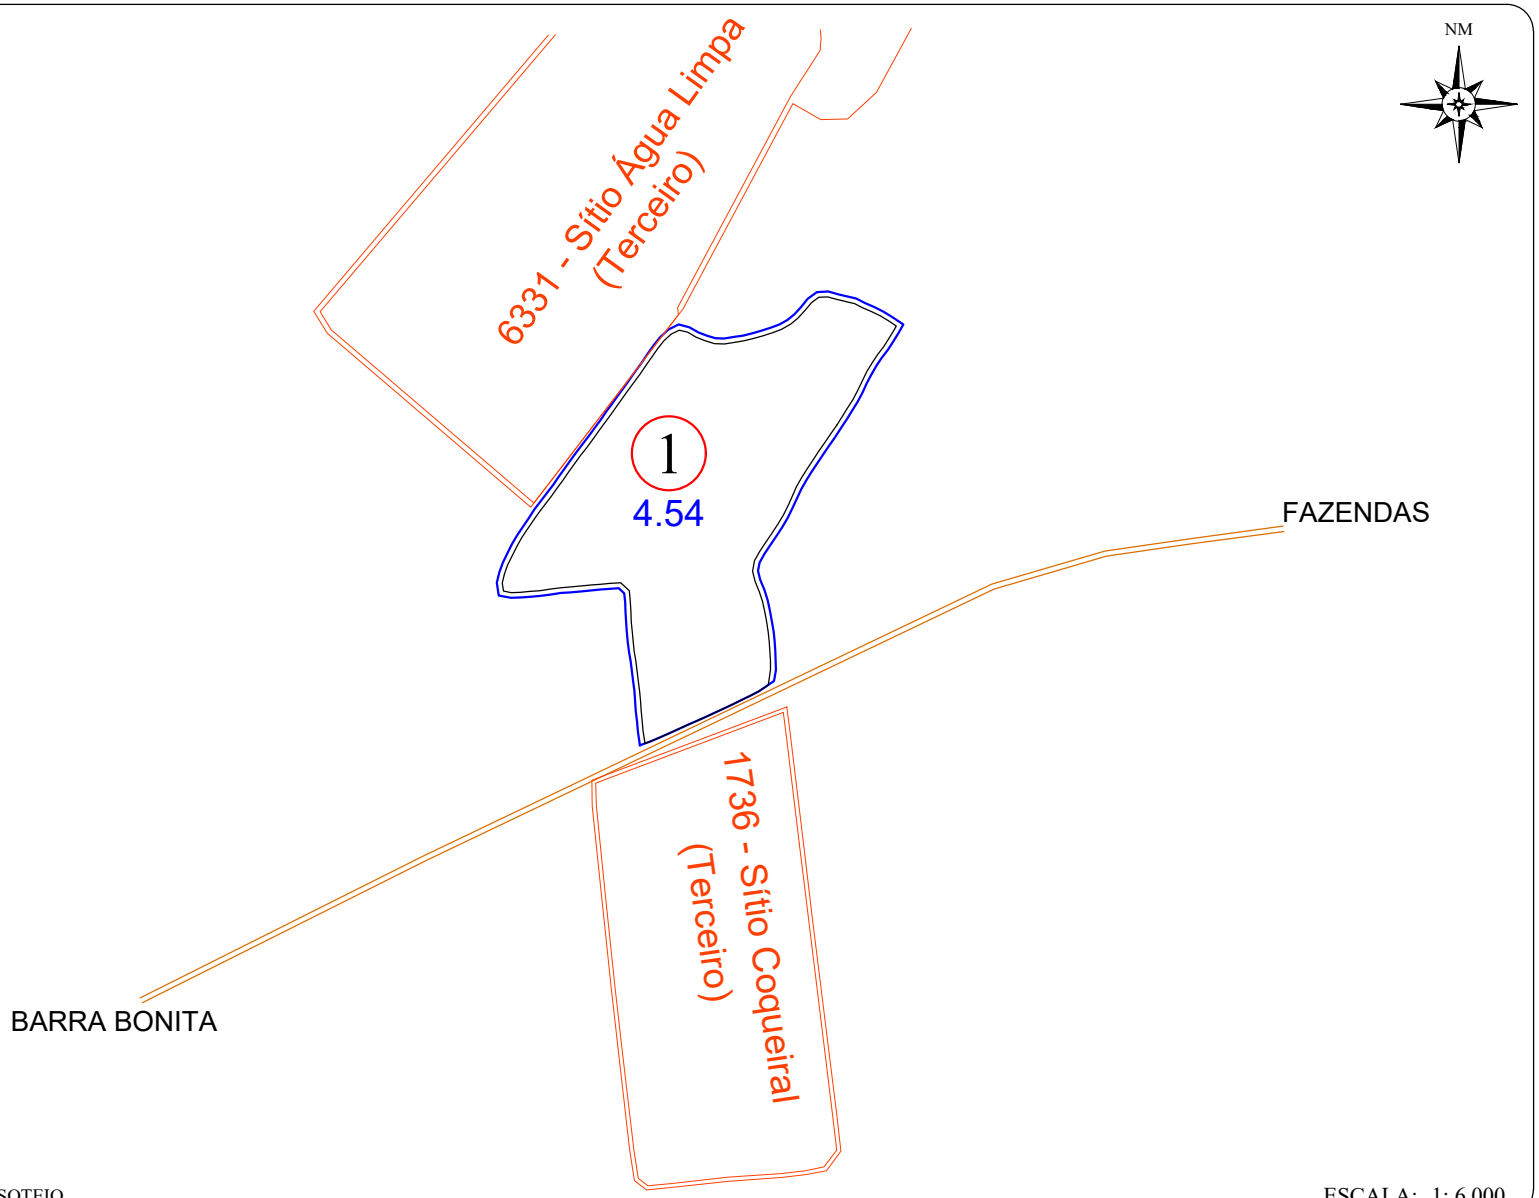

ESCALA: 1: 6.000

CROQUI DE ACESSO

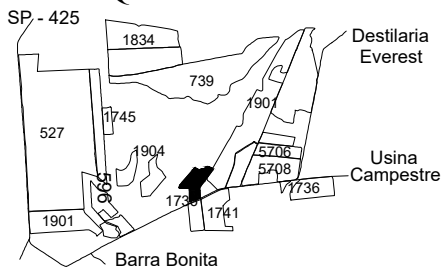

SÍTIO BELA VISTA

PROPRIETÁRIO: CARLOS S. SCARDOVELLI
COMPRADOR: CLEALCO S/A
MUNICÍPIO: PENÁPOLIS

DISTÂNCIAS (km):
UNID. I - Asfalto: 34.00 Terra.: 00.00
UNID.I I - Asfalto: 68.00 Terra.: 00.00
UNID. III -Asfalto: 00.00 Terra.: 13.00

COORDENADAS: E(X): 581974 N(Y): 7620533
LAT: 21° 30' 57,69169" LONG: 50° 12' 30,65299"

CLEALCO - AÇÚCAR E ALCOOL S/A - DEPARTAMENTO DE TOPOGRAFIA

UNIDADE: I

PARTE: A/A

FUNDO AGRÍCOLA: 305815