| ZONA D.V. | Nº TAL. | DATA PL. | ÁREA (ha) | VARIEDADE |
|---|---|---|---|---|
| 999 | 1 | 05/2021 | 6.42 | CTC 04 |
| 5.98 % | 2 | | 44.83 | |
| TOTAL PLANTIO | | | 51.25 | -------- |

| ÁREAS | (ha) | (%) |
|---|---|---|
| PLANTIO | 51.25 | 95.85 |
| CARREADORES | 2.22 | 4.15 |
| OUTROS | 0.00 | 0.00 |
| SUB TOTAL AGRICULTÁVEL | 53.47 | 100.00 |
| AP.P. | 0.00 | 0.00 |
| ÁRVORES | 0.00 | 0.00 |
| OUTROS | 0.00 | 0.00 |
| SUB TOTAL NÃO AGRICULT. | 0.00 | 0.00 |
| ÁREA TOTAL | 53.47 | 100.00 |

| | | | |
|---|---|---|---|
| C. NÍVEL: | 9550.41 m/l | 2.20 ha | 4.11 % |

LEGENDA

| | |
|---|---|
| ▬ FAZENDA | ▬ CONFRONTANTE |
| ▬ TALHÃO | -·- REDE ELÉTRICA |
| ▪▪▪ CURVA DE NÍVEL | —▷ TRAJETO VAZIO |
| — CARREADOR | —► TRAJETO CARREGADO |

PLANTIO MANUAL - ESPAÇAMENTO: 1.50 X 1.50
TIRO MÉDIO ESTIMADO: 217.40 m

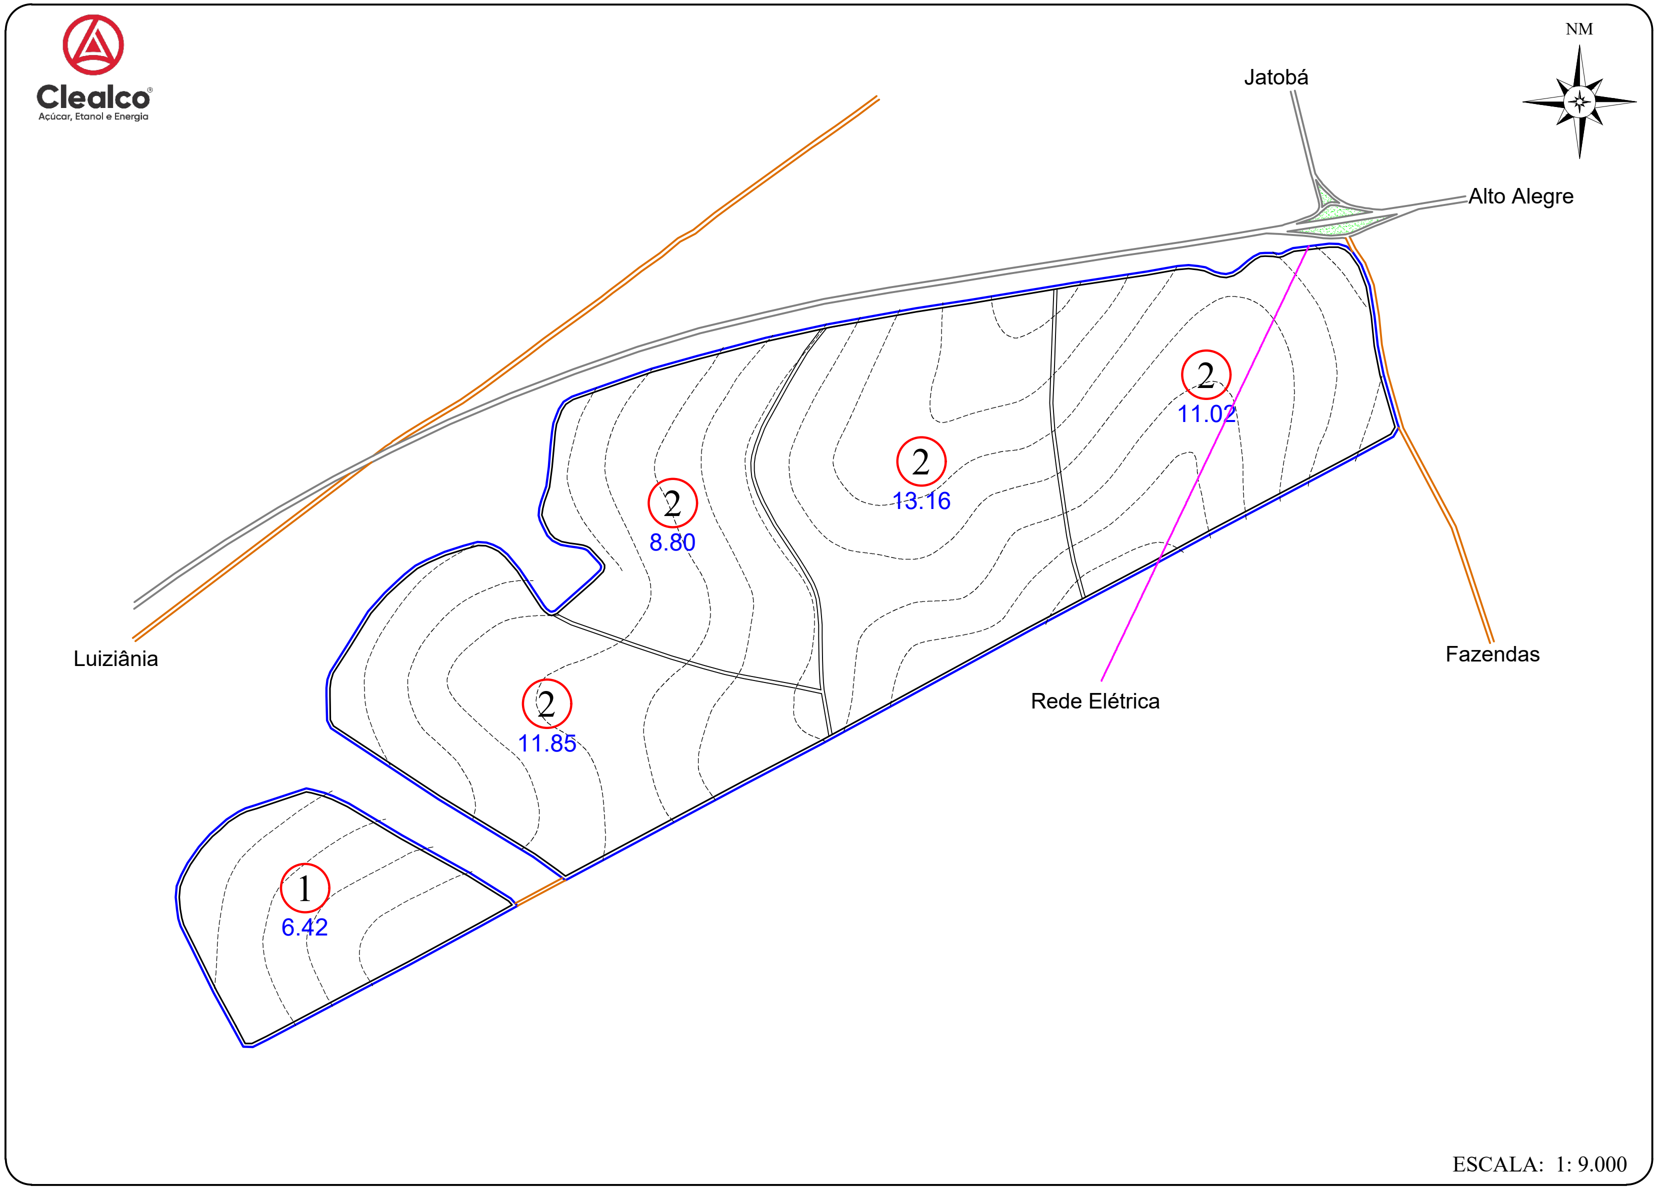

ESCALA: 1: 9.000

## CROQUI DE ACESSO

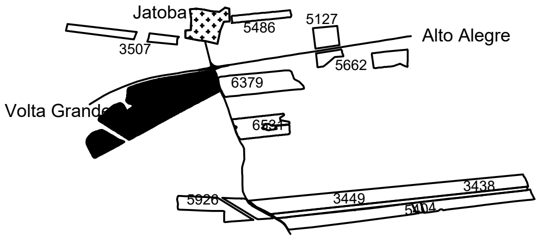

# SÍTIO BOA VISTA

PROPRIETÁRIO: RAFAEL PONTIN E OUTRO
COMPRADOR: CLEALCO S/A
MUNICÍPIO: ALTO ALEGRE

DISTÂNCIAS (km):

| | | | | |
|---|---|---|---|---|
| UNID. I - | Asfalto: | 42.80 | Terra.: | 1.50 |
| UNID.I I - | Asfalto: | 31.00 | Terra.: | 1.50 |
| UNID. III - | Asfalto: | 25.00 | Terra.: | 0.80 |

COORDENADAS: E(X): 577273.43 N(Y): 7607262.88
LAT: -21°38'10.0327" LONG: -50°15'11.8193"

CLEALCO - AÇÚCAR E ALCOOL S/A - DEPARTAMENTO DE TOPOGRAFIA

UNIDADE:
II

PARTE:
A/A

FUNDO AGRÍCOLA:
306032

M:\01-Mapa de safra\Mapas Atualizados\Terceiro\306032 - Sítio Boa Vista (Rafael Pontin)\306032 - Sítio Boa Vista (Rafael Pontin).dwg

Fernanda Bezerra 07/03/24