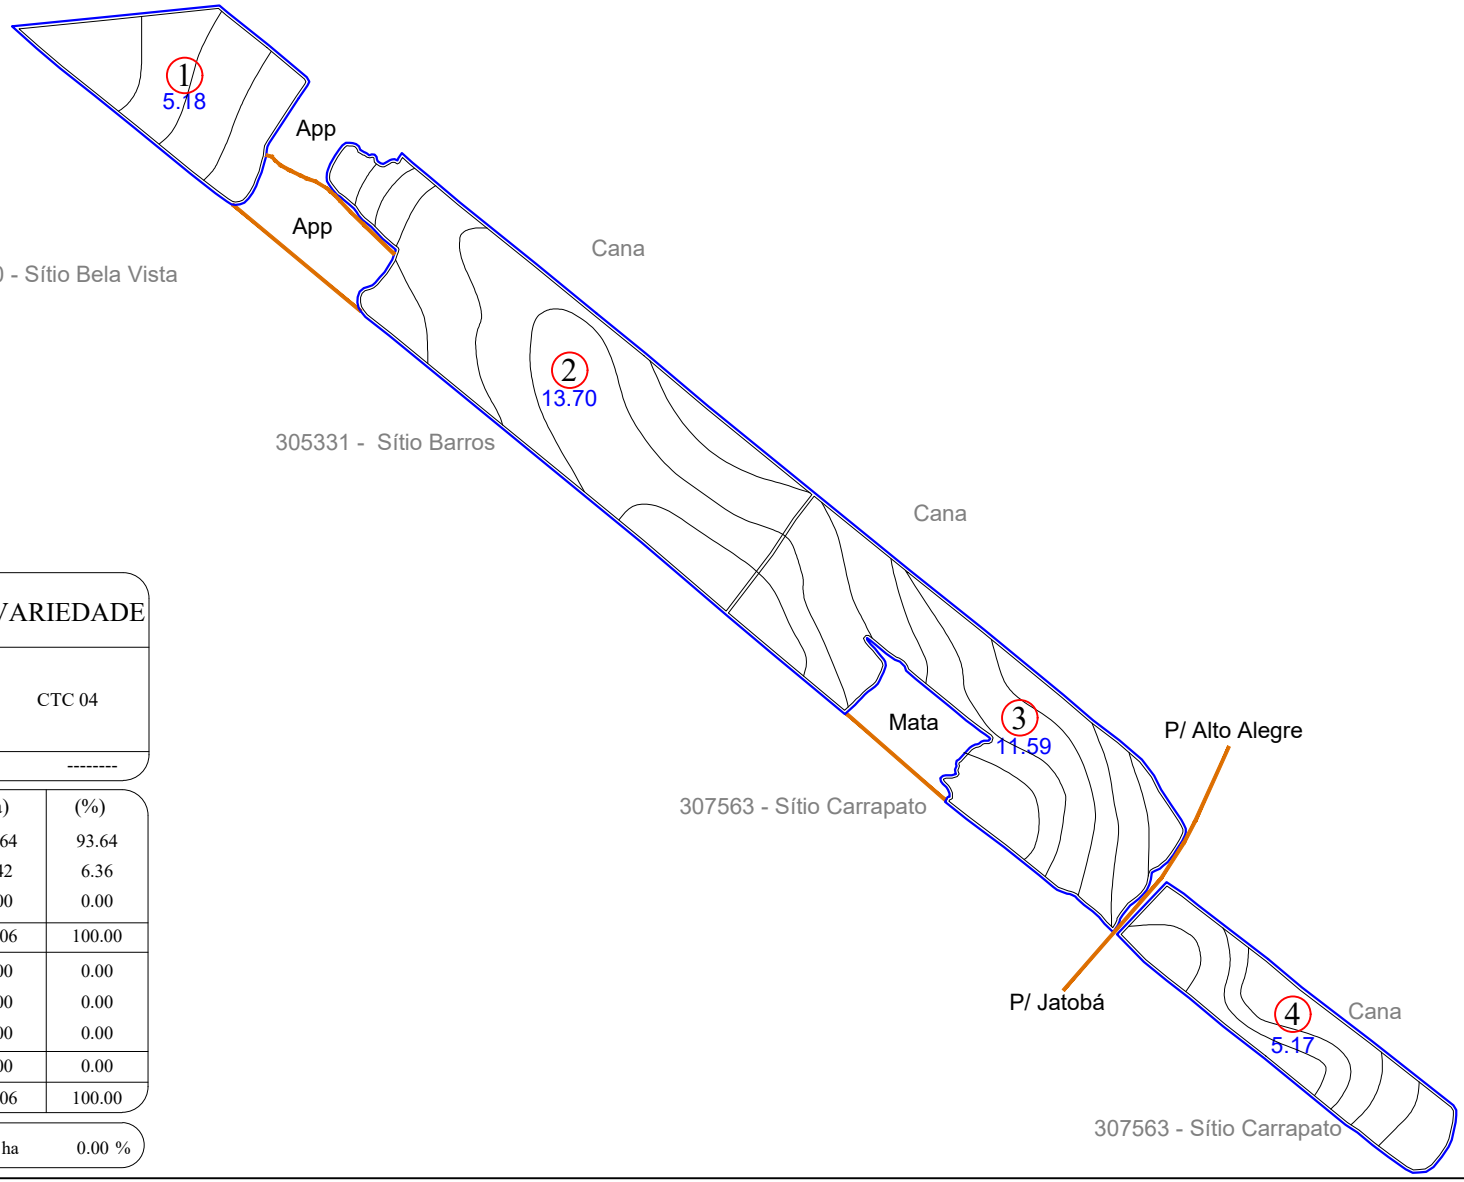


ZONA	Nº TAL.	DATA PL.	ÁREA (ha)	VARIEDADE
999	1	04/2021	5.18	CTC 04
	2		13.70	
	3		11.59	
	4		5.17	
TOTAL PLANTIO			35.64	--------

ÁREAS	(ha)	(%)
PLANTIO	35.64	93.64
CARREADORES	2.42	6.36
OUTROS	0.00	0.00
SUB TOTAL AGRICULTÁVEL	38.06	100.00
AP.P.	0.00	0.00
ÁRVORES	0.00	0.00
OUTROS	0.00	0.00
SUB TOTAL NÃO AGRICULT.	0.00	0.00
ÁREA TOTAL	38.06	100.00

C. NÍVEL: 0.00 m/l 0.00 ha 0.00 %


ESCALA: 1: 10.500

LEGENDA

- FAZENDA
- TALHÃO
- REDE ELÉTRICA
- TERRAÇO BASE LARGA
- TERRAÇO EMBUTIDO

ESPAÇAMENTO: 1.50 x 1.50
TIRO MÉDIO ESTIMADO: 153.39 m
D.V: 5.89 %

CROQUI DE ACESSO

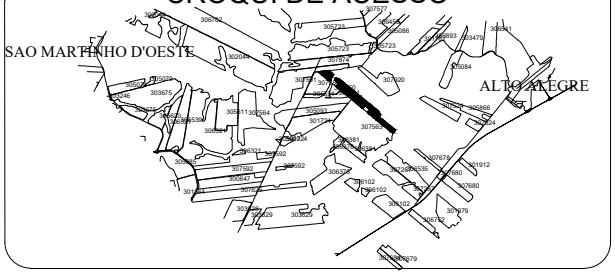

SÍTIO DOIS IRMÃOS

PROPRIETÁRIO: CESAR H. ESPERANCIN CRUZ
COMPRADOR: CLEALCO
MUNICÍPIO: ALTO ALEGRE - SP

DISTÂNCIAS (km):
UNID. I - Asfalto: 47.00 Terra.: 4.00
UNID.I I - Asfalto: 35.00 Terra.: 2.83

COORDENADAS: E(X): 582469.59 N(Y): 7611922.66
LAT: -21°35'37.6442" LONG: -50°12'11.8992"

CLEALCO - AÇÚCAR E ALCOOL S/A - DEPARTAMENTO DE GEOTECNOLOGIA

LEVANTAMENTO VIA:
SATÉLITE
GPS / VANT
GOOGLE

UNIDADE: II
PARTE: A/A
FUNDO AGRÍCOLA: 306034

M:\01-Mapa de safra\Mapas Atualizados\Terceiro\306034 - Sítio Dois Irmãos (Cesar Henrique Esperancin Cruz)\306034 - Sítio Dois Irmãos (Cesar Henrique Esperancin Cruz).dwg

Bruno Gamboa 15/09/25