ZONA DV	Nº TAL.	DATA PL.	ÁREA (ha)	VARIEDADE
999 5.22 %	1	04/2021	17.29	RB 96 6928
TOTAL PLANTIO			17.29	--------

ÁREAS	(ha)	(%)
PLANTIO	17.29	94.83
CARREADORES	0.92	5.06
OUTROS	0.00	0.00
SUB TOTAL AGRICULTÁVEL	18.21	99.89
AP.P.	0.00	0.00
ÁRVORES	0.02	0.11
OUTROS	0.00	0.00
SUB TOTAL NÃO AGRICULT.	0.02	0.11
ÁREA TOTAL	18.23	100.00

C. NÍVEL:	0.00 m/l	0.00 ha	0.00 %

LEGENDA

▬ FAZENDA	▬ CONFRONTANTE
▬ TALHÃO	-·- REDE ELÉTRICA
▪▪▪ CURVA DE NÍVEL	—▷ TRAJETO VAZIO
— CARREADOR	—► TRAJETO CARREGADO

PLANTIO MANUAL - ESPAÇAMENTO: 1.50 X 1.50
TIRO MÉDIO ESTIMADO: 189.63 m

Clealco
Açúcar, Etanol e Energia

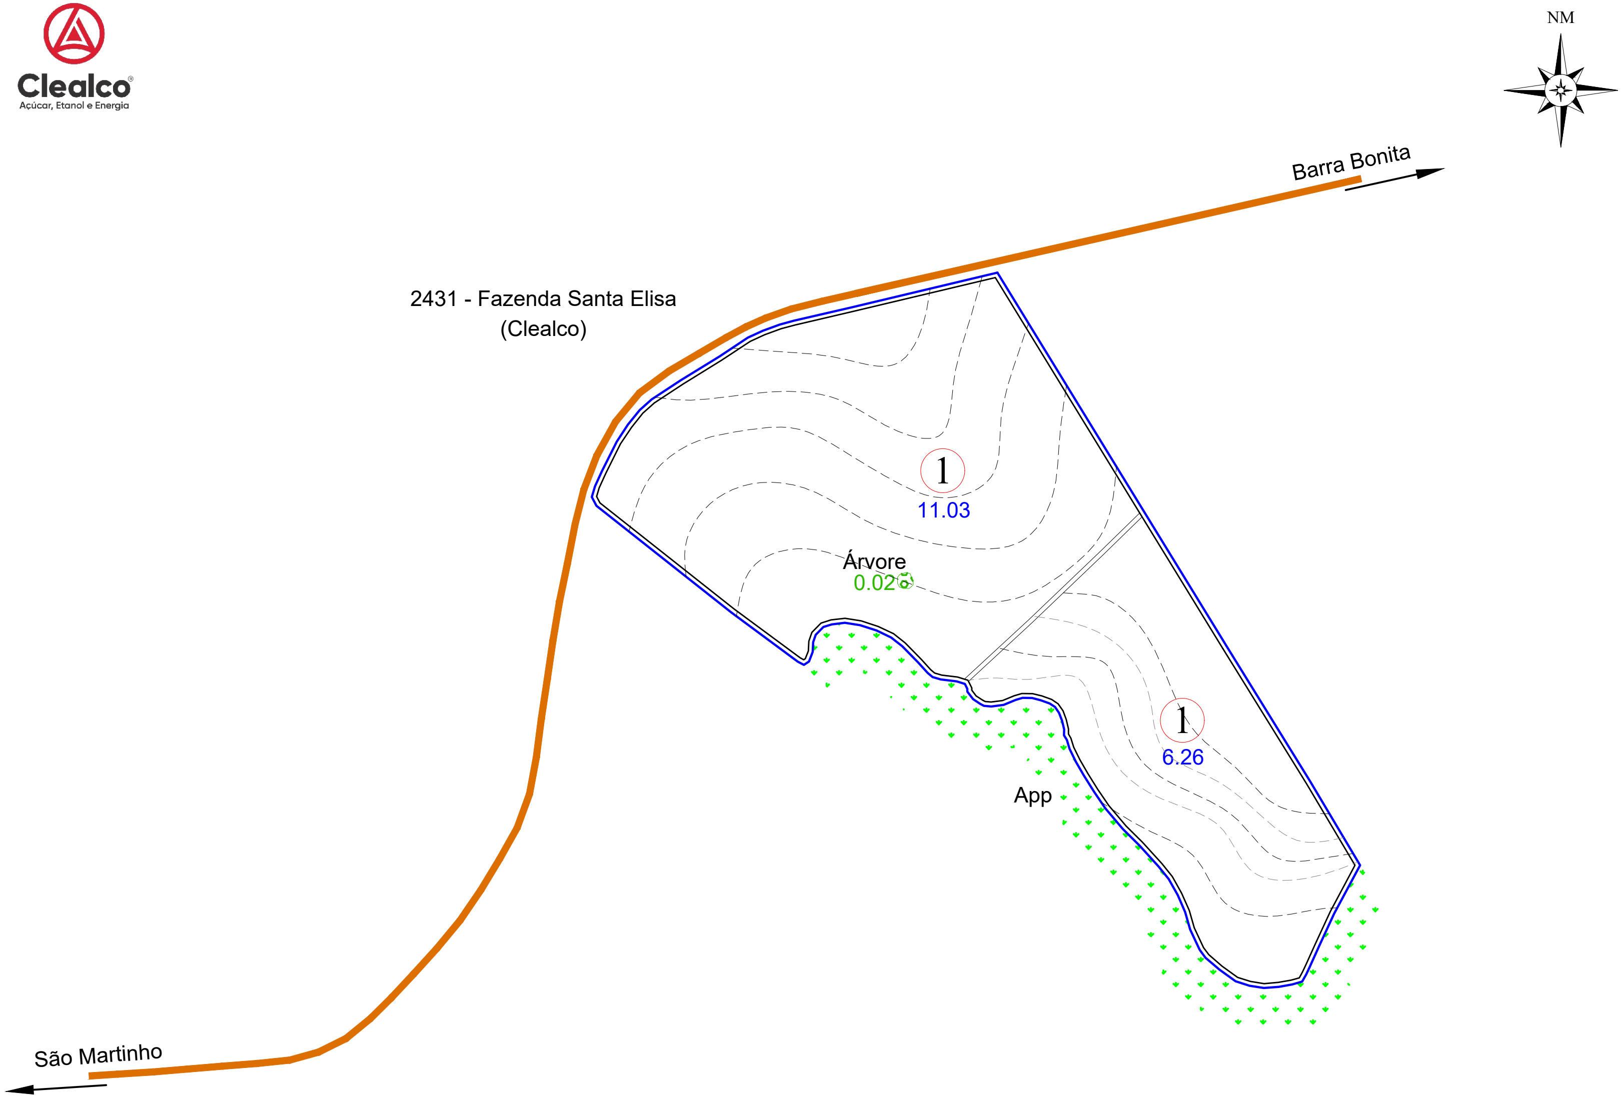

ESCALA: 1: 7.000

CROQUI DE ACESSO

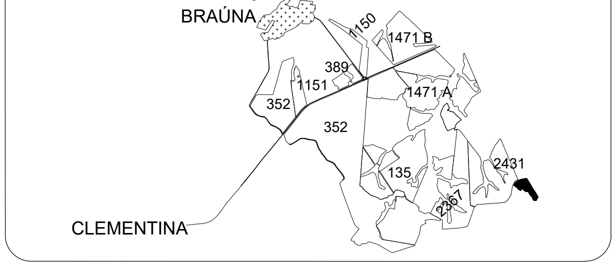

SÍTIO SANTA CRISTINA

PROPRIETÁRIO:	JULIO CESAR DAS NEVES
COMPRADOR:	CLEALCO S/A
MUNICÍPIO:	PENÁPOLIS

DISTÂNCIAS (km):

	Asfalto:		Terra.:
UNID. I -	Asfalto: 20.50		2.00
UNID.I I -	Asfalto: 68.00		2.00
UNID. III -	Asfalto: 26.50		2.00

COORDENADAS:		
E(X): 576719.377	N(Y): 7616906.157
LAT: 21º 32' 56"	LONG: 50º 15' 33"

CLEALCO - AÇÚCAR E ALCOOL S/A - DEPARTAMENTO DE TOPOGRAFIA

UNIDADE:
I

PARTE:
A/A

FUNDO AGRÍCOLA:
306037

M:\01-Mapa de safra\Mapas Atualizados\Terceiro\306037 - Sítio Santa Cristina (Julio Cesar das Neves)\306037 - Sítio Santa Cristina (Julio Cesar das Neves).dwg

Fernanda Bezerra 02/02/22