
Clealco
Açúcar, Etanol e Energia

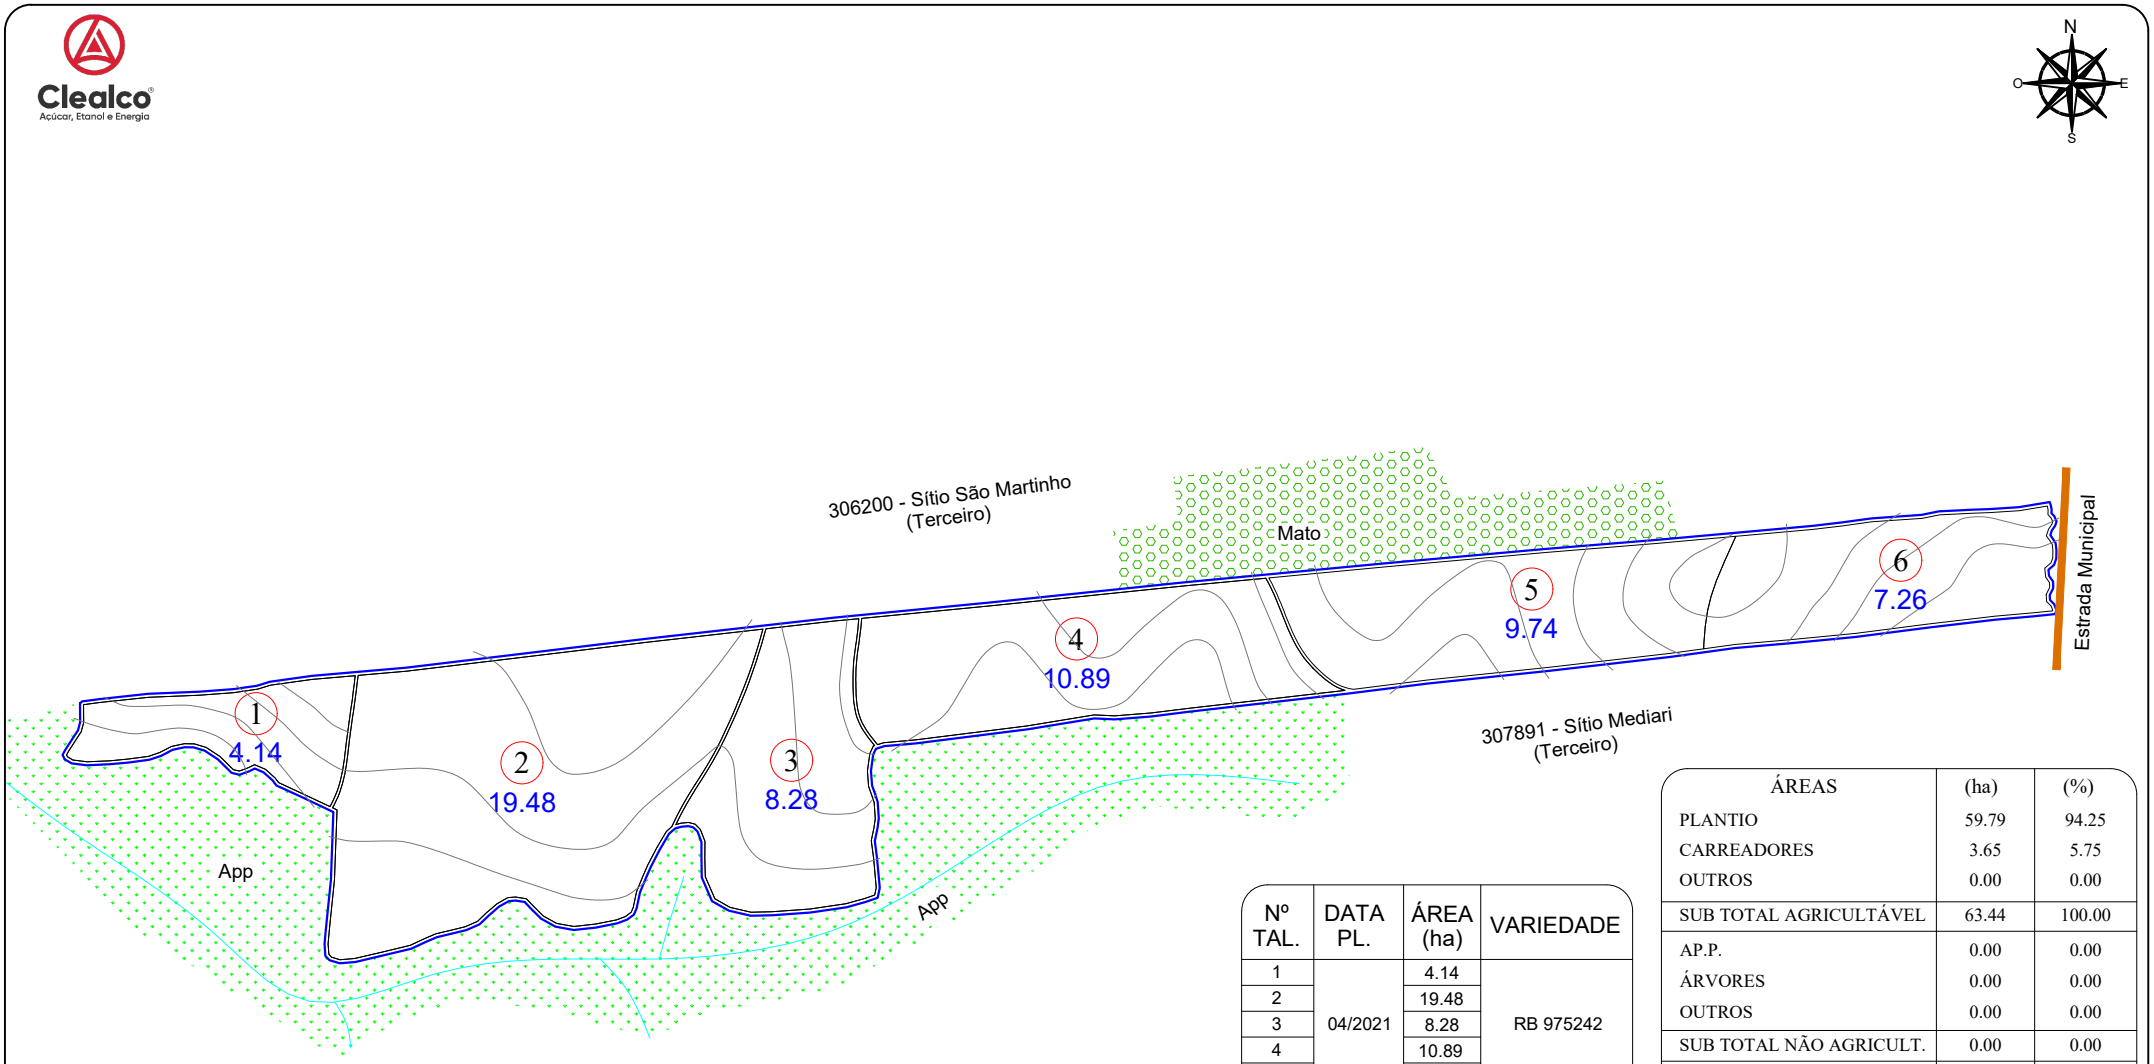

Nº TAL.	DATA PL.	ÁREA (ha)	VARIEDADE
1	04/2021	4.14	RB 975242
2		19.48	
3		8.28	
4		10.89	
5		9.74	
6	2026	7.26	REFORMA
TOTAL PLANTIO		59.79	

ÁREAS	(ha)	(%)
PLANTIO	59.79	94.25
CARREADORES	3.65	5.75
OUTROS	0.00	0.00
SUB TOTAL AGRICULTÁVEL	63.44	100.00
AP.P.	0.00	0.00
ÁRVORES	0.00	0.00
OUTROS	0.00	0.00
SUB TOTAL NÃO AGRICULT.	0.00	0.00
ÁREA TOTAL	63.44	100.00

C. NÍVEL: 0.00 m/l 0.00 ha 0.00 %


ESCALA: 1: 11.000

LEGENDA

- FAZENDA
- TALHÃO
- REDE ELÉTRICA
- TERRAÇO BASE LARGA
- TERRAÇO EMBUTIDO

ESPAÇAMENTO: 1.50 x 1.50
TIRO MÉDIO ESTIMADO: 000.00 m
D.V: 6.00 %

CROQUI DE ACESSO

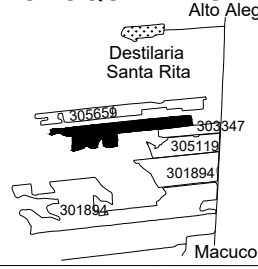

SITIO ALTO ALEGRE

PROPRIETÁRIO: LUIZ CAPUTO
COMPRADOR: CLEALCO
MUNICÍPIO: ALTO ALEGRE - SP

DISTÂNCIAS (km):
UNID. I - Asfalto: 29.50 Terra.: 13.00
UNID.I I - Asfalto: 40.00 Terra.: 5.50

COORDENADAS: E(X): 583624.10 N(Y): 7606377.47
LAT: -21°38'37.7952" LONG: -50°11'30.7487"

CLEALCO - AÇÚCAR E ALCOOL S/A - DEPARTAMENTO DE GEOTECNOLOGIA

LEVANTAMENTO VIA:
SATÉLITE
GPS / VANT
GOOGLE

UNIDADE: II
PARTE: A/A
FUNDO AGRÍCOLA: 306085

M:\01-Mapa de safra\Mapas Atualizados\Terceiro\306085 - Sítio Alto Alegre (Luiz Caputo)\306085 - Sítio Alto Alegre (Luiz Caputo).dwg

Benati 20/02/2026