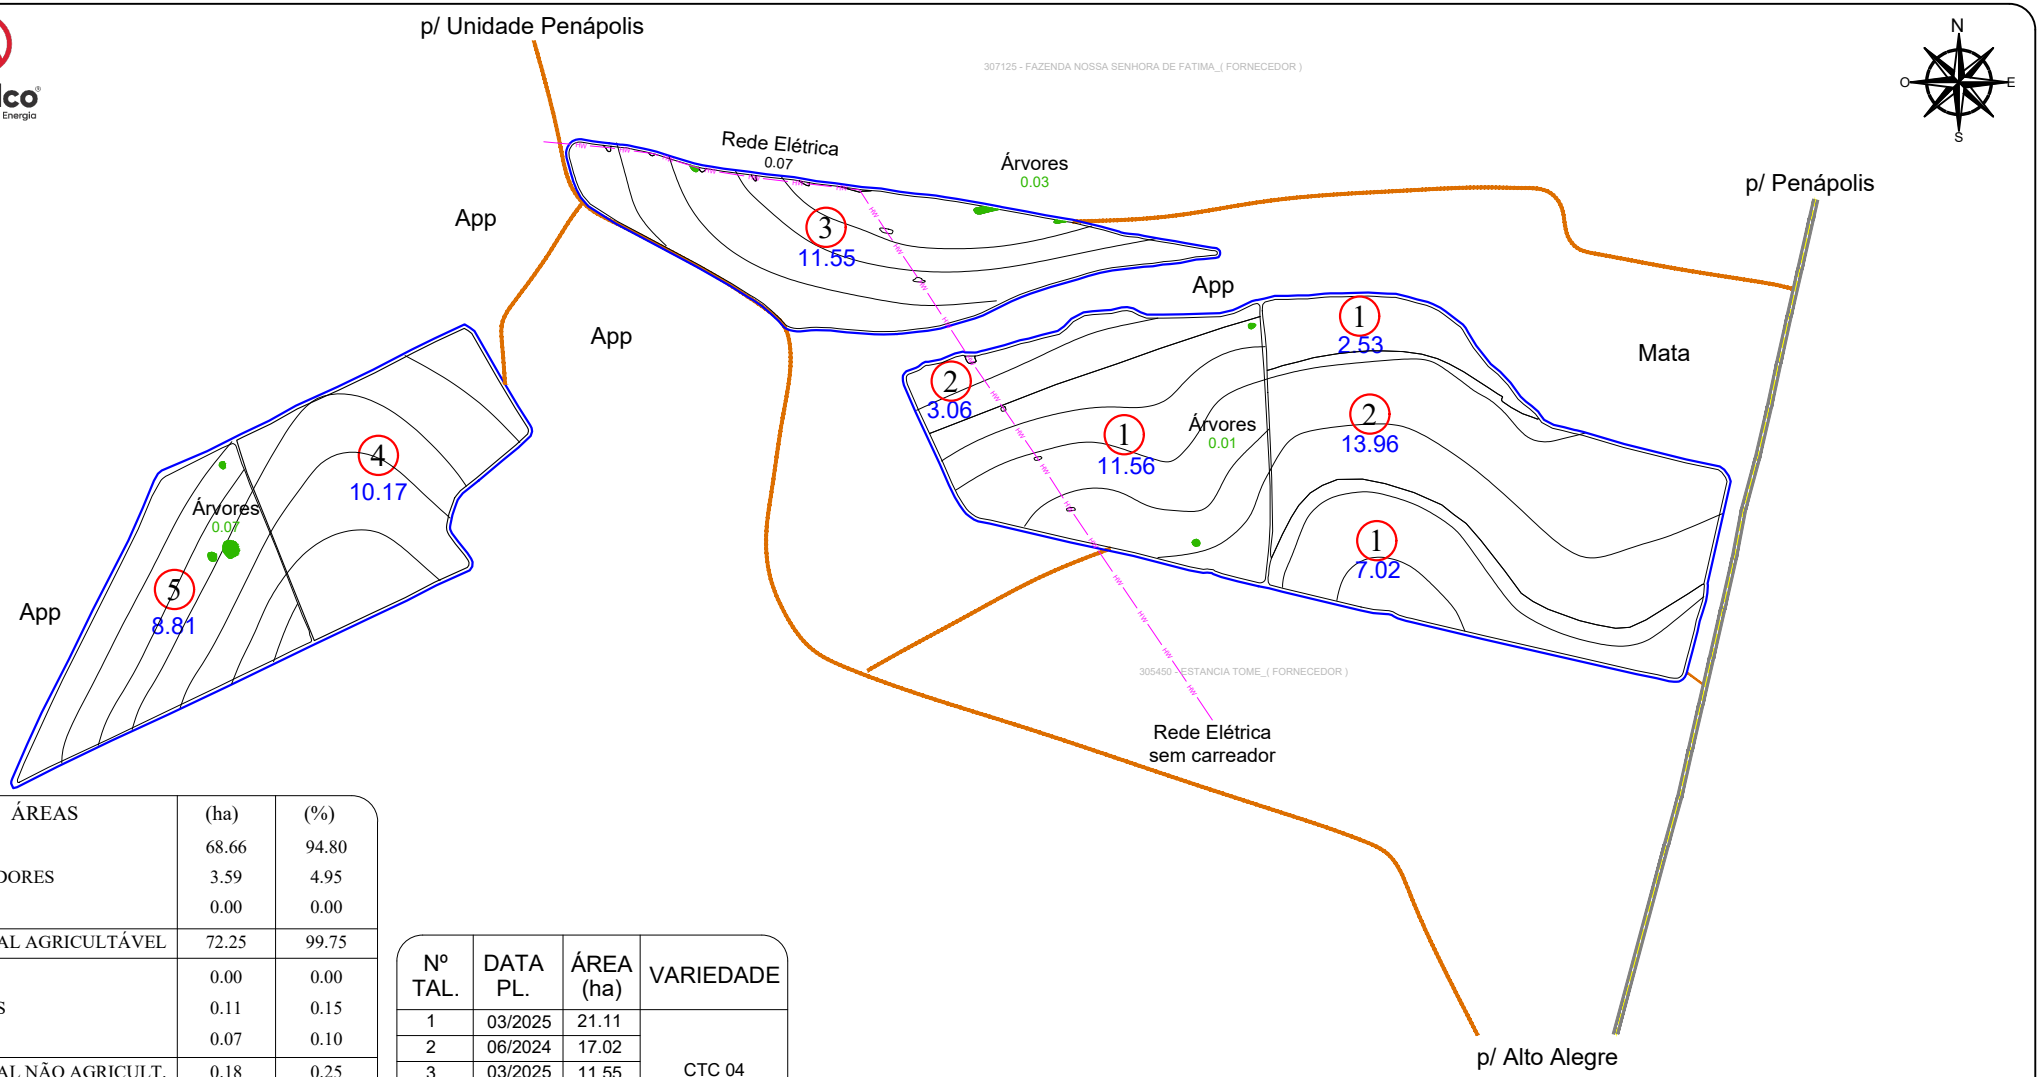


ÁREAS	(ha)	(%)
PLANTIO	68.66	94.80
CARREADORES	3.59	4.95
OUTROS	0.00	0.00
SUB TOTAL AGRICULTÁVEL	72.25	99.75
AP.P.	0.00	0.00
ÁRVORES	0.11	0.15
OUTROS	0.07	0.10
SUB TOTAL NÃO AGRICULT.	0.18	0.25
ÁREA TOTAL	72.43	100.00

C. NÍVEL: 9307.61 m/l 2.14 ha 2.96 %

Nº TAL.	DATA PL.	ÁREA (ha)	VARIEDADE
1	03/2025	21.11	CTC 04
2	06/2024	17.02	
3	03/2025	11.55	
4	05/2022	10.17	
5	03/2025	8.81	
TOTAL PLANTIO		68.66	

ESCALA: 1: 11.000

LEGENDA

- FAZENDA
- TALHÃO
- REDE ELÉTRICA
- TERRAÇO BASE LARGA
- TERRAÇO EMBUTIDO

ESPAÇAMENTO: 1.50 x 1.50
TIRO MÉDIO ESTIMADO: 000.00 m
D.V: 5.68 %

CROQUI DE ACESSO



SÍTIO SANTO ANTÔNIO

PROPRIETÁRIO: WALDEMIR CAPUTO
COMPRADOR: CLEALCO
MUNICÍPIO: ALTO ALEGRE - SP

DISTÂNCIAS (km):
UNID. I - Asfalto: 51.60 Terra.: 1.70
UNID.I I - Asfalto: 46.50 Terra.: 1.70

COORDENADAS: E(X): 588515.83 N(Y): 7615974.30
LAT: -21°33'24.8315" LONG: -50°8'42.4150"

CLEALCO - AÇÚCAR E ALCOOL S/A - DEPARTAMENTO DE GEOTECNOLOGIA

LEVANTAMENTO VIA:
SATÉLITE
GPS / VANT
GOOGLE

UNIDADE: I
PARTE: A/A
FUNDO AGRÍCOLA: 306184

M:\01-Mapa de safra\Mapas Atualizados\Terceiro\306184 - Sítio Santo Antônio (Waldemir Aparicio Caputo)\306184 - Sítio Santo Antônio (Waldemir Aparicio Caputo).dwg

Benati 12/09/2025