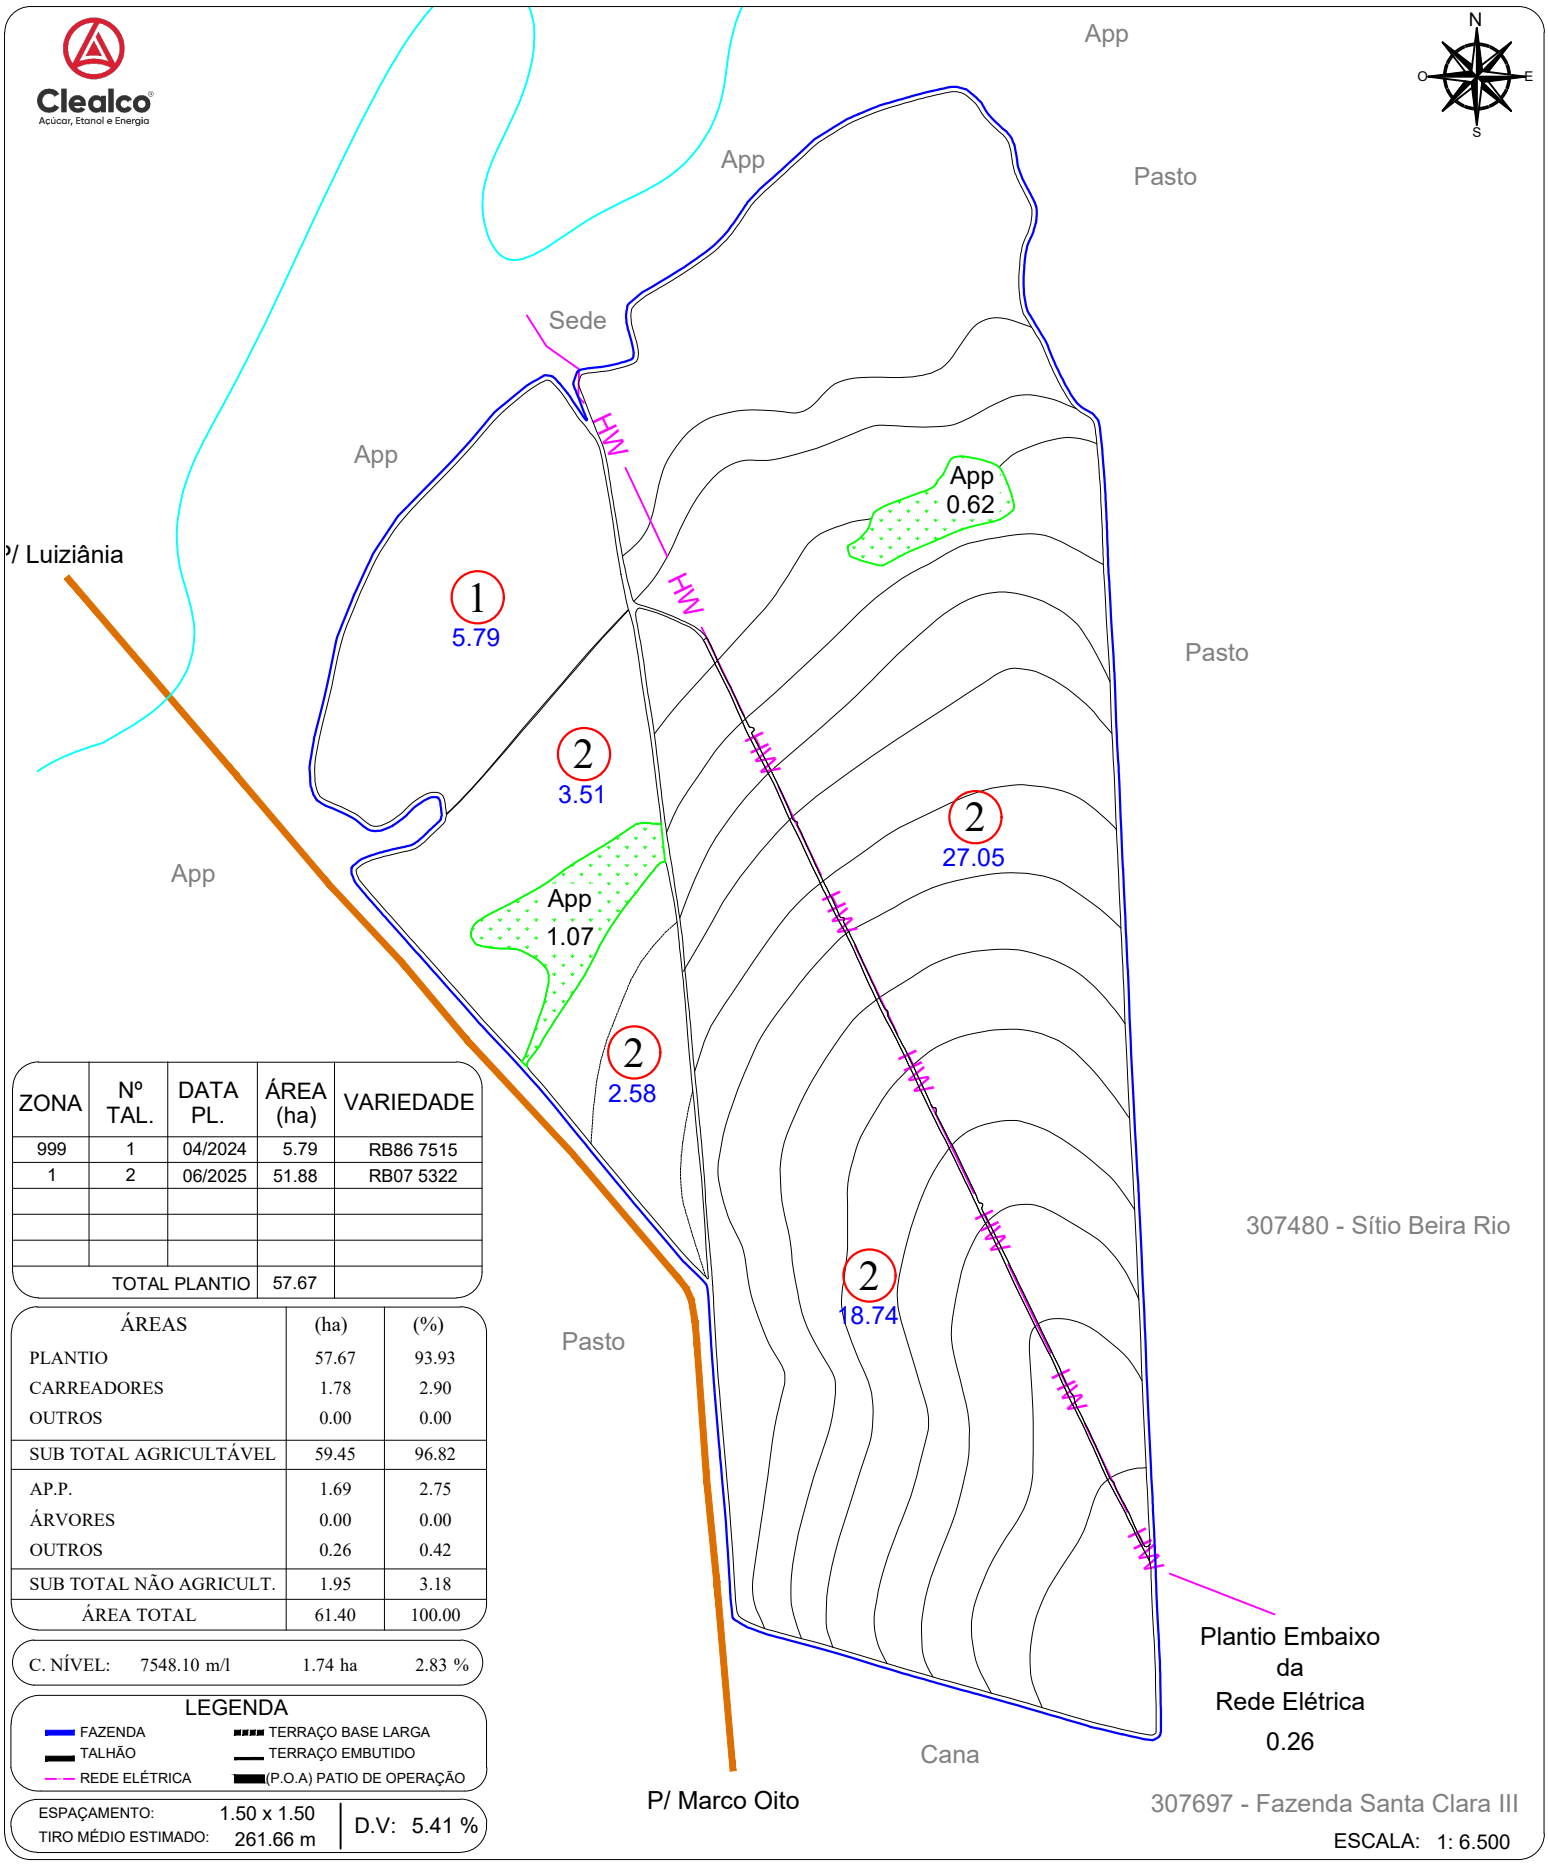


ZONA	Nº TAL.	DATA PL.	ÁREA (ha)	VARIEDADE
999	1	04/2024	5.79	RB86 7515
1	2	06/2025	51.88	RB07 5322
TOTAL PLANTIO			57.67	

ÁREAS	(ha)	(%)
PLANTIO	57.67	93.93
CARREADORES	1.78	2.90
OUTROS	0.00	0.00
SUB TOTAL AGRICULTÁVEL	59.45	96.82
AP.P.	1.69	2.75
ÁRVORES	0.00	0.00
OUTROS	0.26	0.42
SUB TOTAL NÃO AGRICULT.	1.95	3.18
ÁREA TOTAL	61.40	100.00


C. NÍVEL: 7548.10 m/l 1.74 ha 2.83 %

LEGENDA

- FAZENDA
- TALHÃO
- REDE ELÉTRICA
- TERRAÇO BASE LARGA
- TERRAÇO EMBUTIDO
- (P.O.A) PATIO DE OPERAÇÃO

ESPAÇAMENTO: 1.50 x 1.50
TIRO MÉDIO ESTIMADO: 261.66 m
D.V: 5.41 %

CROQUI DE ACESSO

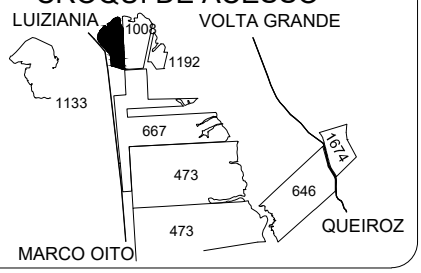

SÍTIO RANCHO ALEGRE

PROPRIETÁRIO: NIVALDO CERVIGNI JUNIOR
COMPRADOR: CLEALCO
MUNICÍPIO: QUEIROZ - SP

DISTÂNCIAS (km):
UNID. I - Asfalto: 32.50 Terra.: 7.00
UNID.I I - Asfalto: 16.50 Terra.: 17.00

COORDENADAS: E(X): 569520.76 N(Y): 7598449.70
LAT: -21°42'57.8187" LONG: -50°19'40.1752"

CLEALCO - AÇÚCAR E ALCOOL S/A - DEPARTAMENTO DE GEOTECNOLOGIA

LEVANTAMENTO VIA:
- SATÉLITE
- GPS / VANT
- GOOGLE

UNIDADE: II
PARTE: A/A
FUNDO AGRÍCOLA: 306195

M:\01-Mapa de safra\Mapas Atualizados\Terceiro\306195 - Sitio Rancho Alegre (Nivaldo Cervigni Junior)\306195 - Sitio Rancho Alegre (Nivaldo Cervigni Junior).dwg

Bruno Gamboa 29/01/26