ZONA DV	Nº TAL.	DATA PL.	ÁREA (ha)	VARIEDADE
999 5.76%	1	06/2022	12.22	CTC 04
	2		19.30	
	3		11.45	
	4		14.10	
	5		3.61	
TOTAL PLANTIO			60.68	--------


ÁREAS	(ha)	(%)
PLANTIO	60.68	96.18
CARREADORES	2.36	3.74
OUTROS	0.00	0.00
SUB TOTAL AGRICULTÁVEL	63.04	99.92
AP.P.	0.00	0.00
ÁRVORES	0.04	0.06
OUTROS	0.01	0.02
SUB TOTAL NÃO AGRICULT.	0.05	0.08
ÁREA TOTAL	63.09	100.00

C. NÍVEL: 7744.17 m/l 1.78 ha 2.82 %


LEGENDA

- FAZENDA
- TALHÃO
- CURVA DE NÍVEL
- CARREADOR
- CONFRONTANTE
- REDE ELÉTRICA
- TRAJETO VAZIO
- TRAJETO CARREGADO

PLANTIO MANUAL - ESPAÇAMENTO: 1.50 X 1.50
TIRO MÉDIO ESTIMADO: 425.26m

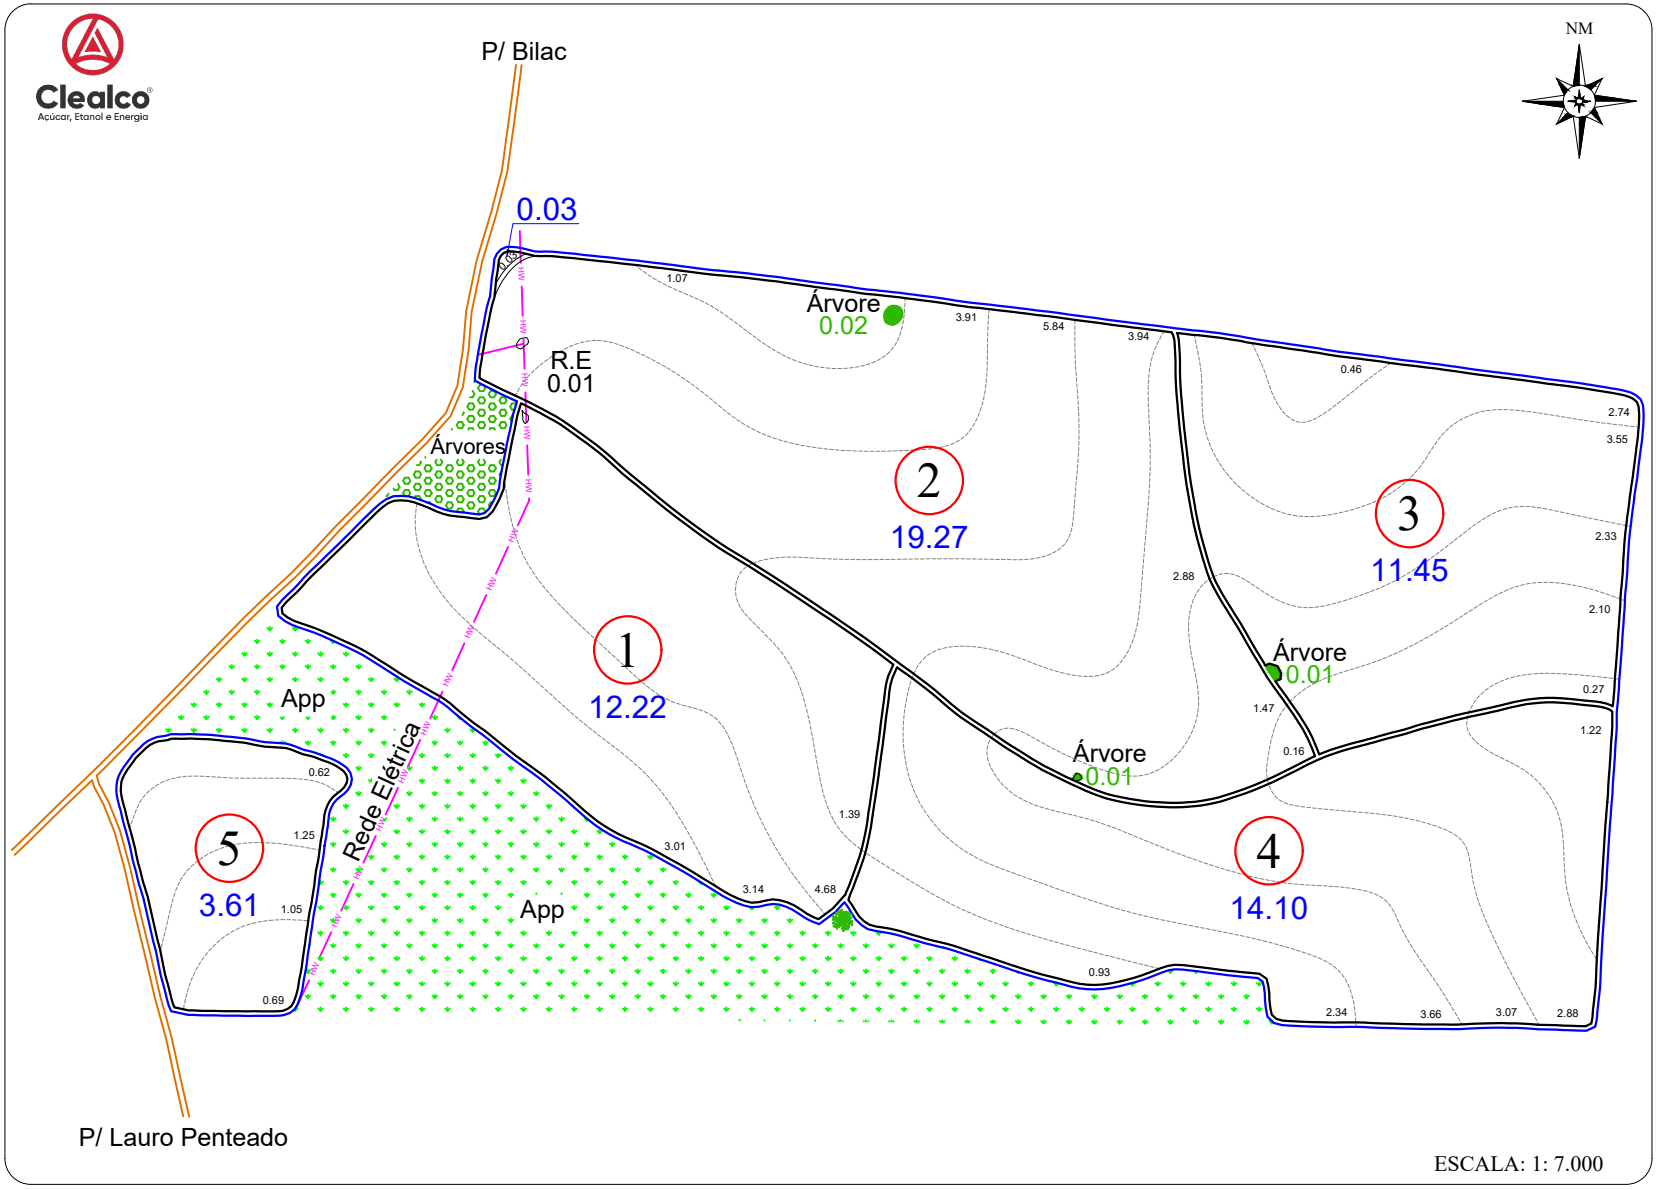

CROQUI DE ACESSO

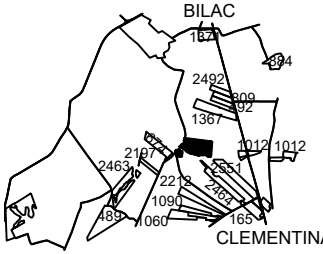

SÍTIO NOSSA SENHORA APARECIDA

PROPRIETÁRIO: PAULO BENTO BOGO
COMPRADOR: CLEALCO S/A
MUNICÍPIO: BILAC

DISTÂNCIAS (km):
UNID. I - Asfalto: 13.00 Terra.: 5.00
UNID.I I - Asfalto: 69.50 Terra.: 5.00
UNID. III -Asfalto: 55.50 Terra.: 5.00

COORDENADAS: E(X): 555436.03 N(Y): 7628875.89
LAT: -21°26'30.0041" LONG: -50°27'54.0439"

CLEALCO - AÇÚCAR E ALCOOL S/A - DEPARTAMENTO DE TOPOGRAFIA

UNIDADE: I
PARTE: A/A
FUNDO AGRÍCOLA: 306203

M:\01-Mapa de safra\Mapas Atualizados\Terceiro\306203 - Sítio Nossa Senhora de Fátima (Paulo Bento Bogo)\306203 - Sítio Nossa Senhora de Fátima (Paulo Bento Bogo).dwg

Fernanda Bezerra 16/08/22