
Clealco
Açúcar, Etanol e Energia

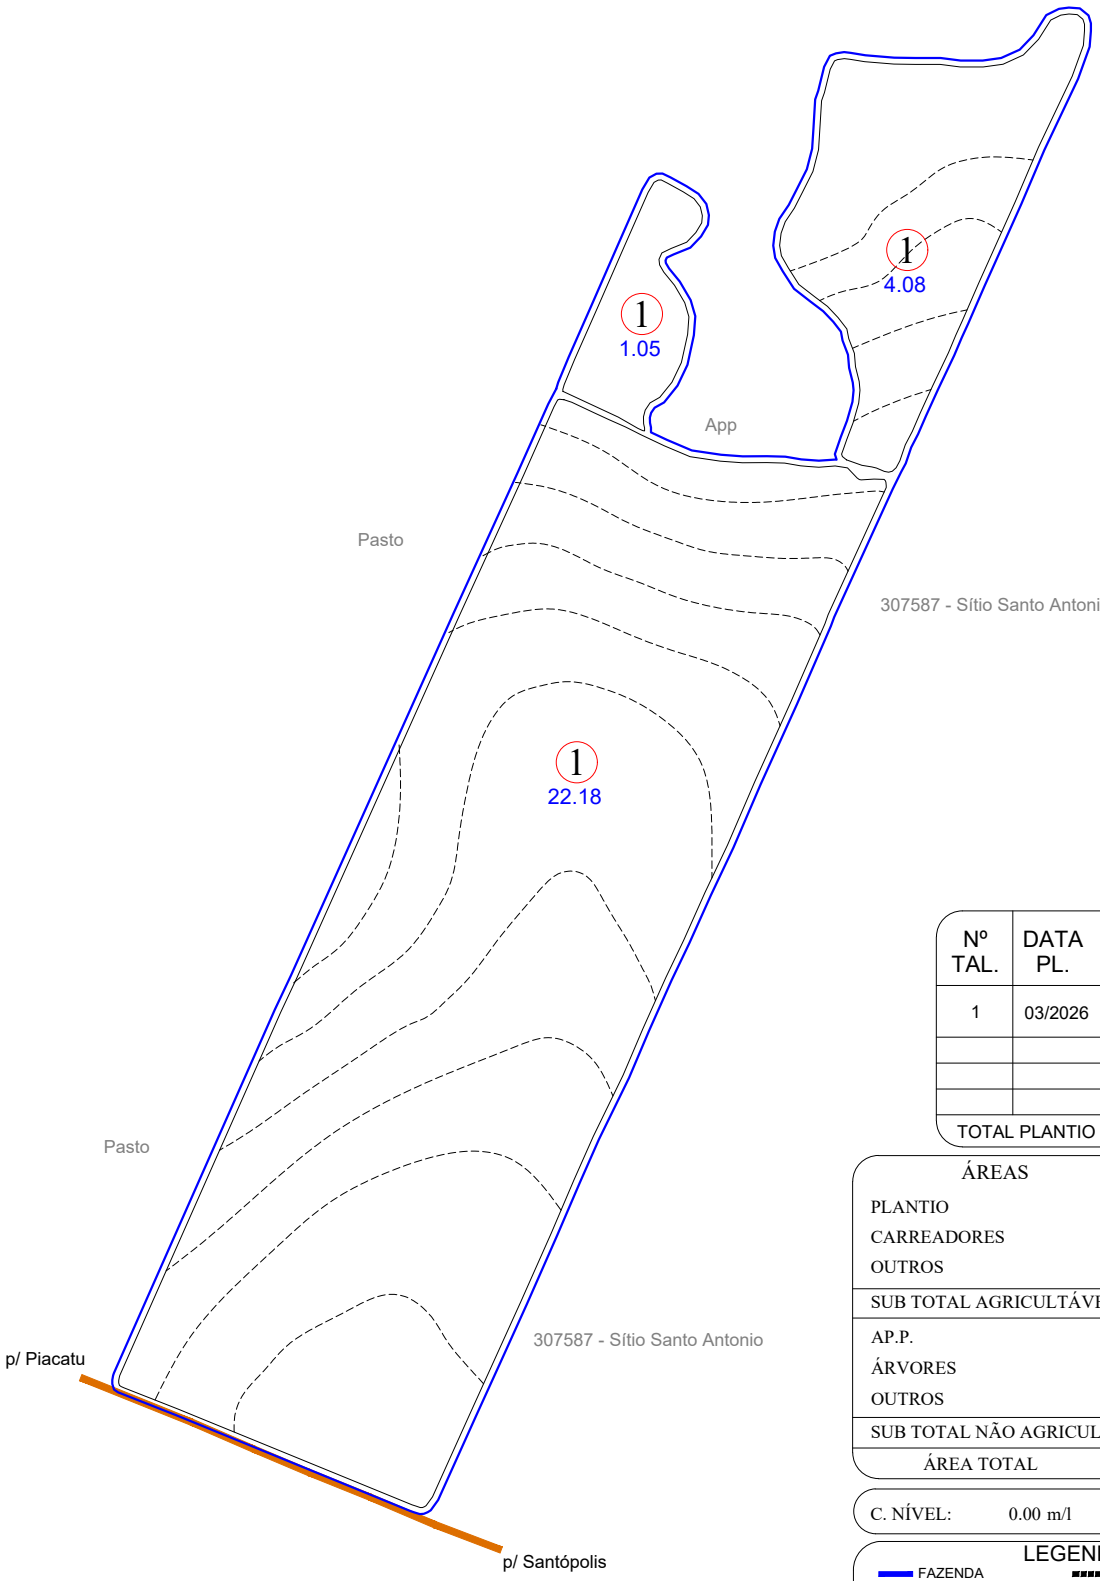

Nº TAL.	DATA PL.	ÁREA (ha)	VARIEDADE
1	03/2026	27.31	RB075322
TOTAL PLANTIO		27.31	

ÁREAS	(ha)	(%)
PLANTIO	27.31	93.68
CARREADORES	1.84	6.32
OUTROS	0.00	0.00
SUB TOTAL AGRICULTÁVEL	29.15	100.00
AP.P.	0.00	0.00
ÁRVORES	0.00	0.00
OUTROS	0.00	0.00
SUB TOTAL NÃO AGRICULT.	0.00	0.00
ÁREA TOTAL	29.15	100.00

C. NÍVEL:	0.00 m/l	0.00 ha	0.00 %


LEGENDA

- FAZENDA
- TALHÃO
- REDE ELÉTRICA
- VAZIO
- TERRAÇO BASE LARGA
- TERRAÇO EMBUTIDO
- (P.O.A) PATIO DE OPERAÇÃO
- CARREGADO

ESPAÇAMENTO: 1.50 x 1.50
TIRO MÉDIO ESTIMADO: 184.59 m
D.V: 4.79%

ESCALA: 1: 5.000

CROQUI DE ACESSO

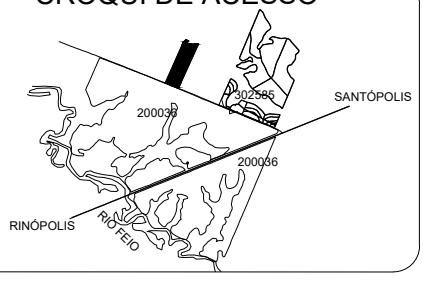

SÍTIO RECANTO ALEGRE

PROPRIETÁRIO: JOSÉ HONÓRIO GASTALDI
COMPRADOR: CLEALCO
MUNICÍPIO: SANTÓPOLIS DO AGUAPEÍ - SP

DISTÂNCIAS (km):
UNID. I - Asfalto: 18.30 Terra.: 2.24
UNID.I I - Asfalto: 55.00 Terra.: 2.24

COORDENADAS: E(X): 543624.02 N(Y): 7605427.80
LAT: -21°39'13.8327" LONG: -50°34'42.2051"

CLEALCO - AÇÚCAR E ALCOOL S/A - DEPARTAMENTO DE GEOTECNOLOGIA

LEVANTAMENTO VIA:
- SATÉLITE
- GPS / VANT
- GOOGLE

UNIDADE: I
PARTE: A/A
FUNDO AGRÍCOLA: 306212

M:\01-Mapa de safra\Mapas Atualizados\Terceiro\306212 - Sítio Recanto Alegre (Jose Honorio Gastaldi)\306212 - Sítio Recanto Alegre (Jose Honorio Gastaldi).dwg

Benati 19/06/2026