ZONA D.V.	Nº TAL.	DATA PL.	ÁREA (ha)	VARIEDADE
999 6.30 %	1	05/2023	18.43	RB 975242
	2		0.42	
TOTAL PLANTIO			18.85	--------

ÁREAS	(ha)	(%)
PLANTIO	18.85	95.23
CARREADORES	0.95	4.77
OUTROS	0.00	0.00
SUB TOTAL AGRICULTÁVEL	19.80	100.00
AP.P.	0.00	0.00
ÁRVORES	0.00	0.00
OUTROS	0.00	0.00
SUB TOTAL NÃO AGRICULT.	0.00	0.00
ÁREA TOTAL	19.80	100.00

C. NÍVEL: 1400.68 m/l 0.32 ha 1.63 %

LEGENDA

▬ FAZENDA	▬ CONFRONTANTE
▬ TALHÃO	— · — REDE ELÉTRICA
■■■■ CURVA DE NÍVEL	⇒ TRAJETO VAZIO
— CARREADOR	→ TRAJETO CARREGADO

PLANTIO MANUAL - ESPAÇAMENTO: 1.50 X 1.50
TIRO MÉDIO ESTIMADO: 267.50 m

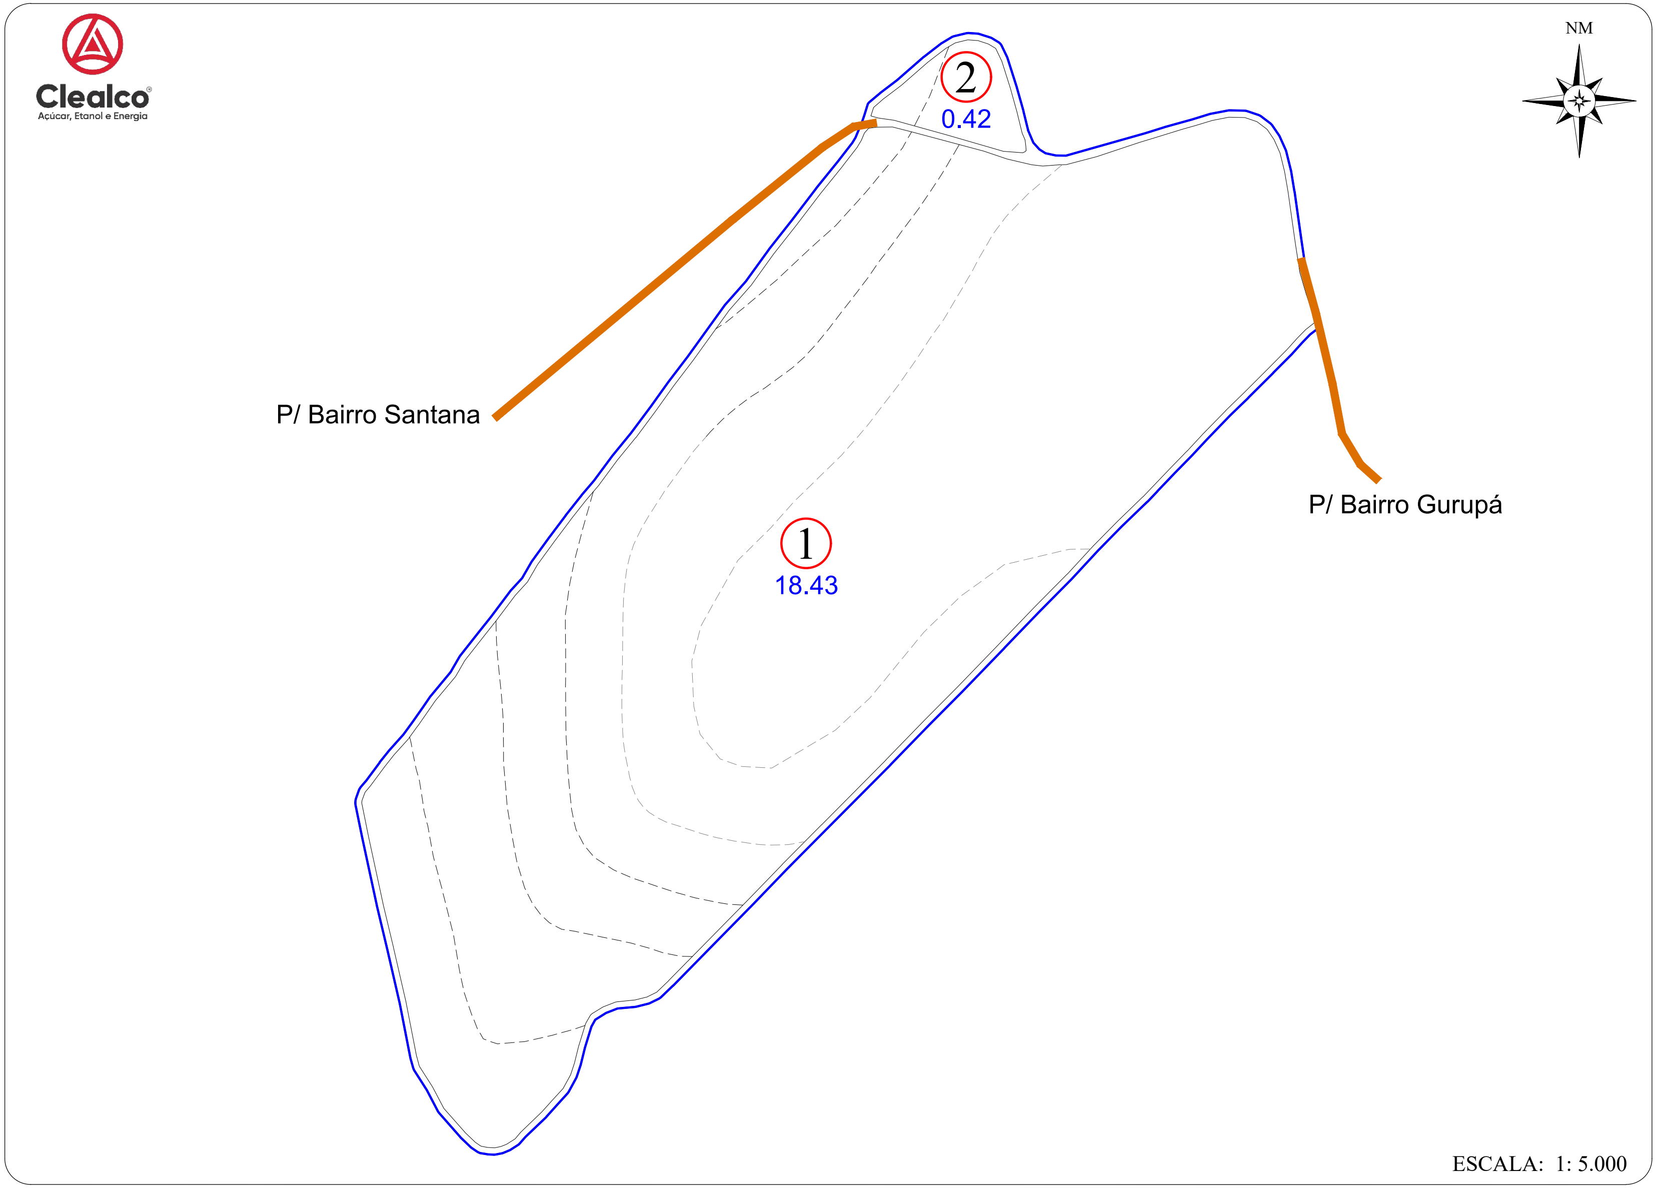

ESCALA: 1: 5.000

CROQUI DE ACESSO

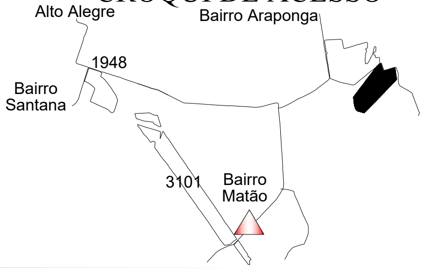

SÍTIO CABECEIRA

PROPRIETÁRIO:	JORGE LUÍZ GILBERTO
COMPRADOR:	CLEALCO S/A
MUNICÍPIO:	PENÁPOLIS

DISTÂNCIAS (km):

UNID. I - Asfalto:	61.00	Terra.:	0.00
UNID.I I - Asfalto:	51.00	Terra.:	0.00
UNID. III -Asfalto:	13.00	Terra.:	7.00

COORDENADAS: E(X): 596866.85 N(Y): 7612718.82
LAT: -21°35'9.1462" LONG: -50°3'51.4091"

CLEALCO - AÇÚCAR E ALCOOL S/A - DEPARTAMENTO DE TOPOGRAFIA

UNIDADE:
II

PARTE:
A/A

FUNDO AGRÍCOLA:
306304

M:\01-Mapa de safra\Mapas Atualizados\Terceiro\306304 - Sítio Cabeceira (Jorge Luiz Gilberto)\306304 - Sítio Cabeceira (Jorge Luiz Gilberto).dwg

Bruno Gamboa 24/01/24