
Clealco
Açúcar, Etanol e Energia

Pós Plantio

Nº TAL.	DATA PL.	ÁREA (ha)	VARIEDADE
1	05/2025	3.53	RB12 7825
2		2.78	
3		10.21	
4	04/2022	18.42	RB96 6928
6		24.31	
7	2027	48.25	PLANTIO 2027
8	04/2022	18.48	RB96 6928
9		3.60	
10		14.26	
11		26.71	
12	2027	14.79	PLANTIO 2027
13		20.90	
14		16.64	
TOTAL PLANTIO		222.88	

ÁREAS	(ha)	(%)
PLANTIO	222.88	97.06
CARREADORES	6.76	2.94
OUTROS	0.00	0.00
SUB TOTAL AGRICULTÁVEL	229.64	100.00
AP.P.	0.00	0.00
ÁRVORES	0.00	0.00
OUTROS	0.00	0.00
SUB TOTAL NÃO AGRICULT.	0.00	0.00
ÁREA TOTAL	229.64	100.00

C. NÍVEL: 22217.91 m/l 5.11 ha 2.23 %

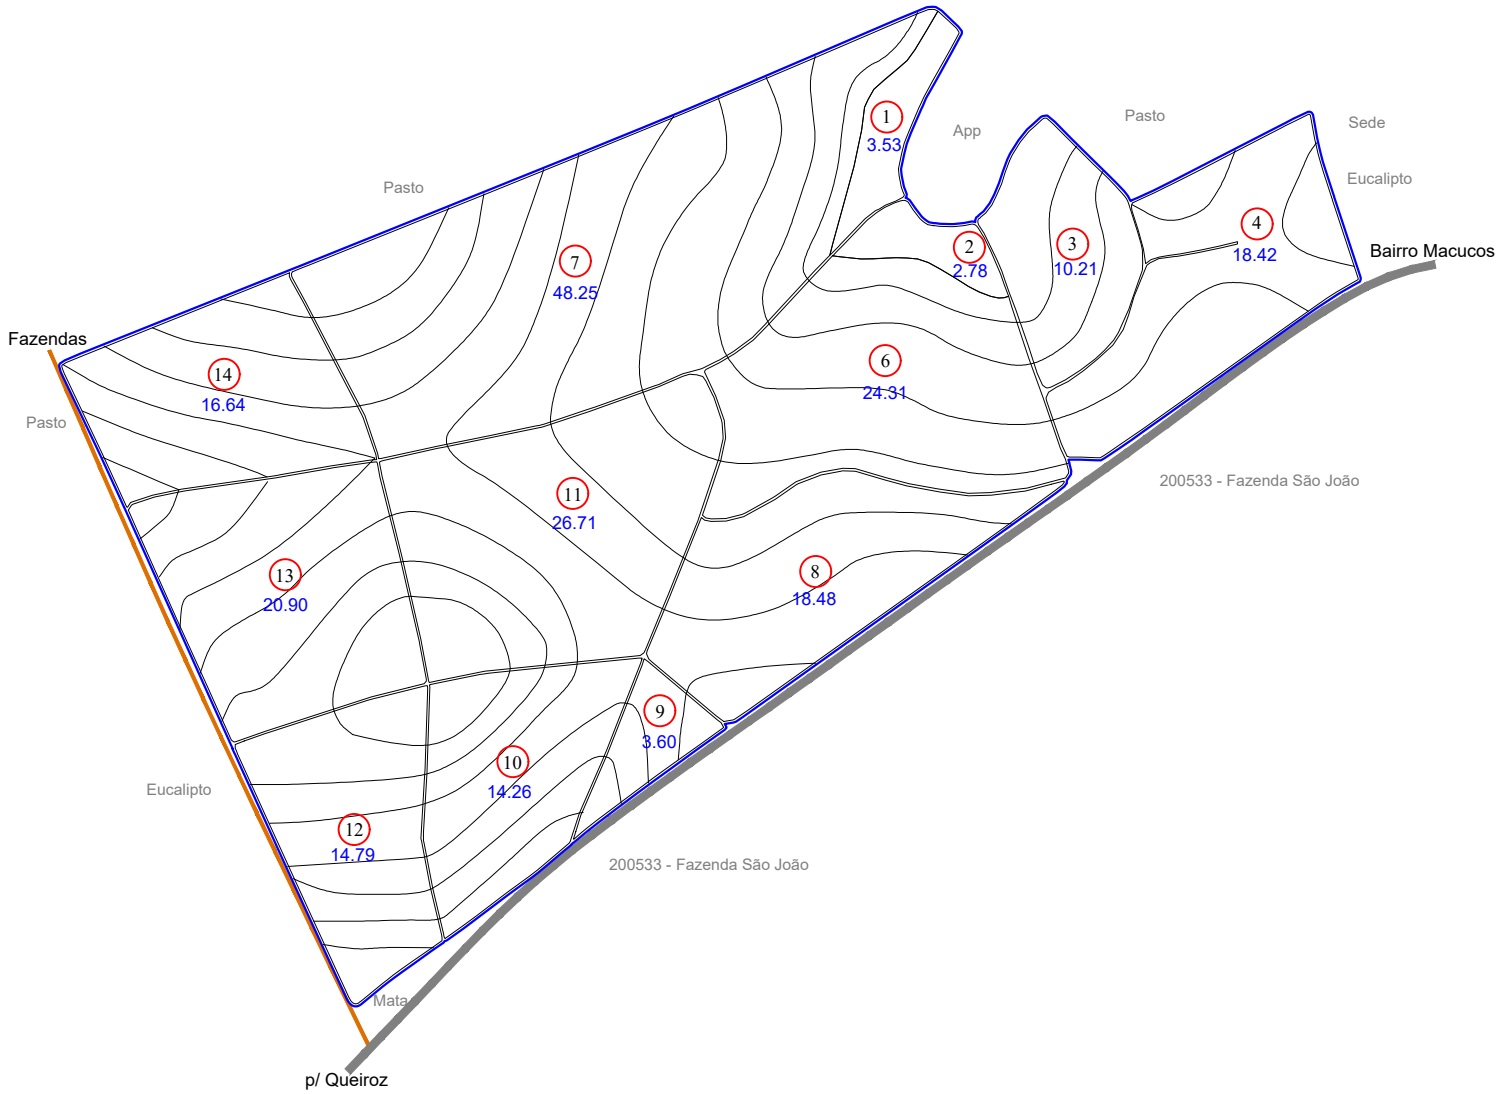


ESCALA: 1: 15.000

LEGENDA
- FAZENDA
- TALHÃO
- REDE ELÉTRICA
- TERRAÇO BASE LARGA
- TERRAÇO EMBUTIDO

ESPAÇAMENTO: 1.50 x 1.50
TIRO MÉDIO ESTIMADO: 371.06 m
D.V: 3.71%

CROQUI DE ACESSO

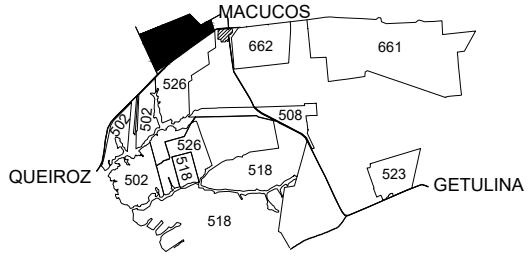

FAZENDA NOSSA SENHORA DA APARECIDA

PROPRIETÁRIO: SANDRA SOARES TOBIAS
COMPRADOR: CLEALCO S/A
MUNICÍPIO: GETULINA - SP

DISTÂNCIAS (km):
UNID. I - Asfalto: 72.50 Terra.: 2.00
UNID.I I - Asfalto: 16.00 Terra.: 2.00

COORDENADAS: E(X): 590361.91 N(Y): 7594747.28
LAT: -21°44'54.8445" LONG: -50°7'34.0814"

CLEALCO - AÇÚCAR E ALCOOL S/A - DEPARTAMENTO DE GEOTECNOLOGIA

LEVANTAMENTO VIA:
- SATÉLITE
- GPS / VANT
- GOOGLE

UNIDADE: II
PARTE: A/A
FUNDO AGRÍCOLA: 306319

M:\01-Mapa de safra\Mapas Atualizados\Terceiro\306319 - Fazenda Nossa Senhora da Aparecida (Sandra Soares Tobias)\306319 - Fazenda Nossa Senhora da Aparecida (Sandra Soares Tobias).dwg

Benati 29/07/2025