Clealco
Açúcar, Etanol e Energia

PÓS PLANTIO

D.V.	Nº TAL.	DATA PL.	ÁREA (ha)	VARIEDADE
7.95%	1	06/2024	34.54	RB86 7515
	2		85.45	
	3		12.56	
	4		9.93	
TOTAL PLANTIO			142.48	--------


ÁREAS	(ha)	(%)
PLANTIO	142.48	94.16
CARREADORES	6.46	4.27
OUTROS	0.00	0.00
SUB TOTAL AGRICULTÁVEL	148.94	98.43
AP.P.	0.00	0.00
ÁRVORES	0.07	0.05
OUTROS	2.31	1.53
SUB TOTAL NÃO AGRICULT.	2.38	1.57
ÁREA TOTAL	151.32	100.00

C. NÍVEL: 14072.18 m/l 3.24 ha 2.14 %

LEGENDA


- FAZENDA
- TALHÃO
- CURVA DE NÍVEL
- CARREADOR
- CONFRONTANTE
- REDE ELÉTRICA
- TRAJETO VAZIO
- TRAJETO CARREGADO

PLANTIO MANUAL - ESPAÇAMENTO: 1.50 X 1.50
TIRO MÉDIO ESTIMADO: 333.94 m

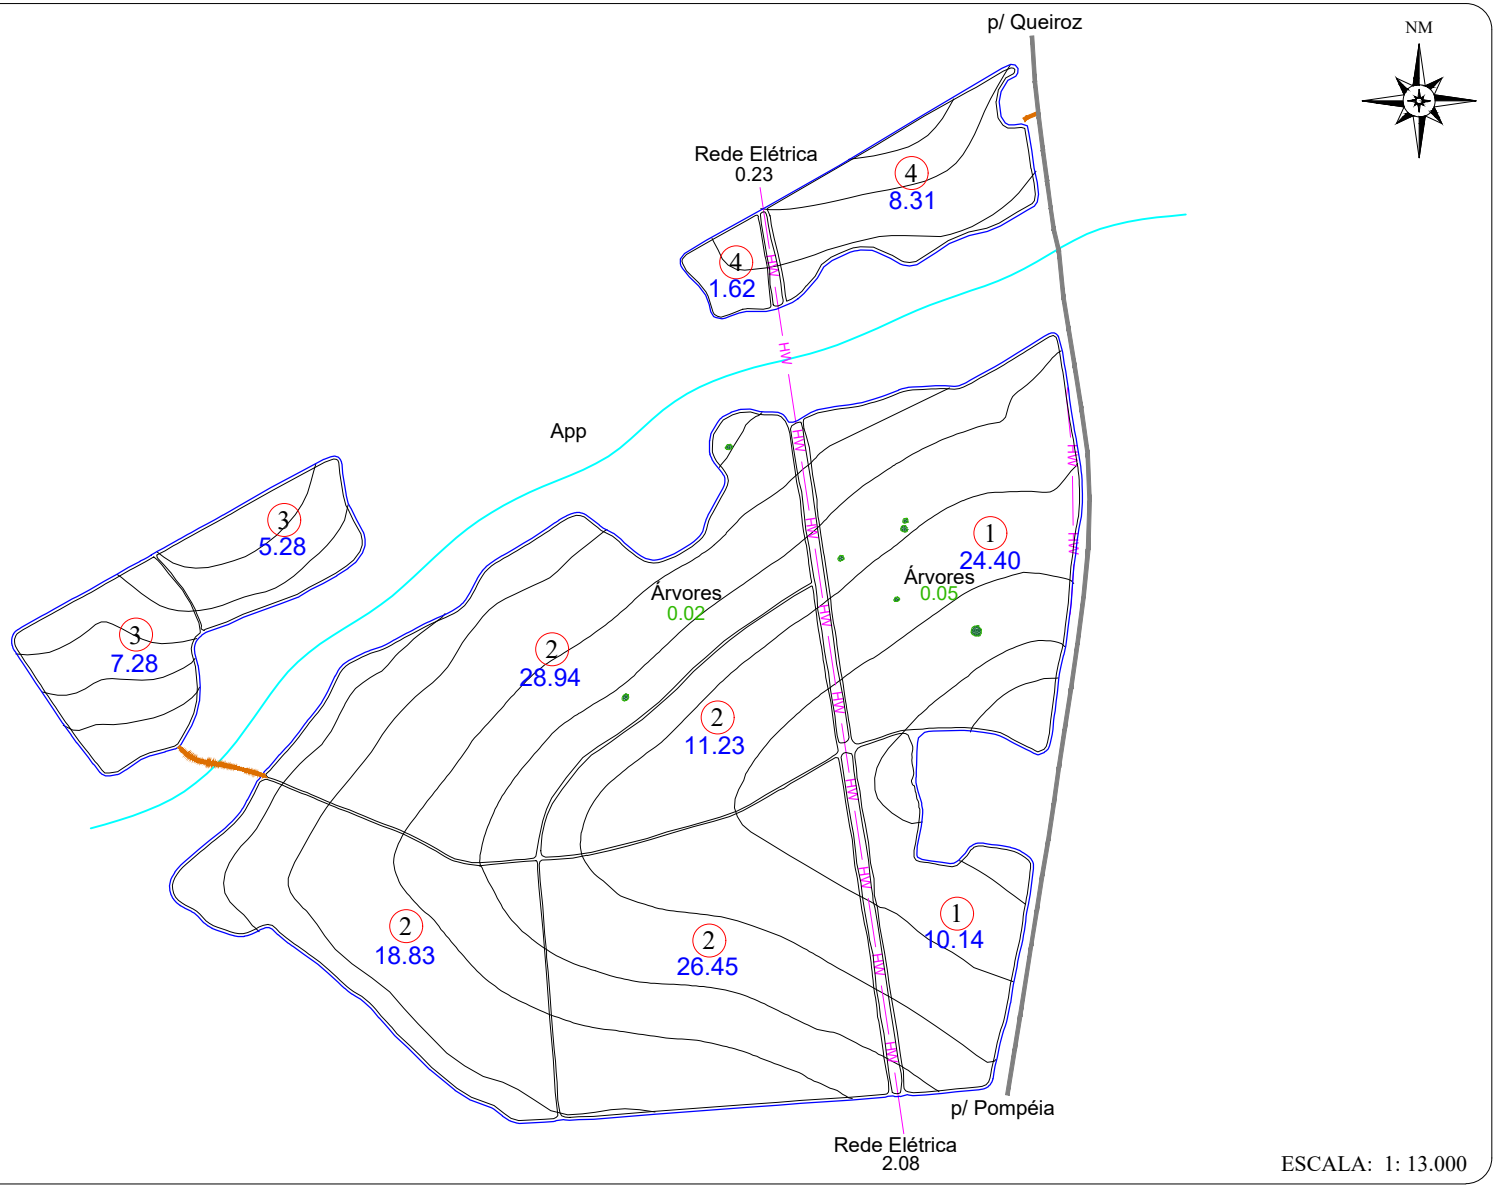

ESCALA: 1: 13.000

CROQUI DE ACESSO

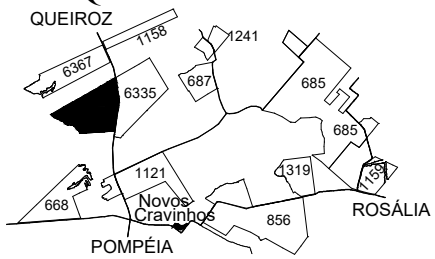

FAZENDA SÃO FRANCISCO

PROPRIETÁRIO: ADENILSON PONTIN
COMPRADOR: CLEALCO S/A
MUNICÍPIO: POMPÉIA - SP

DISTÂNCIAS (km):
UNID. I - Asfalto: 80.00 Terra.: 1.50
UNID.I I - Asfalto: 20.00 Terra.: 1.50
UNID. III -Asfalto: 101.00 Terra.: 1.50

COORDENADAS: E(X): 588095.37 N(Y): 7572243.92
LAT: -21°57'7.0970" LONG: -50°8'48.6416"

CLEALCO - AÇÚCAR E ALCOOL S/A - DEPARTAMENTO DE TOPOGRAFIA

UNIDADE: II
PARTE: A/A
FUNDO AGRÍCOLA: 306336

M:\01-Mapa de safra\Mapas Atualizados\Terceiro\306336 - Fazenda Sao Francisco (Adenilson Pontin)\306336 - Fazenda Sao Francisco (Adenilson Pontin).dwg

Benati 22/11/2024