ZONA D.V.	Nº TAL.	DATA PL.	ÁREA (ha)	VARIEDADE
999 5.90%	1	05/2023	24.21	RB 975242
	2		21.15	
	3		42.42	
TOTAL PLANTIO			87.78	--------


ÁREAS	(ha)	(%)
PLANTIO	87.78	97.20
CARREADORES	2.48	2.74
OUTROS	0.00	0.00
SUB TOTAL AGRICULTÁVEL	90.26	99.94
AP.P.	0.00	0.00
ÁRVORES	0.00	0.00
OUTROS	0.05	0.06
SUB TOTAL NÃO AGRICULT.	0.05	0.06
ÁREA TOTAL	90.31	100.00

C. NÍVEL: 14636.15 m/l 3.37 ha 3.73 %

LEGENDA


- FAZENDA
- TALHÃO
- CURVA DE NÍVEL
- CARREADOR
- CONFRONTANTE
- REDE ELÉTRICA
- TRAJETO VAZIO
- TRAJETO CARREGADO

PLANTIO MANUAL - ESPAÇAMENTO: 1.50 X 1.50
TIRO MÉDIO ESTIMADO: 313.86 m

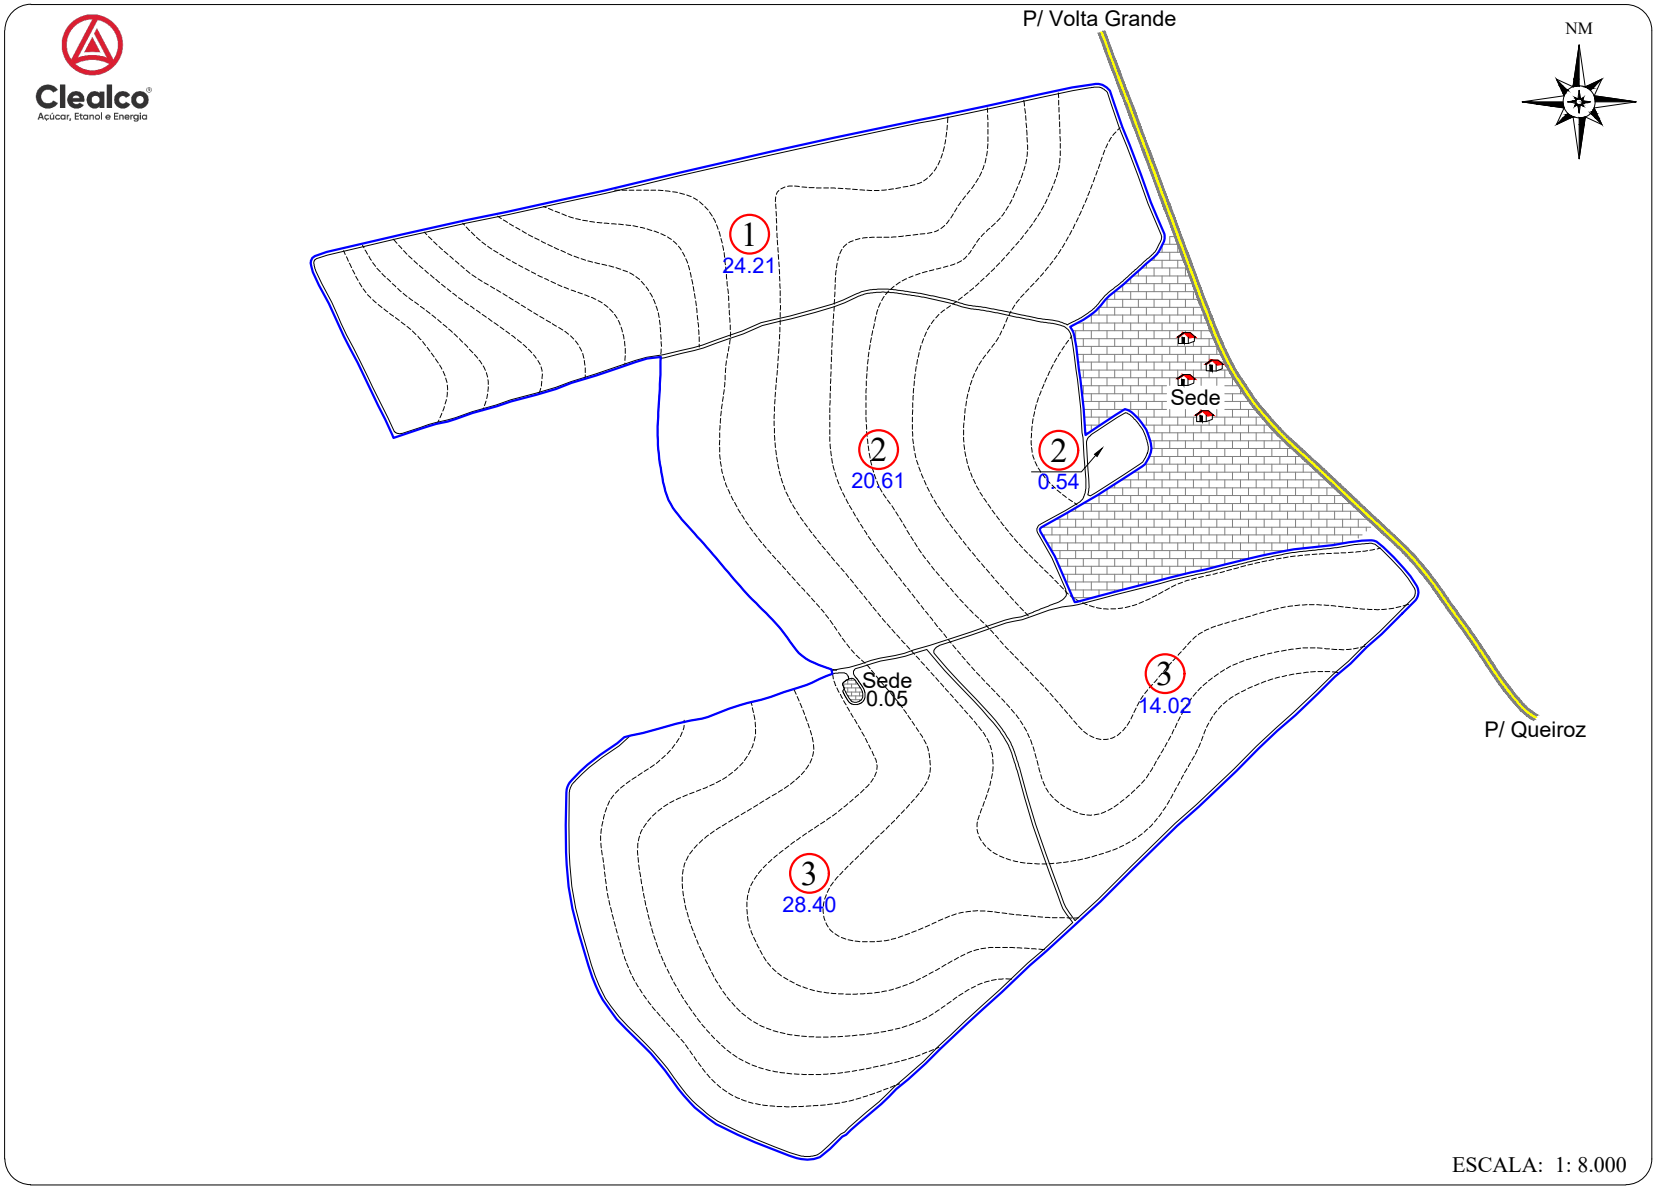

ESCALA: 1: 8.000

CROQUI DE ACESSO

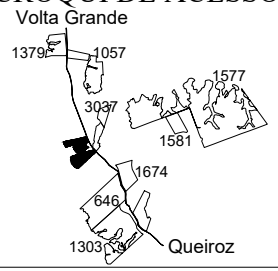

SITIO SANTA CATARINA

PROPRIETÁRIO: MARIA ALICE C. BARRETO
COMPRADOR: CLEALCO S/A
MUNICÍPIO: QUEIROZ

DISTÂNCIAS (km):
UNID. I - Asfalto: 48.50 Terra.: 0.00
UNID.I I - Asfalto: 11.70 Terra.: 0.00
UNID. III -Asfalto: 45.50 Terra.: 0.00

COORDENADAS: E(X): 573548.47 N(Y): 7596621.13
LAT: -21°43'56.7042" LONG: -50°17'19.6973"

CLEALCO - AÇÚCAR E ALCOOL S/A - DEPARTAMENTO DE TOPOGRAFIA

UNIDADE: II
PARTE: A/A
FUNDO AGRÍCOLA: 306350