
Clealco
Açúcar, Etanol e Energia

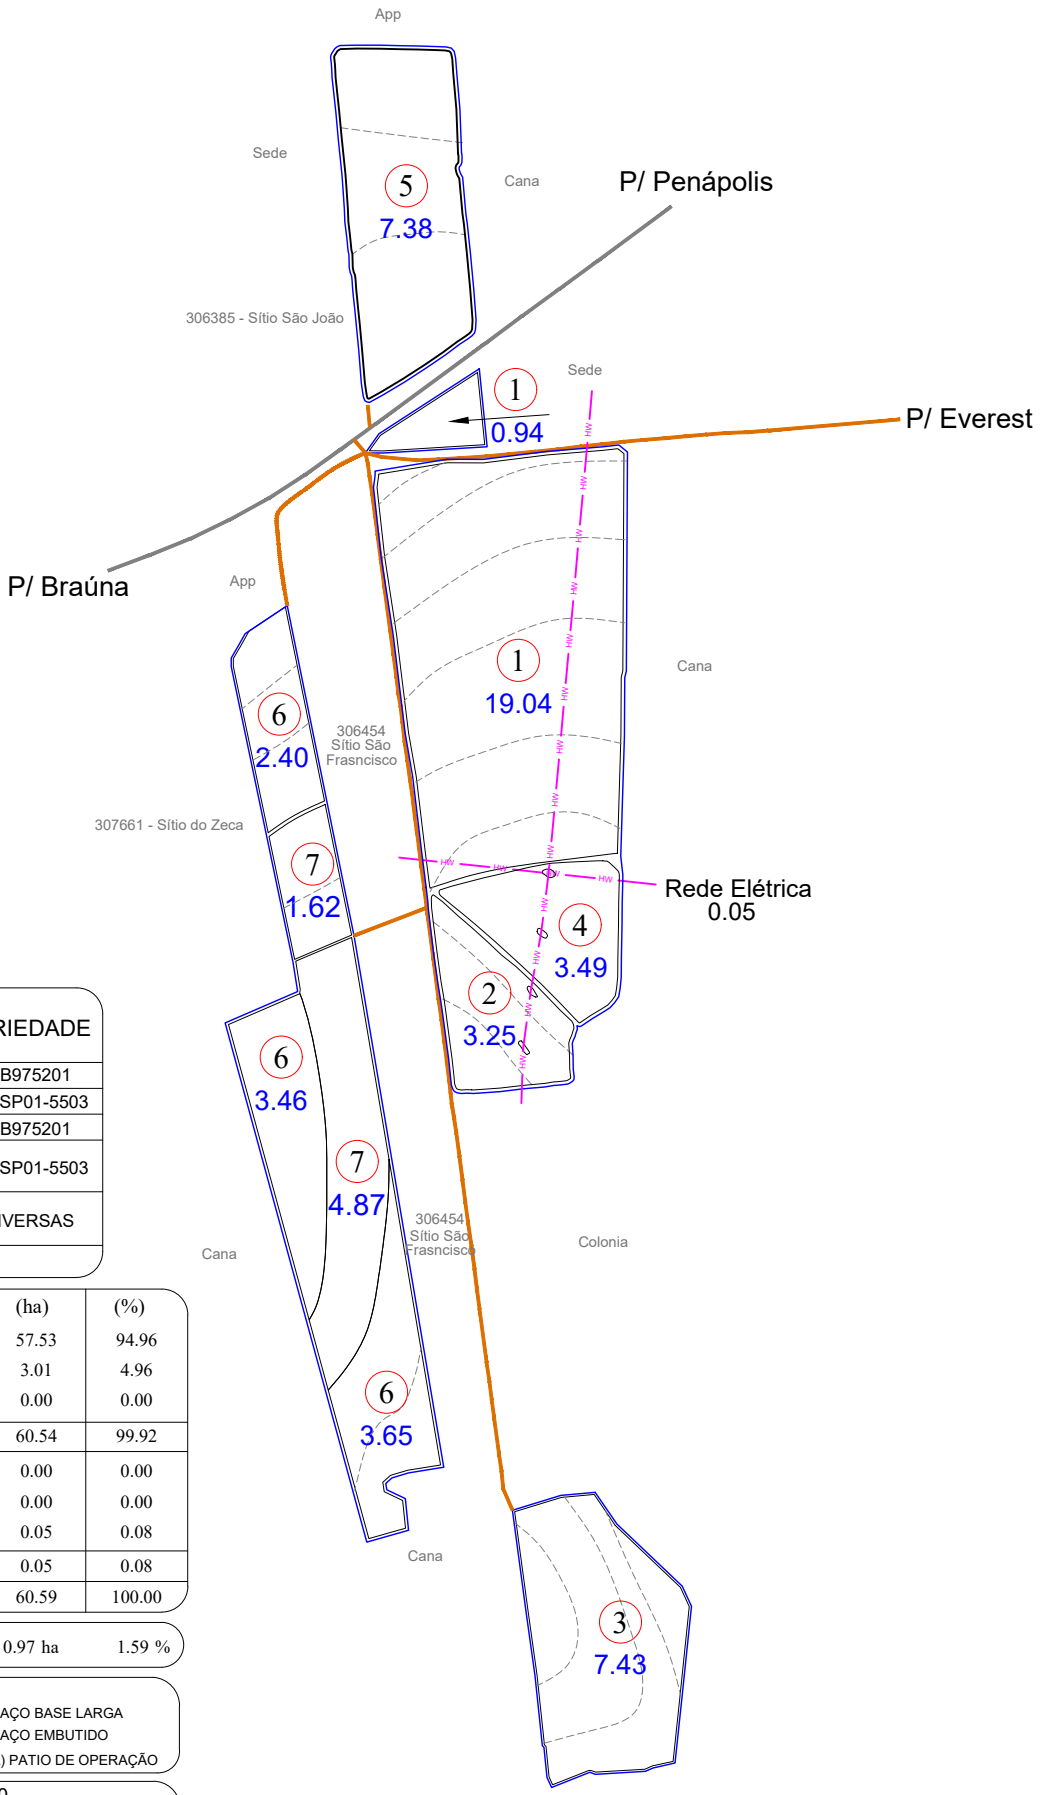

Nº TAL.	DATA PL.	ÁREA (ha)	VARIEDADE
1	03/2020	19.98	RB975201
2	2026	3.25	IACSP01-5503
3	03/2020	7.43	RB975201
4	2026	3.49	IACSP01-5503
5		7.38	
6	04/2025	9.51	DIVERSAS
7	04/2024	6.49	
TOTAL PLANTIO		57.53	

ÁREAS	(ha)	(%)
PLANTIO	57.53	94.96
CARREADORES	3.01	4.96
OUTROS	0.00	0.00
SUB TOTAL AGRICULTÁVEL	60.54	99.92
AP.P.	0.00	0.00
ÁRVORES	0.00	0.00
OUTROS	0.05	0.08
SUB TOTAL NÃO AGRICULT.	0.05	0.08
ÁREA TOTAL	60.59	100.00

C. NÍVEL: 4199.79 m/l 0.97 ha 1.59 %


LEGENDA

- FAZENDA
- TALHÃO
- REDE ELÉTRICA
- TERRAÇO BASE LARGA
- TERRAÇO EMBUTIDO
- (P.O.A) PATIO DE OPERAÇÃO

ESPAÇAMENTO: 1.50 x 1.50
TIRO MÉDIO ESTIMADO: 205.27 m
D.V: 3.45 %

ESCALA: 1: 11.000

CROQUI DE ACESSO

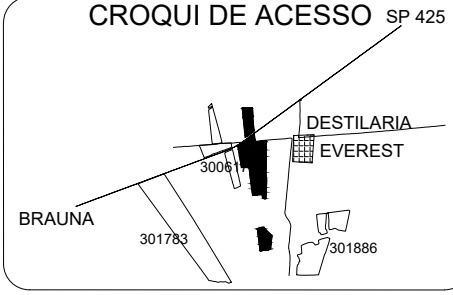

SITIO SAO PEDRO

PROPRIETÁRIO: NILTON CEZÁRIO ANNELLI
COMPRADOR: CLEALCO
MUNICÍPIO: PENÁPOLIS- SP

DISTÂNCIAS (km):
UNID. I - Asfalto: 31.00 Terra.: 0.50
UNID.I I - Asfalto: 71.80 Terra.: 0.00

COORDENADAS: E(X): 582336.89 N(Y): 7624542.32
LAT: -21°28'47.2355" LONG: -50°12'18.7487"

CLEALCO - AÇÚCAR E ALCOOL S/A - DEPARTAMENTO DE GEOTECNOLOGIA

LEVANTAMENTO VIA:
- SATÉLITE
- GPS / VANT
- GOOGLE

UNIDADE: I
PARTE: A/A
FUNDO AGRÍCOLA: 306352

M:\01-Mapa de safra\Mapas Atualizados\Terceiro\306352 - Sitio São Pedro (Nilton Cezário Annelli)\306352 - Sitio São Pedro (Nilton Cezário Annelli).dwg

Benati 07/07/2026