
Clealco
Açúcar, Etanol e Energia

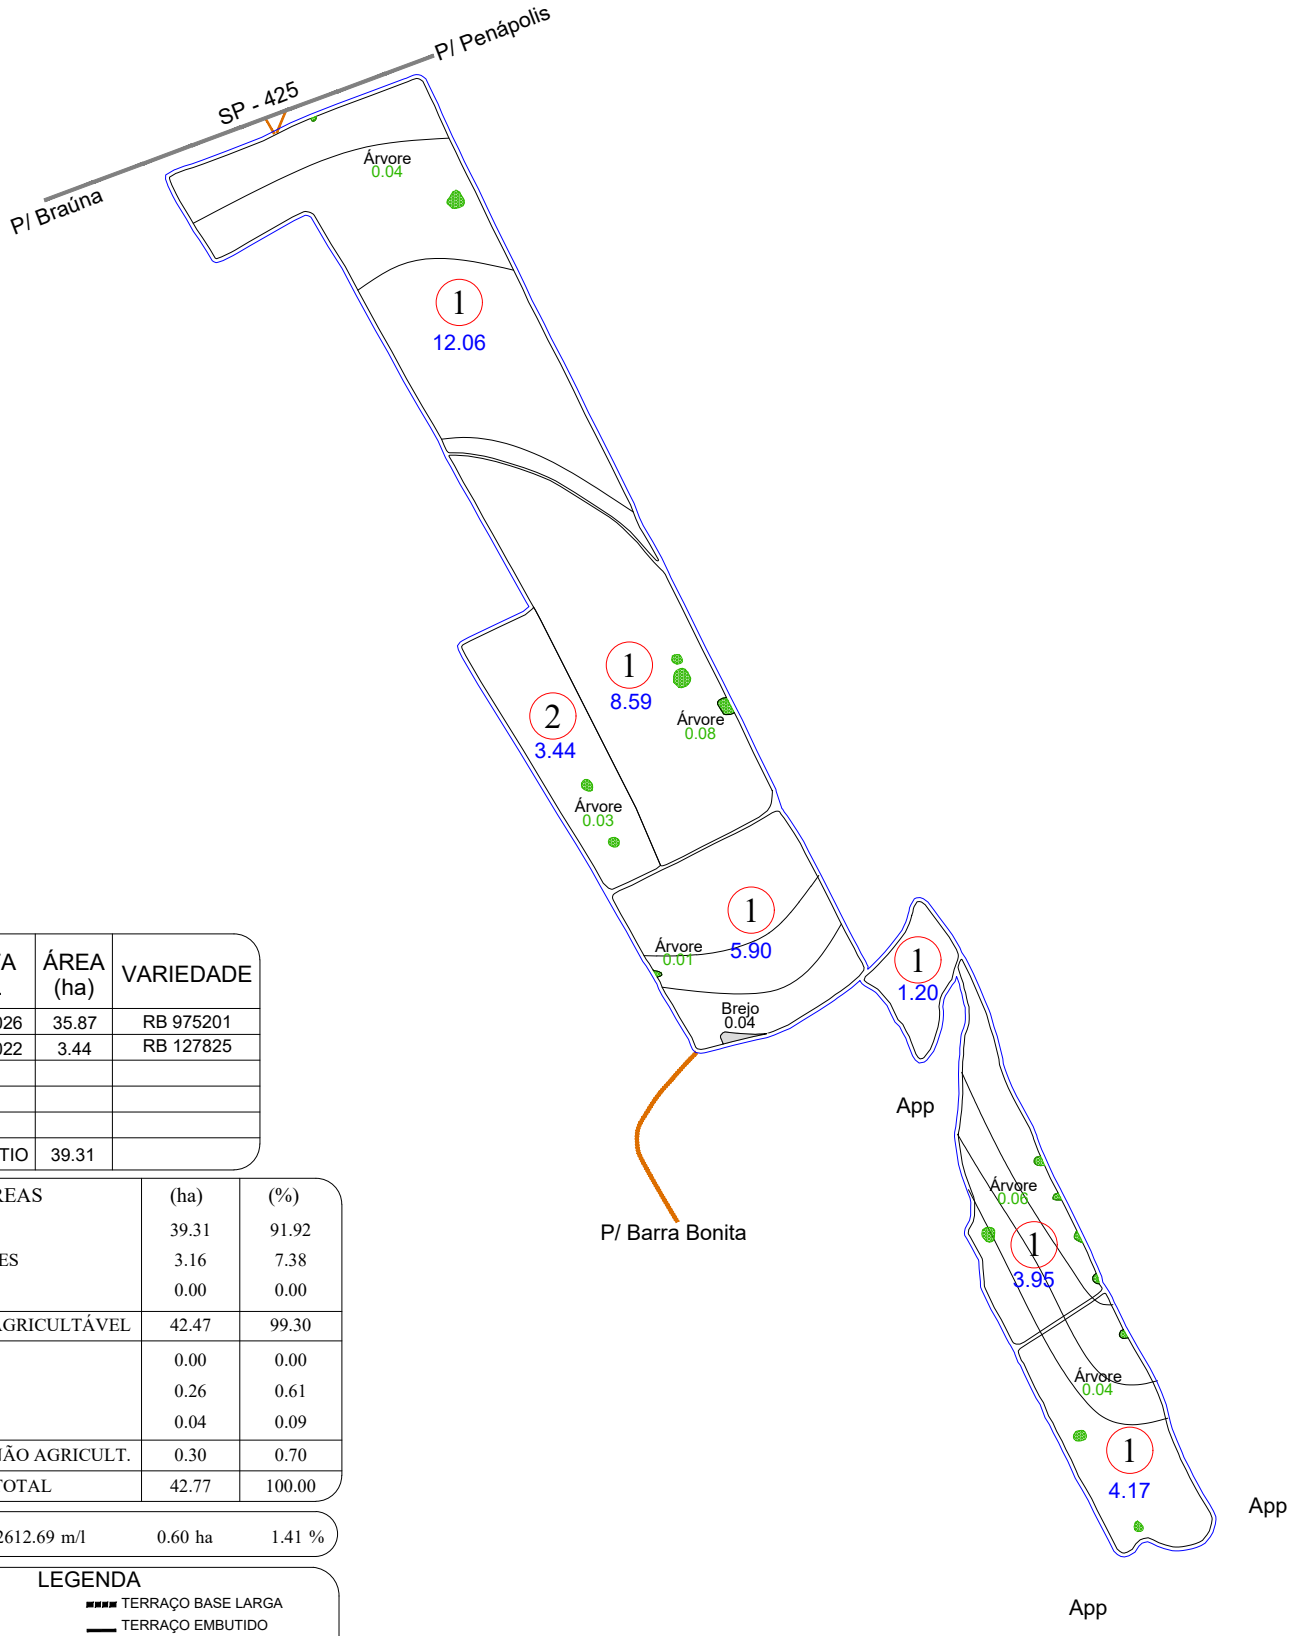

Nº TAL.	DATA PL.	ÁREA (ha)	VARIEDADE
1	03/2026	35.87	RB 975201
2	04/2022	3.44	RB 127825
TOTAL PLANTIO		39.31	

ÁREAS	(ha)	(%)
PLANTIO	39.31	91.92
CARREADORES	3.16	7.38
OUTROS	0.00	0.00
SUB TOTAL AGRICULTÁVEL	42.47	99.30
AP.P.	0.00	0.00
ÁRVORES	0.26	0.61
OUTROS	0.04	0.09
SUB TOTAL NÃO AGRICULT.	0.30	0.70
ÁREA TOTAL	42.77	100.00

C. NÍVEL: 2612.69 m/l 0.60 ha 1.41 %


LEGENDA

- FAZENDA
- TALHÃO
- REDE ELÉTRICA
- TERRAÇO BASE LARGA
- TERRAÇO EMBUTIDO
- (P.O.A) PATIO DE OPERAÇÃO

ESPAÇAMENTO: 1.50 x 1.50
TIRO MÉDIO ESTIMADO: 000.00 m
D.V: 0.00 %

ESCALA: 1: 10.000

CROQUI DE ACESSO

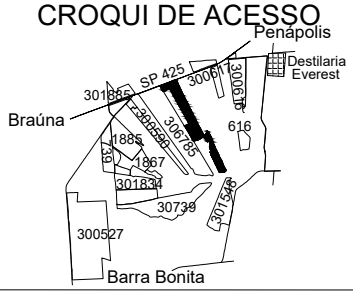

SÍTIO SANTO ANTÔNIO

PROPRIETÁRIO: NILTON CEZÁRIO ANNELLI
COMPRADOR: CLEALCO
MUNICÍPIO: PENÁPOLIS - SP

DISTÂNCIAS (km):
UNID. I - Asfalto: 31.00 Terra.: 1.00
UNID.I I - Asfalto: 31.70 Terra.: 19.50

COORDENADAS: E(X): 581507.50 N(Y): 7622799.77
LAT: -21°29'44.0454" LONG: -50°12'47.2637"

CLEALCO - AÇÚCAR E ALCOOL S/A - DEPARTAMENTO DE GEOTECNOLOGIA

LEVANTAMENTO VIA:
- SATÉLITE
- GPS / VANT
- GOOGLE

UNIDADE: I
PARTE: A/A
FUNDO AGRÍCOLA: 306353

M:\01-Mapa de safra\Mapas Atualizados\Terceiro\306353 - Sítio Santo Antonio (Nilton Cezario Annelli)\306353 - Sítio Santo Antonio (Nilton Cezario Annelli).dwg

Benati 19/06/2026